


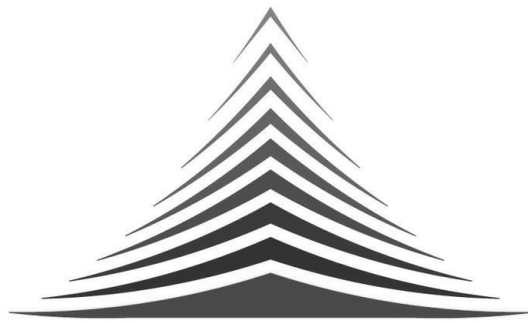

ASSET WORLD CORPORATION

THE OKURA PRESTIGE SUKHUMVIT
BANGKOK HOTEL AND SPA

เจ้าของโครงการ:
LUXURY HOTEL DEVELOPMENT SUKHUMVIT 38
CO., LTD

ที่ตั้งโครงการ:
Sukhumvit Road, Alley 38, Khlong Toei,
Bangkok 10110, Thailand

DRAWING SET

- แบบสถาปัตยกรรม
Architecture
- แบบสถาปัตยกรรมภายใน
Interior
- แบบวิศวกรรมโยธา
Civil
- แบบภูมิสถาปัตยกรรม
Landscape
- แบบวิศวกรรมโครงสร้าง
Structure
- แบบวิศวกรรมระบบปรับอากาศและระบายอากาศ
Mechanical
- แบบวิศวกรรมระบบสุขาภิบาล
Sanitary
- แบบวิศวกรรมระบบป้องกันอัคคีภัย
Fire Protection
- แบบวิศวกรรมไฟฟ้าและสื่อสาร
Electrical

ISSUED OF PACKAGE

- แบบเพื่อการประสานงาน
Co-Ordination
- แบบขออนุญาตปลูกสร้าง
Authority Submittal
- แบบประกวดราคา
Bidding Document
- แบบคู่สัญญาก่อสร้าง
Contract Document
- แบบก่อสร้าง
Construction Document
- แบบเพื่อประกอบรายงานวิเคราะห์ผลกระทบสิ่งแวดล้อม
Environmental Impact Assessment

ISSUED DATE

17/04/2569

SHEET NO.	SHEET NAME
A0_ข้อมูลทั่วไป	
A0.00	แผ่นปก
A0.02	แผนที่สิ่งเขป,ผังโหนดที่ดิน
A0.03	สัญลักษณ์มาตรฐาน,มาตรฐานคำย่อ,กำหนดหลักเกณฑ์ในการก่อสร้าง
A0.04	มาตรฐานป้องกันความปลอดภัย
A0.05	แบบผนัง (WALL TYPE)
A0.06	รายการวัสดุ
A0.07	รายการวัสดุ
A0.08	ผังบริเวณ

A1_ผังพื้นอาคาร	
A1.01	ผังพื้นชั้น B2
A1.02	ผังพื้นชั้น B1
A1.04	ผังพื้นชั้น G
A1.05	ผังพื้นชั้น 1
A1.06	ผังพื้นชั้น 1A
A1.07	ผังพื้นชั้น 2
A1.08	ผังพื้นชั้น 2A
A1.09	ผังพื้นชั้น 2B
A1.10	ผังพื้นชั้น 3
A1.11	ผังพื้นชั้น 3A
A1.12	ผังพื้นชั้น 4
A1.13	ผังพื้นชั้น 4A
A1.14	ผังพื้นชั้น 5
A1.15	ผังพื้นชั้น 6 (BALLROOM)
A1.16	ผังพื้นชั้น 6A
A1.17	ผังพื้นชั้น 7
A1.18	ผังพื้นชั้น 8 (GUESTROOM)
A1.19	ผังพื้นชั้น 9-12A (GUESTROOM)
A1.20	ผังพื้นชั้น 14 (GUESTROOM)
A1.21	ผังพื้นชั้น 15-18 (GUESTROOM)
A1.22	ผังพื้นชั้น 19-22 (GUESTROOM)
A1.23	ผังพื้นชั้น 23 (GUESTROOM)
A1.24	ผังพื้นชั้น 24 (ALL DAY DINING)
A1.25	ผังพื้นชั้น 25 (WELLNESS)
A1.26	ผังพื้นชั้น 26
A1.27	ผังพื้นชั้น 27 (SWIMMING POOL)
A1.28	ผังพื้นชั้น 28 (LOBBY)
A1.29	ผังพื้นชั้น 29
A1.30	ผังพื้นชั้นคาดฟ้า
A1.31	ผังพื้นชั้น 10x10
A4.01.1	SCOPE OF WORK ผังพื้นชั้น G

A2_รูปด้านอาคาร	
A2.01	รูปด้าน 1
A2.02	รูปด้าน 2
A2.03	รูปด้าน 3

A3_รูปตัดอาคาร	
A3.01	รูปตัด 1
A3.02	รูปตัด 2
A3.03	รูปตัด 3

A6_แบบขยายผังพื้นที่เฉพาะส่วนและรูปด้านภายใน	
A6.01.01	แบบขยายห้องน้ำ T-B201, T-B101, T-G01-03
A6.01.02	แบบขยายห้องน้ำ T-G04, T-2A01, T-601-03
A6.01.03	แบบขยายห้องน้ำ T-604, T-701-02, T-703-04
A6.01.04	แบบขยายห้องน้ำ TYP1 , TYP2, T-2401-02
A6.01.05	แบบขยายห้องน้ำ T-2401-02, T-2403-05
A6.01.07	แบบขยายห้องน้ำ T-2701-02, T-2801-03
A6.01.08	แบบขยายห้องน้ำ T-2901-02, T-3001-03
A6.01.09	มาตรฐานการติดตั้งสุขภัณฑ์
A6.01.10	มาตรฐานการติดตั้งสุขภัณฑ์
A6.01.11	มาตรฐานการติดตั้งสุขภัณฑ์
A6.01.12	มาตรฐานการติดตั้งสุขภัณฑ์
A6.01.13	มาตรฐานการติดตั้งสุขภัณฑ์
A6.02.02	แบบขยายลิฟต์จอดรถอัตโนมัติ
A6.02.03	แบบขยายลิฟต์จอดรถอัตโนมัติ
A6.02.04	แบบขยายลิฟต์จอดรถอัตโนมัติ

A7_แบบขยายทางสัญจร	
A7.01.01	แบบขยายบันได ST-01
A7.01.02	แบบขยายบันได ST-01
A7.01.03	แบบขยายบันได ST-01
A7.01.04	แบบขยายบันได ST-01
A7.01.05	แบบขยายบันได ST-01
A7.01.07	แบบขยายบันได ST-02
A7.01.08	แบบขยายบันได ST-02

SHEET NO.	SHEET NAME
A7.01.09	แบบขยายบันได ST-02
A7.01.10	แบบขยายบันได ST-02
A7.01.12	แบบขยายบันได ST-03, ST-04
A7.01.13	แบบขยายบันได ST-05
A7.02.01	แบบขยายทางลาด R-01,R-02,R-03
A7.02.02	แบบขยายทางลาด R-04, R-05
A7.02.03	แบบขยายทางลาด R-06
A7.02.04	แบบขยายทางลาด R-07
A7.02.05	แบบขยายทางลาด R-08
A7.02.06	แบบขยายทางลาด R-09
A7.02.07	แบบขยายทางลาด R-10
A7.02.08	แบบขยายทางลาด R-11, R-12
A7.02.09	แบบขยายทางลาด R-13
A7.02.10	แบบขยายบันไดหนีไฟ(TYPICAL)
A7.04.01	แบบขยายลิฟต์ E-01, E-02, E-03, E-04, E-05, E-06, E-07
A7.04.02	แบบขยายลิฟต์ E-01, E-02, E-03, E-04, E-05, E-06, E-07
A7.04.03	แบบขยายลิฟต์ E-01, E-02, E-03, E-04, E-05, E-06, E-07
A7.04.04	แบบขยายลิฟต์ E-01, E-02, E-03, E-04, E-05, E-06, E-08, E-09
A7.04.05	แบบขยายลิฟต์ E-01, E-02, E-03, E-04, E-05, E-06, E-08, E09
A7.04.06	แบบขยายรูปตัดลิฟต์
A7.04.07	แบบขยายรูปตัดลิฟต์
A7.04.08	แบบขยายรูปตัดลิฟต์

A8_แบบขยายประตูหน้าต่าง	
A8.01	ตารางรายการประตู-หน้าต่าง
A8.02	ตารางรายการประตู-หน้าต่าง
A8.03	ตารางรายการประตู-หน้าต่าง
A8.04	ตารางรายการประตู-หน้าต่าง
A8.05	ตารางรายการประตู-หน้าต่าง
A8.06	รายการชุดอุปกรณ์ประตู-หน้าต่าง
A8.07	รายการชุดอุปกรณ์ประตู-หน้าต่าง
A8.08	รายการชุดอุปกรณ์ประตู-หน้าต่าง
A8.09	รายการชุดอุปกรณ์ประตู-หน้าต่าง
A8.10	รายการชุดอุปกรณ์ประตู-หน้าต่าง
A8.11	รายการชุดอุปกรณ์ประตู-หน้าต่าง
A8.12	รายการชุดอุปกรณ์ประตู-หน้าต่าง
A8.13	รายการชุดอุปกรณ์ประตู-หน้าต่าง
A8.14	แบบขยายประตู
A8.15	แบบขยายหน้าต่าง

A9_แบบขยายทั่วไป	
A9.01	แบบขยายทั่วไป
A9.02	แบบขยายทั่วไป
A9.03	แบบขยายทั่วไป
A9.04	แบบขยายทั่วไป
A9.05	แบบขยายทั่วไป
A9.06	แบบขยายทั่วไป
A9.07	แบบขยายทั่วไป
A9.08	แบบขยายลูกศรทางเดินรถ
A9.09	แบบขยาย COLUMN GUARD, RAMP แบบขยายทั่วไป
A9.10	แบบขยายฝาดังเก็บน้ำ, แบบขยายบันไดภายนอกอาคาร
A9.11	แบบขยายที่จอดรถ, ที่จอดรถคนพิการ
A9.12	แบบขยายที่จอดรถขยะ, ที่จอดรถส่งของ
A9.13	แบบขยาย RAMP คนพิการ
A9.14	แบบขยายห้องขยะ
A9.15	แบบขยายราวกันตก
A9.16	แบบขยายทั่วไป

OWNER

LUXURY HOTEL DEVELOPMENT

SUKHUMVIT 38 CO., LTD.

DESIGNER

ARCHITECTS 49 LIMITED

81 SUKHUMVIT 26

BANGKOK 1010 THAILAND

T + 66 (0) 2260 4370

F + 66 (0) 2259 3872

E A49@A49.CO.TH

W A49.CO.TH



K.C.S. & ASSOCIATES CO.,LTD.

22ND FLOOR, CHARN ISSARA TOWER II

2592/267 NEW PETCHABURI ROAD, BANGKAPI,

HUAY KWANG, BAKOK 10310 THAILAND

T +66 (0) 2308 2481 5

F +66 (0) 2308 2485



MEC PRO DESIGN CO.,LTD.


567 BUILDING 4TH FLOOR 1X SOI 51

SUAN LUANG, BANGKOK 10250 THAILAND

T +66 (0) 2170 8029

F +66 (0) 37 034 8917

E MECPRO.DESIGN@GMAIL.COM

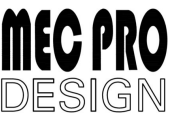

P.LANDSCAPE CO.,LTD.

59/3 SUKHUMVIT 39, KLONGTON NUA,

WATTANA, BANGKOK 10110 THAILAND

T (622) 261 3700 TO 9

F (622) 238 3388

E INFO@PLANDSCAPE.COM

W WWW.PLANDSCAPE.COM



ARCHITECTS	SIGNED
พิธีชัย วงศ์โศภวรรณ	วสท.509
ณรงค์ชัย อธิวิจิตร	วสท.720
จารุวิมล อธิวิจิตร	วสท.769
พิณนพร อธิวิจิตร	สทต.3432
สุชภา ศรีสมบูรณ์	สทต.3347
ปวิศต์ หิเนนโนโย	วสท.20910
ศสพร ศิริพจน์	วสท.23830
วันธรณ์ พูลสวัสดิ์	วสท.27171

STRUCTURAL ENGINEER	SIGNED
กาญจนา จันทวงศ์	วช.1023
กุลศิริ จันทวงศ์	สช.9572
ภาณุ สายรวมญาติ	สช.15169
อภิสิทธิ์ สมอียง	วช.69140

ELECTRICAL ENGINEER	SIGNED
ชานน นิ่มสาร	พท.1118
ทนศักดิ์ พิธีสุข	สท.1586
ธนวัฒน์ น้อยจ้อย	พท.63548

MECHANICAL ENGINEER	SIGNED
เบนศ ไชยพงษ์	สท.3566
ณัทพร วิเชียรเพทยาคม	วท.51088
วิฑรศักดิ์ บุญโคตร	วท.52030

ENVIRONMENTAL ENGINEER	SIGNED
ทรงวุฒิ วิเศษศิลป์	สท.625
เบนศ ไชยพงษ์	วท.112
วสุ ละเอียด	วท.7507

SANITARY ENGINEER	SIGNED
ธีร นามสกุล	สท.6094

LANDSCAPE ARCHITECT	SIGNED
นัทธ วรรณวิจิตร	วท.108

GENERAL NOTE

- THIS DRAWING IS THE PROPERTY OF ARCHITECTS 49 LIMITED OR ONE OF ITS AFFILIATES. IT IS ISSUED SUBJECT TO RETURN UPON DEMAND AND IS NOT TO BE USED EXCEPT IN CONNECTION WITH THE PROJECT FOR WHICH IT IS INTENDED.
- DO NOT SCALE THIS DRAWING. USE FIGURED DIMENSIONS ONLY.

ให้ใช้ตัวเลขที่กำหนดไว้เท่านั้น ห้ามวัดจากแบบ

PROJECT NAME

THE OKURA PRESTIGE

SUKHUMVIT BANGKOK HOTEL

AND SPA

DRAWING TITLE

สารบัญแบบ

ISSUE/REVISION

NO	DESCRIPTION	BY	DATE
1	แบบขยายทาง	A49	17/04/2569

CHECK BY DRAWING NO.


ARCHITECT	SIGNED
PD	
PA	
JC	

A0.01

DRAWN BY Author

PRINTED DATE 17/04/2569

SCALE: REF. FILE

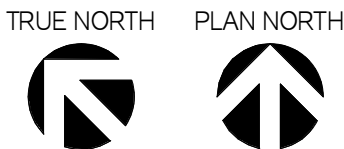

OWNER
LUXURY HOTEL DEVELOPMENT
SUKHUMVIT 38 CO., LTD.

DESIGNER
ARCHITECTS 49 LIMITED
81 SUKHUMVIT 26
BANGKOK 10110 THAILAND
T + 66 (0) 2260 4370
F + 66 (0) 2259 3872
E A49@A49.CO.TH
W A49.CO.TH

K.C.S. & ASSOCIATES CO., LTD.
22ND FLOOR, CHARN ISSARA TOWER II
2592/267 NEW PETCHABURI ROAD, BANGKAPI,
HUAY KWANG, BAKOK 10310 THAILAND
T +66 (0) 2308 2481 5
F +66 (0) 2308 2485

MEC PRO DESIGN CO., LTD.
567 BUILDING 4TH FLOOR, SUKUMVIT 38
SUAN LUANG, BANGKOK 10250 THAILAND
T +66 (0) 2170 8029
+66 (0) 97 094 8917
E MECPRO.DESIGN@GMAIL.COM

P LANDSCAPE CO., LTD.
59/3 SUKHUMVIT 39, KLONGTON NUA,
WATTANA, BANGKOK 10110 THAILAND
T (622) 261 3700 TO 9
F (622) 238 5588
E INFO@PLANDSCAPE.COM
W WWW.PLANDSCAPE.COM

ARCHITECTS				SIGNED
พิธีชัย	วงศ์ไวยวรรณ	วสท.509		
ณเรศวิทย์	อริวิตร	วสท.720		
จารุวัฒน์	อริวิตร	วสท.769		
พิณนพร	อริวิตร	วสท.3432		
สุชภา	ศรีสมบุญ	วสท.3347		
ปาริชาติ	ดิเรกนันท	วสท.20910		
ศสพร	ศิริพงษ์	วสท.23830		
วรินทร์	พลสวัสดิ์	วสท.27171		

STRUCTURAL ENGINEER				SIGNED
กาญจนา	จันทราวุธ	วสท.1023		
กุลสิริ	จันทราวุธ	วสท.9572		
ภาสกร	สายวณภูมิ	วสท.15169		
อภิสิทธิ์	สมชาย	วสท.69140		

ELECTRICAL ENGINEER				SIGNED
ชานน	นิมิต	วสท.1118		
พนมศักดิ์	พิรุณ	วสท.1586		
ธนวัฒน์	น้อยจ้อย	วสท.63548		

MECHANICAL ENGINEER				SIGNED
เบน	ไชยพงษ์	วสท.3566		
ณภัทร	วิเชษฐพญาคม	วสท.51086		
วิฑูรย์	บุญวิเศษ	วสท.52030		

ENVIRONMENTAL ENGINEER				SIGNED
ทรงวุฒิ	วิเศษศิลป์	วสท.625		
เบน	ไชยพงษ์	วสท.112		
วสุ	ละลาชัย	วสท.7507		

SANITARY ENGINEER				SIGNED
ช่อ	นามสกุล	เลขใบอนุญาต		

LANDSCAPE ARCHITECT				SIGNED
นัท	รณศิริ	วสท.108		

GENERAL NOTE
1. THIS DRAWING IS THE PROPERTY OF ARCHITECTS 49 LIMITED OR ONE OF ITS AFFILIATES. IT IS ISSUED SUBJECT TO RETURN UPON DEMAND AND IS NOT TO BE USED EXCEPT IN CONNECTION WITH THE PROJECT FOR WHICH IT IS INTENDED.
2. DO NOT SCALE THIS DRAWING. USE FIGURED DIMENSIONS ONLY.
ให้ใช้ค่าเลขที่กำกับไว้เท่านั้น ห้ามวัดจากแบบ

PROJECT NAME
THE OKURA PRESTIGE
SUKHUMVIT BANGKOK HOTEL
AND SPA

DRAWING TITLE
แผนที่สังเขป,ผังโฉนดที่ดิน

ISSUE/REVISION			
NO	DESCRIPTION	BY	DATE
1	แบบแปลนอาคาร	A49	17/04/2569















CHECK BY
ARCHITECT
PD
PA
JC

DRAWING NO.
A0.02

DRAWN BY
PRINTED DATE
17/04/2569

SCALE:
REF. FILE
1 : 250

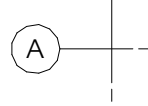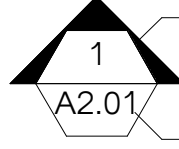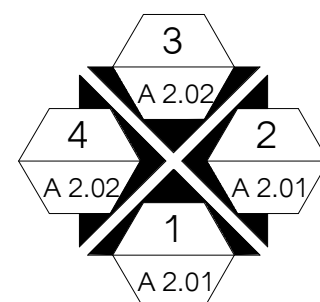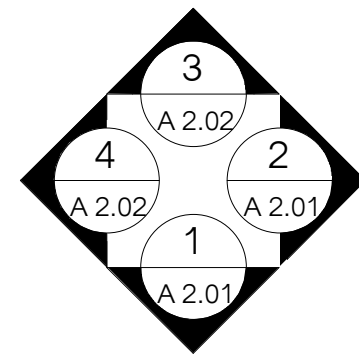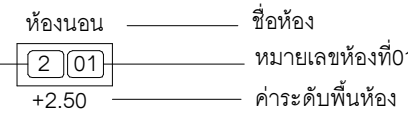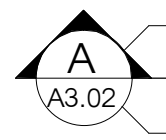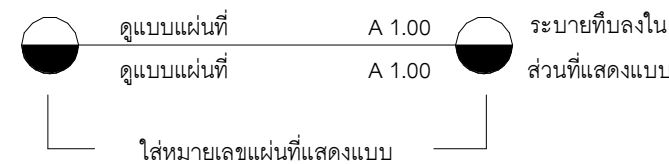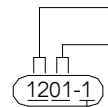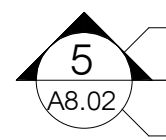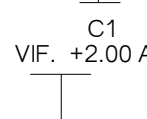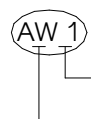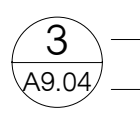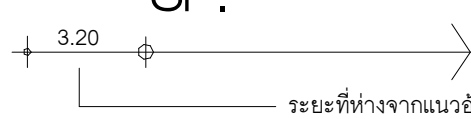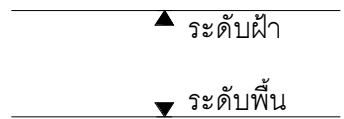

สัญลักษณ์มาตรฐาน			
สัญลักษณ์เส้นเสา 	สัญลักษณ์รูปด้านอาคาร  — ลำดับรูปด้านตามตัวเลข — หมายเลขแผนที่แสดงรูปด้าน	สัญลักษณ์รูปด้านภายนอก 	สัญลักษณ์แสดงรูปด้านภายใน  (แสดงทิศทางการมองรูปด้านแบบแปลน) (แสดงแบบแปลน)
สัญลักษณ์เลขห้อง  — ห้องเลขที่ 02 — ชื่อห้อง — หมายเลขห้องที่ 01 — ค่าระดับพื้นห้อง	สัญลักษณ์รูปตัดอาคาร  — ลำดับรูปตัดตามตัวเลข — หมายเลขแผนที่แสดงรูปตัด	MATCH LINE  — ดูแบบแผนที่ — ระบายที่บ่งบอกส่วนที่แสดงแบบ — ใส่หมายเลขแผนที่แสดงแบบ	
สัญลักษณ์ประตู  — หมายเลขอื่นอาคาร — หมายเลขห้อง — หมายเลขลำดับประตูในห้อง	สัญลักษณ์รูปตัดขยาย  — ลำดับรูปตัดขยายตามตัวเลข — หมายเลขแผนที่แสดงรูปตัด	สัญลักษณ์แสดงทิศเหนือ 	
สัญลักษณ์ฝ้าเพดาน  — ชนิดฝ้าเพดาน — อ้างอิงที่ ABOVE FLOOR FINISH — ระดับความสูงของฝ้าเพดาน	สัญลักษณ์ตัดผนังภายนอก  — ลำดับรูปตัดขยายตามตัวเลข — หมายเลขแผนที่แสดงรูปตัด (แสดงแนวตัด WALL SECTION)	สัญลักษณ์จุดอ้างอิง (BENCHMARK) 	
สัญลักษณ์หน้าต่าง  — หมายเลขแบบหน้าต่าง — วัสดุของหน้าต่าง	สัญลักษณ์แบบขยาย  — ลำดับแบบขยาย ตามตัวเลข — หมายเลขแผนที่แสดงแบบขยาย	สัญลักษณ์จุดเริ่มต้น  — STARTING POINT — ระยะที่ห่างจากแนวอ้างอิง	
สัญลักษณ์วัสดุผนังภายนอก  — หมายเลขผิววัสดุผนังภายนอก (กำหนดตามตารางวัสดุ / แสดงในรูปด้าน)	สัญลักษณ์แสดงระดับ  — ระดับฝ้า — ระดับพื้น	สัญลักษณ์ทั่วไป  — ประเภทและลักษณะผนังภายใน (กำหนดตามตาราง WALL TYPE / แสดงในแบบแปลน)	
สัญลักษณ์วัสดุ ผนังภายใน  — ประเภทและลักษณะผนังภายใน (กำหนดตามตาราง WALL TYPE / แสดงในแบบแปลน)	สัญลักษณ์แก้ไขแบบ  — กรอบแสดงบริเวณที่แก้ไข — ลำดับการแก้ไข	แสดงทิศทางเดินรถ  — ประเภทและลักษณะผนังภายใน (กำหนดตามตาราง WALL TYPE / แสดงในแบบแปลน)	

สัญลักษณ์วัสดุแบบสถาปัตยกรรม

	ดินเดิม		หินดิบ (รูปตัด)
	ดินถม		หินอ่อน หินแกรนิต (รูปตัด)
	ทวาช ปูนทราย ปูนประระดับ		หินอ่อน หินแกรนิต (รูปตัดขยาย)
	กรวดหินคลุก		หินบุฉาบ (รูปด้าน)
	คอนกรีต		พรม (รูปตัด)
	ผนัง ค.ส.ล. สำเร็จรูป		หินทราย (รูปตัด)
	อิฐมอดู (แปลน รูปตัด แบบขยาย)	สัญลักษณ์ของลายเส้น	
	คอนกรีตลึบ (แปลน รูปตัด แบบขยาย)		
	อิฐยี่สิบเอ็ด (รูปตัด แบบขยาย)		
	ไม้ขัด		
	ไม้ทึบแสงผิว		
	โครงไม้ ไม้ทึบไม้แต่งผิว		แสดงเส้นวงตัวไป
	เหล็ก		เส้นแสดงผนังค.ส.ล.
	โลหะทึบไข่เหล็ก		เส้นแสดงสิ่งก่อสร้างเหนือระดับพื้น
	กระจก (รูปตัด แบบขยาย)		เส้นแสดงฐานถ้ำล่าง
	กระจก (รูปตัด)		เส้นแสดงแนวระดับดิน
	น็อตแก้ว		เส้นแสดงสิ่งก่อสร้างหรืออุปกรณ์ที่ไปรวมในสัญลักษณ์
	ฉนวนที่มีลักษณะอ่อน (รูปตัด แบบขยาย)		เส้นแสดงขอบเขตของการก่อสร้าง
	ฉนวนที่มีลักษณะแข็ง (รูปตัด แบบขยาย)		เส้นแสดงแนวคัต
	วัสดุอุดรอยต่อ		เส้นแสดงระยะ (หน่วยเป็นมิลลิเมตร)
	วัสดุทน ผนวกกับไฟ	การบอกระดับ	
	กระเบื้อง (รูปตัด แบบขยาย)		

มาตรฐานคำย่อภาษาอังกฤษ

&	AND	D		H		N		S. SK.	SERVICE SINK
<	ANGLE	DET.	DETAIL	H.	HIGH	N.	NORTH	STD.	STANDARD
@	AT	DIA.	DIAMETER	H.B.	HOSE BIB	N.I.C.	NOT IN CONTRACT	STL.	STEEL
CL	CENTER LINE	DIM.	DIMENSION	H.C.	HOLLOW CORE	NO.	NUMBER	STOR.	STORAGE
#	NUMBER	DN.	DOWN	HCP.	HANDICAPPED	NOM.	NORMAL	STRUCT.	STRUCTURAL
Ø	DIAMETER	D.O.	DOOR OPENING	HDWR.	HARDWARE	N.S.	NO SCALE	SUSP.	SUSPENDED
A		DS.	DOWNSPOUT	HDWD.	HARDWOOD	N.T.S.	NOT TO SCALE	SYMM.	SYMMETRICAL
A/C	AIR CONDITIONED	DWG.	DRAWING	H.M.	HOLLOW METAL			SYS.	SYSTEM
ADJ.	ADJUSTABLE			HORIZ.	HORIZONTAL	O			
AFF.	ABOVE FINISH FLOOR	E		HR.	HOUR	O.A.	OVERALL	T	
ALT.	ALTERNATE	E.	EAST	HT.	HEIGHT	O.C.	ON CENTER	T.	TREAD
ALUM.	ALUMINIUM	EA.	EACH	HVAC.	HEATING, VENTILATION	O.D.	OUTSIDE DIAMETER	T.B.	TOWEL BAR
ANOD.	ANODIZED	E.J.	EXPANSION JOINT		AND AIR CONDITIONING	OFD.	OVERFLOW DRAIN	T&G	TOUNGE AND GROOVE
A.P.	ACCESS PANEL	EL.	ELEVATION	H.W.	HOT WATER	OVHD.	OVERHEAD	TEL.	TELEPHONE
APPROX.	APPROXIMATE	ELEC.	ELECTRICAL			OPNG.	OPENING	TEMPER.	TEMPERED
ARCH.	ARCHITECTURAL	ELEV.	ELEVATION	I		OPP.	OPPOSITE	THK.	THICK
ASPH.	ASPHALT	EMER.	EMERGENCY	I.D.	INSIDE DIAMETER			T.O.C.	TOP OF CURB
		E.O.S.	EDGE OF SLAB	INCL.	INCLUDING	P		TOIL.	TOILET
B		EQ.	EQUAL	INSUL.	INSULATION	PL.	PLATE	TOP	TOP OF PAVEMENT
BL.	BUILDING LINE	EXP.	EXPANSION	INT.	INTERIOR	P.L.	PROPERTY LINE	TOW	TOP OD WALL
BD.	BOARD	EXPO.	EXPOSED			PLBG.	PLUMBING	T.P.D.	TOILET PAPER DISPENCES
BITUM.	BITUMINOUS	EXT.	EXTERIOR	J		PLAS.	PLASTER	T.V.	TELEVISION
BLDG.	BUILDING	EXCL.	EXCLUDE	JAN.	JANITOR	PLYWD.	PLYWOOD	TYP.	TYPICAL
BM.	BENCHMARK			JST.	JOIST	PCC	PRECASE CONCRETE		
BOT.	BOTTOM	F		JT.	JOINT	PT	PAINT	U	
BOC.	BOTTOM OF CURB	F.A.	FIRE ALARM			P.T.D.	PAPER TOWEL DISPENSER	UNF.	UNFURNISHED
BSMT.	BASEMENT	F.D.	FLOOR DRAIN	K		PTN.	PARTITION	UNF.	UNLESS NOTED
B.U.R.	BUILT UP ROOFING	FDN.	FOUNDATION	KIT.	KITCHEN				OTHERWISE
		F.E.	FIRE EXTINGUISHER			R		UR.	URINAL
		F.E.C.	FIRE EXTINGUISHER	L		R.	RADIUS		
C				LAM.	LAMINATE	R.D.	ROOF DRAIN	V	
CAB	CABINET	F.F.L.	FLOOR FINISH LEVEL	LAV.	LAVATORY	REF.	REFERENCE	VERT.	VERTICAL
CARP.	CARPET	F.H.C	FIRE HOSE CABINET	L.F.	LINEAR FOOT	REINF.	REINFORCED	VOL.	VOLUME
C.B.	CATCH BASIN	FIN.	FINISH	L.H.	LEFT HAND	REV.	REVISED		
CEM.	CEMENT	FLR.	FLOOR	LKH.	LOCKER	RFG.	ROOFING	W	
CER.	CAST IRON	FR.	FRAME	LVR.	LOUVER	R.H.	RIGHT HAND	W.	WEST
CLG.	CEILING	FST.	FIRW STAIR			RS.	ROLLING SHUTTER	W	WITH
CLO.	CLOSET	FT.	FOOT, FEET	M		RL.	REINFORCED CONCRETE	W.H.	WATER HEATER
CLR.	CLEAR	FURR.	FURRING, FURRED	MATL.	MATERIAL		STRUCTURE LEVEL	W/O	WITH OUT
C.M.U.	CONCRETE MASONRY UNIT	FUT.	FUTURE	MAX.	MAXIMUM	S		W.C.	WATER CLOSET
COL.	COLUMN			M.B.	MECHANICAL BOLT			WD.	WOOD
CONC.	CONCRETE	G		MECH.	MECHANICAL	S.	SOUTH	WP.	WATERPROOF
COND.	CONDENSER	GALV.	GALVANIZE	MEMB.	MEMBRANE	SHED.	SCHEDULE	WPM.	WATERPROOF MEMBRANE
CONST.	CONSTRUCTION	G.B.	GRAB BAR	MET.	METAL	SECT.	SECTION	WT.	WEIGHT
CONT.	CONTINUOUS	G.I.	GALVANIZED IRON	MFR.	MANUFACTURER	SHR.	SHOWER		
CTR.	CENTER	GL.	GLASS, GLAZING	MH.	MANHOLE	SHT.	SHEET		
CTSK.	COUNTERSINK	GND.	GROUND	MIN.	MINIMUM	SIM.	SIMILAR		
C.W.	COLD WATER	GYP.	GYPSUM	MIR.	MORROR	SP.	STARTING POINT		
				MISC.	MISCELLANEOUS	SPEC.	SPECIFICATION		
				M.O.	MASONRY OPENING	SQ.	SQUARE		
				MULL.	MULLION	S.S.	STAINLESS STEEL		

หลักเกณฑ์ในการก่อสร้างอาคารและสาธารณูปโภค

[illegible]**OWNER**

**LUXURY HOTEL DEVELOPMENT
SUKHUMVIT 38 CO., LTD.**



K.C.S. & ASSOCIATES CO., LTD.
22ND FLOOR, CHARN ISSARA TOWER II
2922/267 NEW PETCHABURI ROAD, BANGKAPI,
HUAY KWANG, BAKOK 10310 THAILAND
T +66 (0) 2308 2481 5
F +66 (0) 2308 2485

MEC PRO DESIGN CO.,LTD.
567 BUILDING 4TH FLOOR 4TH FLOOR 4TH FLOOR
SUAN LUANG, BANGKOK 10250 THAILAND
T +66 (0) 2170 8029
+66 (0) 97 094 8917
E MECPRO.DESIGN@GMAIL.COM

P LANDSCAPE CO.,LTD.
59/3 SUKHUMVIT 39, KLONGTON NUA,
WATTANA, BANGKOK 10110 THAILAND
T (622) 261 3700 TO 9
F (622) 258 3588
E INFO@PLANDSCAPE.COM
W WWW.PLANDSCAPE.COM

ARCHITECTS

พิชัย	วงศ์ไทยวรรณ	วสท.509
เนตรงศวิชัย	อริยมิตร	วสท.720
จารุวอลลภ	อวันเกียรติศักดิ์	วสท.769
ทิมมพร	อิรพวงศักดิ์	สสท.3432
อุษุภา	ศรีสมบุญรัตน์	สสท.3347
ปาริชาติ	หินหมื่นไวย	ภสท.20910
ดลพร	ศิริพจน์	ภสท.23830
วันวิษุณี	พลสวัสดิ์	ภสท.27171

STRUCTURAL ENGINEER

การุญ	จันทรวงศ์	วย.1023	
กุลสิริ	จันทรวงศ์	สย.9572	
ภาสุ	สายรวมญาติ	สย.15169	
อภิสิทธิ์	สมอ้าง	ภย.69140	

ELECTRICAL ENGINEER

อาคม	นิมิตตรง	วพค.1116
ทองศักดิ์	ฟ้ารุ่งแสง	สพค.1586
ธนวัฒน์	น้อยจ้อย	ภพค.63548

MECHANICAL ENGINEER

ชเนต	ไชยพงษ์	สท.3566
ณภัทร	วิเชียรแพทยาคม	ภท.51086
รักพงศ์	บุญวิเศษ	ภท.52030

ENVIRONMENTAL ENGINEER

ทรงวุฒิ	วิเศษศิลป์	สส.625
ธเนศ	ไชยพงษ์	ภส.112
วสุ	ละลายบาป	ภส.7507

SANITARY ENGINEER

ชื่อ นามสกุล เลขใบอนุญาต

LANDSCAPE ARCHITECT

หน้าที่ยื่น รจนาศรีไพโรจน์ สกส.108 *แก้ไข*

GENERAL NOTE

1. THIS DRAWING IS THE PROPERTY OF ARCHITECTS 49 LIMITED OR ONE OF ITS AFFILIATES. IT IS ISSUED SUBJECT TO RETURN UPON DEMAND AND IS NOT TO BE USED EXCEPT IN CONNECTION WITH THE PROJECT FOR WHICH IT IS INTENDED.
2. DO NOT SCALE THIS DRAWING. USE FIGURED DIMENSIONS ONLY.
ให้ใช้ค่าตัวเลขที่กำหนดไว้เท่านั้น ห้ามวัดจากแบบ

PROJECT NAME

**THE OKURA PRESTIGE
SUKHUMVIT BANGKOK HOTEL
AND SPA**

DRAWING TITLE

สัญลักษณ์มาตรฐาน, มาตรฐานคำย่อ,
กำหนดหลักเกณฑ์ในการก่อสร้าง

ISSUE/REVISION

NO	DESCRIPTION	BY	DATE
1	แบบประกาศราคา	A49	17/04/2569

CHECK BY

ARCHITECT SIGNED


PM

PD

PA _____


JC _____

DRAWN BY **Author** SCALE: **1:1**
PRINTED DATE **17/04/2569** REF. FILE

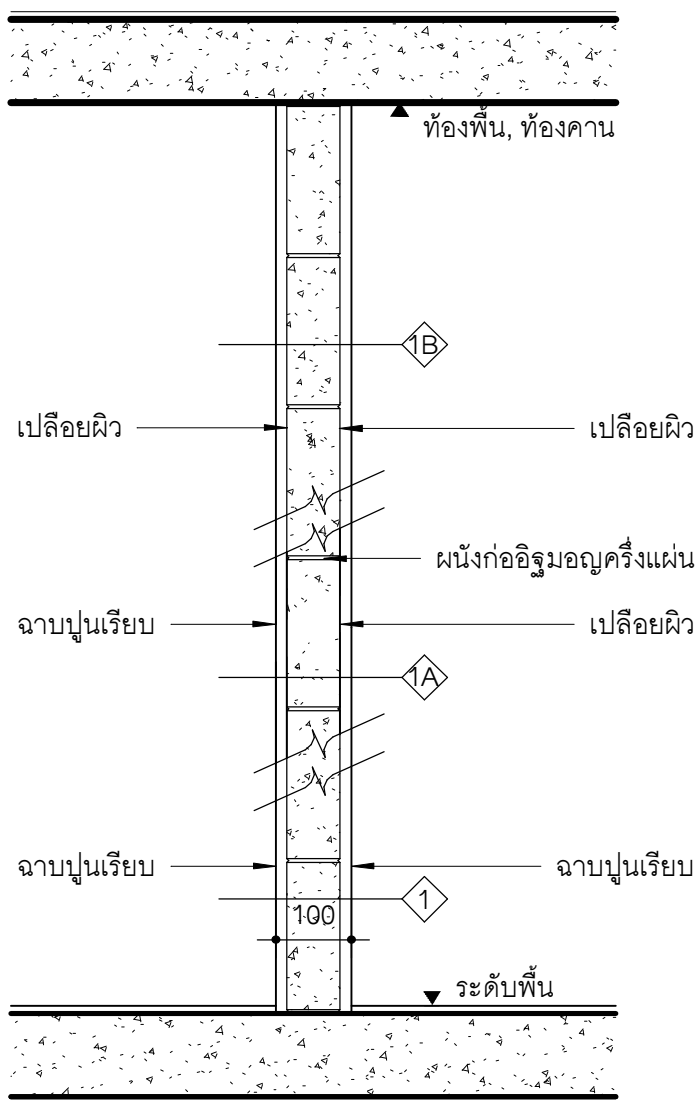


ผนังแบบที่ 1 ผนังคอนกรีตบล็อกเชิงตัน ทหนา 100 มม.

- 1 ผนังคอนกรีตบล็อกเชิงตัน ทหนา 100 มม. ฉาบปูนเรียบ 2 ด้าน
- 1A ผนังคอนกรีตบล็อกเชิงตัน ทหนา 100 มม. ฉาบปูนเรียบ 1 ด้าน
- 1B ผนังคอนกรีตบล็อกเชิงตัน ทหนา 100 มม. เปลือยผิว

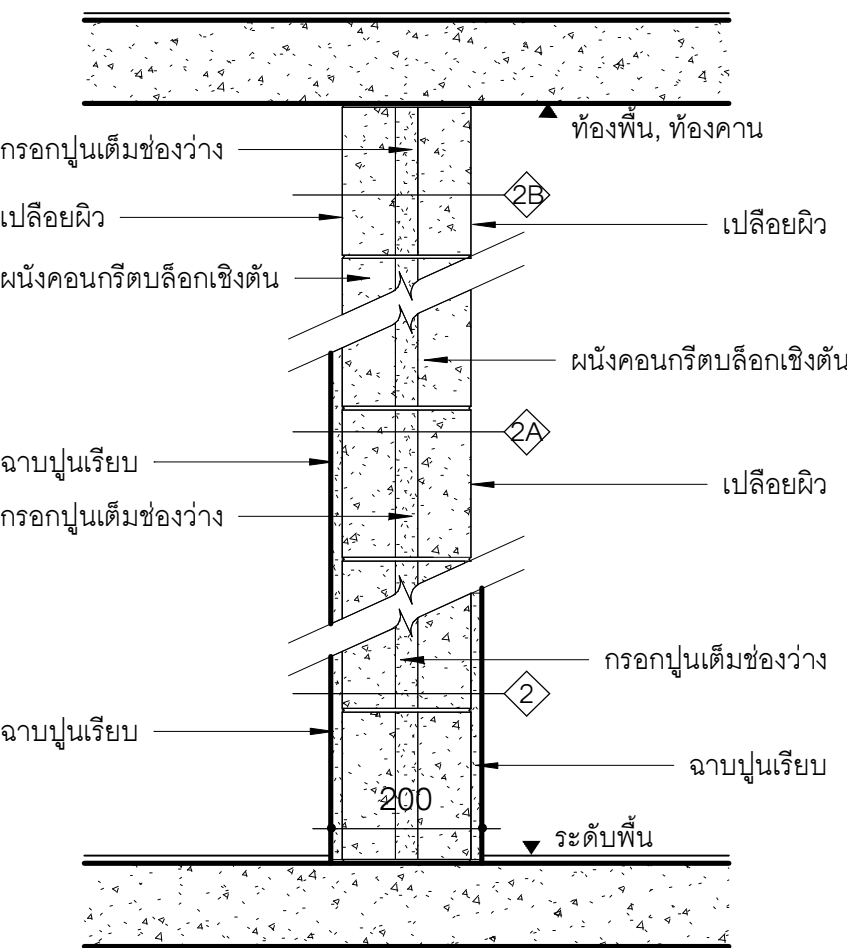


ผนังแบบที่ 2 ผนังคอนกรีตบล็อกเชิงตัน ทหนา 200 มม.

- 2 ผนังคอนกรีตบล็อกเชิงตัน 2 ชั้น ทหนา 200 มม. ฉาบปูนเรียบ 2 ด้าน
- 2A ผนังคอนกรีตบล็อกเชิงตัน 2 ชั้น ทหนา 200 มม. ฉาบปูนเรียบ 1 ด้าน
- 2B ผนังคอนกรีตบล็อกเชิงตัน 2 ชั้น ทหนา 200 มม. เปลือยผิว

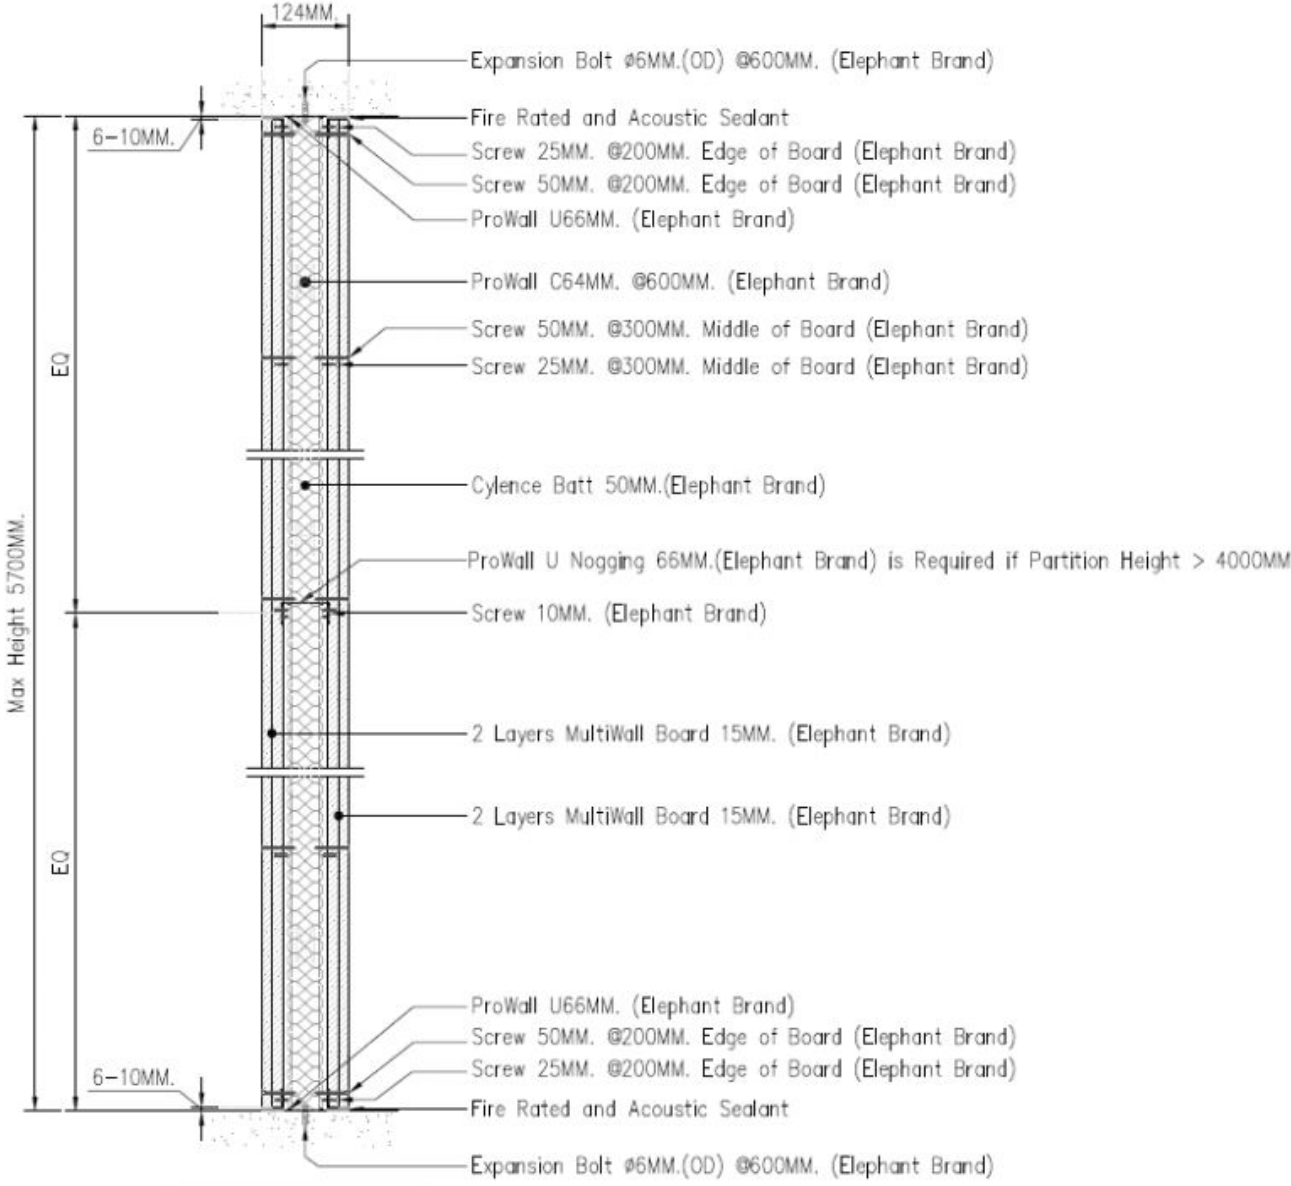


ผนังแบบที่ 4 ผนังกันเสียง STC ทหนา 125 มม.


- 4 ผนังกันเสียง STC ทหนา 125 มม. กรุแผ่นกันเสียง 2 ด้าน

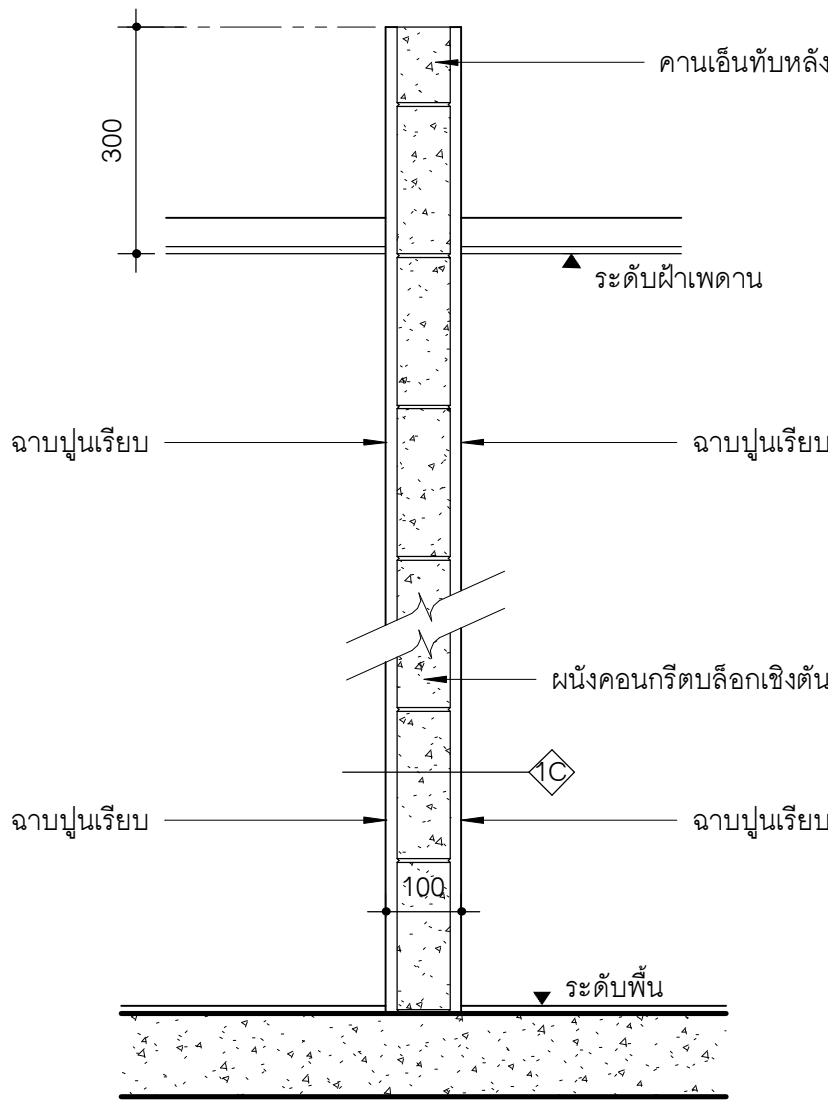

- 5 ผนังคอนกรีตบล็อกเชิงตัน ทหนา 200 มม. ฉาบปูนเรียบ 2 ด้าน สูงกว่าระดับฝ้าเพดาน 300 มม.

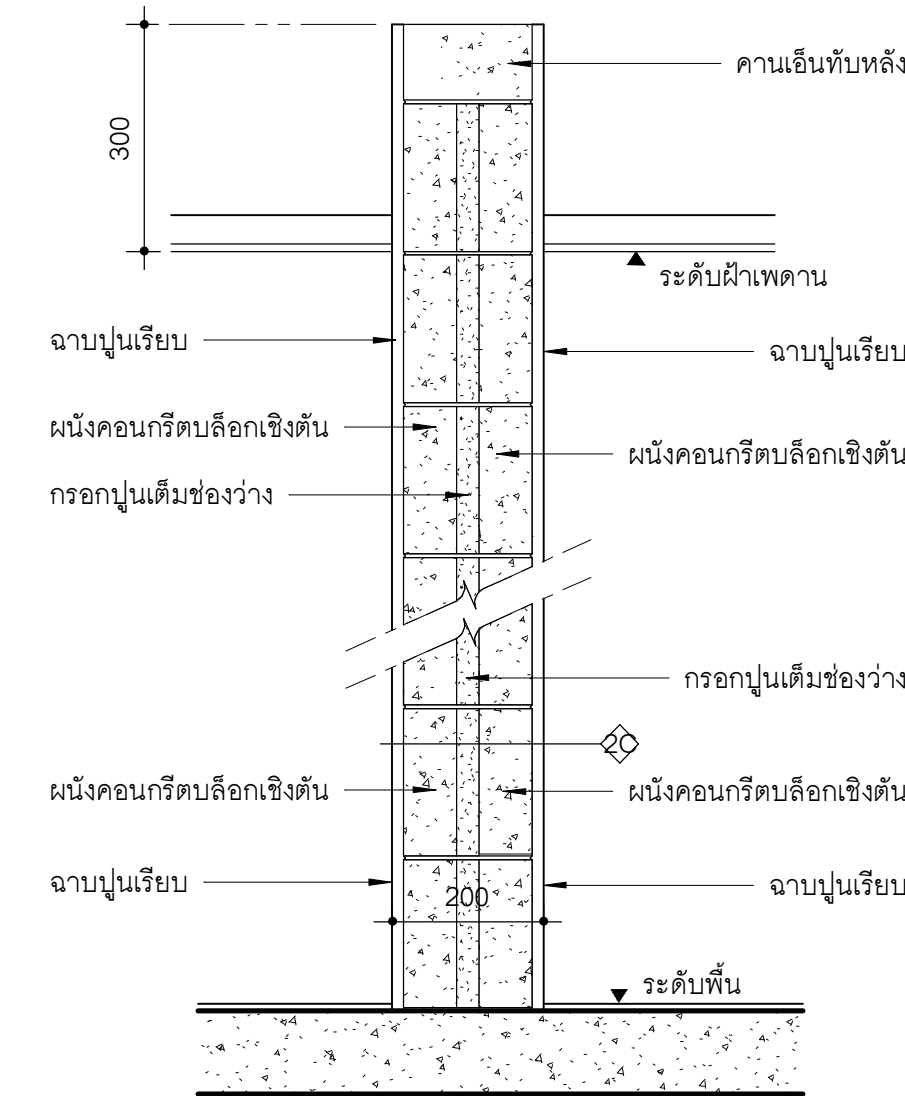


- 6 ผนังคอนกรีตบล็อกเชิงตัน 2 ชั้น ทหนา 200 มม. ฉาบปูนเรียบ 2 ด้าน สูงกว่าระดับฝ้าเพดาน 300 มม.

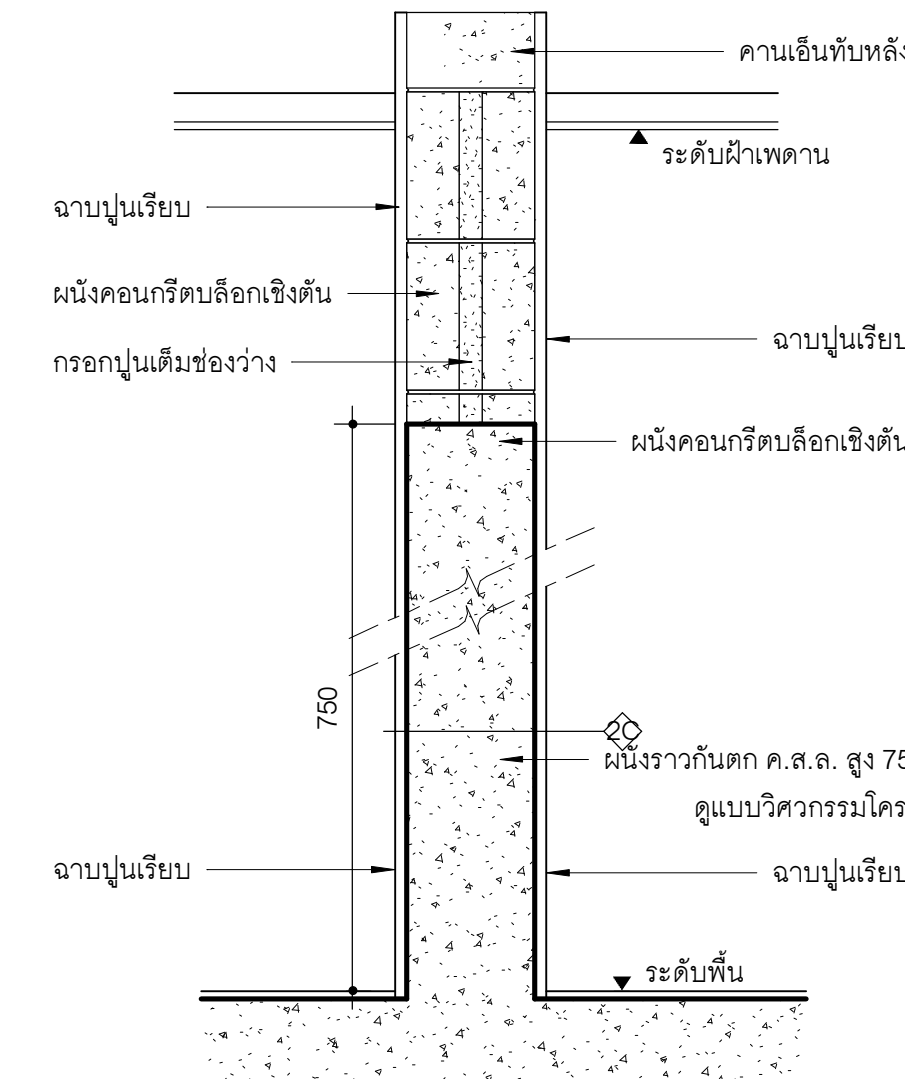


- 7 ผนังคอนกรีตบล็อกเชิงตัน 2 ชั้น ทหนา 200 มม. ฉาบปูนเรียบ 2 ด้าน สูงกว่าระดับฝ้าเพดาน 300 มม.

ผนังแบบที่ 5 ผนังคอนกรีตฉาบเรียบ ทหนา 200 มม.

- 8 ผนังกันเสียง STC ทหนา 125 มม. กรุแผ่นกันเสียง 2 ด้าน

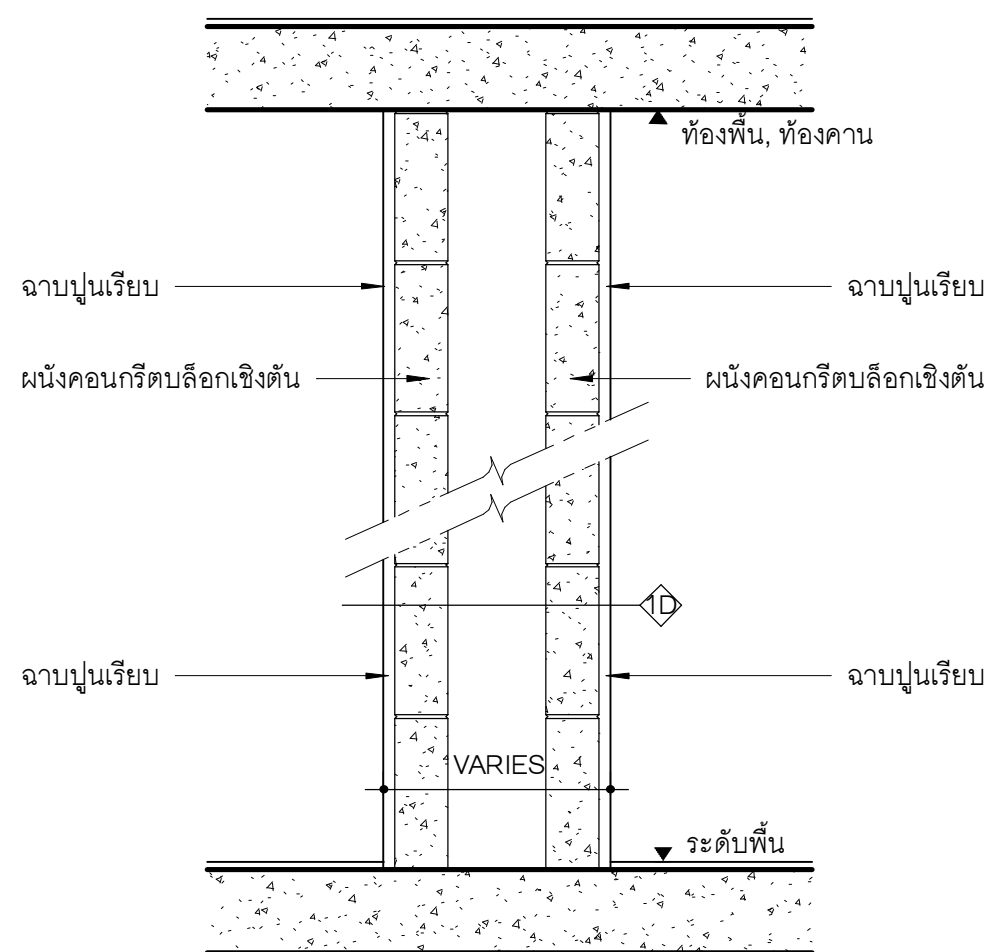

- 8 ผนังคอนกรีตบล็อกเชิงตัน 2 ชั้น ฉาบปูนเรียบ 2 ด้าน ระยะความกว้างผนังตามแบบ

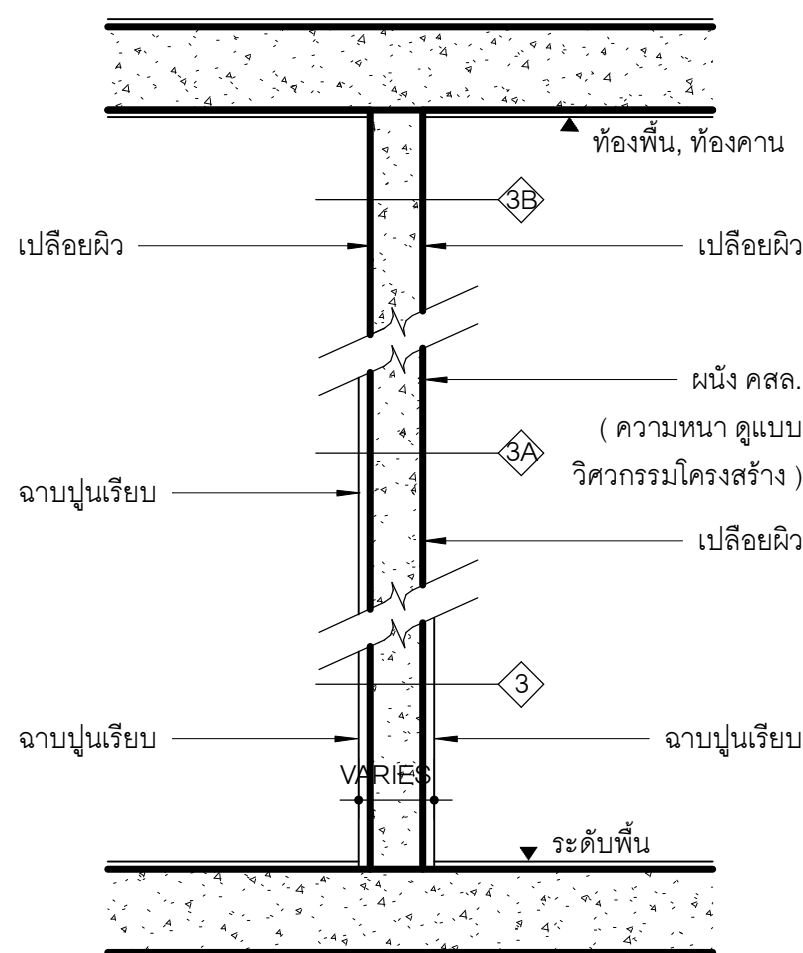

ผนังแบบที่ 3 ผนังคอนกรีตเสริมเหล็ก

- 3 ผนังคอนกรีตเสริมเหล็ก ฉาบปูน 2 ด้าน
- 3A ผนังคอนกรีตเสริมเหล็ก ฉาบปูน 1 ด้าน
- 3B ผนังคอนกรีตเสริมเหล็ก เปลือยผิว

OWNER
LUXURY HOTEL DEVELOPMENT
SUKHUMVIT 38 CO., LTD.

DESIGNER
ARCHITECTS 49 LIMITED
81 SUKHUMVIT 26
BANGKOK 10110 THAILAND
T + 66 (0) 2260 4370
F + 66 (0) 2259 3872
E A49@A49.CO.TH
W A49.CO.TH

K.C.S. & ASSOCIATES CO. LTD.
22ND FLOOR, CHARN ISSARA TOWER II
2522/267 NEW PETCHABURI ROAD, BANGKAPI,
HUAY KWANG, BAKOK 10310 THAILAND
T +66 (0) 2308 2481 5
F +66 (0) 2308 2485

MEC PRO DESIGN CO. LTD.
567 BUILDING 4TH FLOOR, SUKUMVIT 38
SUAN LUANG, BANGKOK 10250 THAILAND
T +66 (0) 2170 8029
F +66 (0) 37 034 8917
E MECPRO.DESIGN@GMAIL.COM

P LANDSCAPE CO. LTD.
55/3 SUKHUMVIT 39, KLONGTON NUA,
WATTANA, BANGKOK 10110 THAILAND
T (622) 261 3700 TO 9
F (622) 238 3388
E INFO@PLANDSCAPE.COM
W WWW.PLANDSCAPE.COM

ARCHITECTS				SIGNED
พิธีชัย	วงศ์ไวศยวรรณ	วสท.509		
ณรงค์ชัย	อริยมิตร	วสท.720		
จารุวัฒน์	อริยมิตร	วสท.769		
พิณพร	อริยมิตร	สท.3432		
สุชาภา	ศรีสมบุญ	สท.3347		
ปวิศร์	พิณนัย	วสท.20910		
ศสพร	ศิริพจน์	วสท.23830		
วันธรณ์	พลสวัสดิ์	วสท.27171		

STRUCTURAL ENGINEER				SIGNED
กาญจนา	จันทวงศ	วสท.1023		
กุลสิทธิ์	จันทวงศ	สท.9572		
ภาณุ	สายวณภูมิ	สท.15169		
อภิสิทธิ์	สมอียง	วสท.69140		

ELECTRICAL ENGINEER				SIGNED
ชานน	นิมิต	วสท.1118		
พนมศักดิ์	พิรุณ	สท.1188		
ธนวัฒน์	น้อยจ้อย	วสท.63548		

MECHANICAL ENGINEER				SIGNED
เบน	ไชยพงษ์	สท.3566		
ณัทพร	วิเชียรพทยาคม	วสท.51088		
วิภากร	บุญนิยม	วสท.52030		

ENVIRONMENTAL ENGINEER				SIGNED
ทรงวุฒิ	วิเศษศิลป์	สท.625		
เบน	ไชยพงษ์	วสท.112		
วสุ	ละลาบาย	วสท.7507		

SANITARY ENGINEER				SIGNED
ชื่อ	นามสกุล	เลขใบอนุญาต		

LANDSCAPE ARCHITECT				SIGNED
นัท	รณศิริ	วสท.108		

GENERAL NOTE

- THIS DRAWING IS THE PROPERTY OF ARCHITECTS 49 LIMITED OR ONE OF ITS AFFILIATES. IT IS ISSUED SUBJECT TO RETURN UPON DEMAND AND IS NOT TO BE USED EXCEPT IN CONNECTION WITH THE PROJECT FOR WHICH IT IS INTENDED.
- DO NOT SCALE THIS DRAWING. USE FIGURED DIMENSIONS ONLY.

ไม่ใช้ตัวเลขวัดที่กำหนดไว้ทำขึ้น ห้ามวัดจากแบบ

PROJECT NAME
THE OKURA PRESTIGE
SUKHUMVIT BANGKOK HOTEL
AND SPA

DRAWING TITLE
แบบผนัง (WALL TYPE)

ISSUE/REVISION			
NO	DESCRIPTION	BY	DATE
1	แบบผนังอาคาร	A49	17/04/2569

CHECK BY
ARCHITECT SIGNED

PH
PD
PA
JC

DRAWN BY Author
PRINTED DATE 17/04/2569
SCALE: 1:10
REF. FILE

A0.05

หมายเลข ห้อง	ชื่อห้อง	ผิวสำเร็จ			บัว เชิง ผนัง	หมายเหตุ
		พื้น	ผนัง	เพดาน		
ระดับชั้น B2						
B201	รักษาความปลอดภัย/วิศวกรรม (FIX)	F2.2	P3	C1.2	B1	
B202	โถงลิฟต์ดับเพลิง	F4.2	P3	C2.1	B4	
B203	บันไดหนีไฟ ST-01	F2.2	P2.1	C1.2	B2	
B204	บันไดหนีไฟ ST-02	F2.2	P2.1	C1.2	B2	
B205	หัวหน้าวิศวกรรม	F8	P3	C1.2	-	
B206	เลขานุการ	F8	P3	C1.2	-	
B207	เลขานุการ	F8	P3	C1.2	-	
B208	ห้องเครื่องปั้ม	F2.2	P3	C1.2	B1	
B209	ห้องเครื่องปั้ม	F2.2	P3	C1.2	B1	
B210	ปอลิฟต์	F1	P1	C1.1	-	
B211	ปอลิฟต์	F1	P1	C1.1	-	
B215	ปอลิฟต์	F1	P1	C1.1	-	
B216	ปอลิฟต์	F1	P1	C1.1	-	
B217	ถังเก็บน้ำ	F1	P1	C1.1	-	
T-B201	ห้องน้ำพนักงาน	F4.1	P6.2	C2.2	-	
ระดับชั้น B1						
B101	โถงลิฟต์	F4.2	P3	C2.1	B4	
B102	โถงลิฟต์ดับเพลิง	F4.2	P3	C2.1	B4	
B103	บันไดหนีไฟ ST-01	F2.2	P2.1	C1.2	B2	
B104	บันไดหนีไฟ ST-02	F2.2	P2.1	C1.2	B2	
B106	ห้องคนขับรถ	F8	P3	C1.2	-	
B108	โถงทางเดิน	F5.1	P4.1	C3	B4	
B109	ห้องพักผ่อนดูอากาศ	F2.2	P3	C1.2	B1	
B111	พื้นที่รับส่งสินค้า	F7	P3	C1.2	B6	
B112	ห้องทำงาน	F8	P3	C1.2	-	
B113	ห้องหัวหน้างาน	F8	P3	C1.2	-	
B114	ห้องเก็บของสำรอง	F8	P3	C1.2	-	
B115	ห้องเก็บของทำความสะอาด	F7	P6.1	C1.2	B6	
B116	ห้องเก็บของทั่วไป	F2.2	P3	C1.2	B1	
B117	ห้องเก็บผ้าสกรปรก	F7	P6.1	C1.2	B6	
B118	ห้องเก็บผ้าสะอาด	F7	P6.1	C1.2	B6	
B119	ห้องเตรียมวัสดุติดขั้นต้น F&B	F7	P6.1	C2.5	B6	
B120	ห้องเก็บอุปกรณ์ส่วนกลาง	F7	P6.1	C1.2	B6	
B121	ที่จอดรถ	F3	P2.1	C1.2	B1	
B123	แผนกของหาย	F2.2	P3	C1.2	B1	
B124	ทางเดิน	F7	P6.1	C1.2	B6	
B125	ห้อง รมภ.	F8	P3	C1.2	-	
B126	ห้องเก็บของ	F2.2	P3	C1.2	B1	
B127	โถงลิฟต์	F0	P0	C0	B0	
B128	ที่จอดรถมอเตอร์ไซด์	F3	P2.1	C1.2	B1	
B129	ห้องทำงาน	F8	P3	C1.2	-	
B130	ห้องทำงาน	F8	P3	C1.2	-	
B131	ห้องหัวหน้างาน	F8	P3	C1.2	-	
T-B101	ห้องน้ำพนักงาน	F4.1	P6.2	C2.2	-	
T-B102	ห้องน้ำคนขับรถ	F4.1	P6.2	C2.2	-	
ระดับชั้น G						
G01	โถงลิฟต์	F0	P0	C0	B0	
G02	โถงลิฟต์ดับเพลิง	F4.2	P3	C2.1	B4	
G03	บันไดหนีไฟ ST-01	F2.2	P2.1	C1.2	B2	
G04	บันไดหนีไฟ ST-02	F2.2	P2.1	C1.2	B2	
G05	โถงทางเข้า	F5.2	P4.1	C3	B4	
G06	พนักงานจอดรถ	F8	P3	C1.2	-	
G07	โถงต้อนรับ	F0	P0	C0	B0	
G08	ร้านกาแฟ	F0	P0	C0	B0	
G09	ห้องแม่บ้าน	F4.1	P6.2	C2.2	-	
G13	โถงทางเดิน	F0	P0	C0	B0	
G14	ห้องเก็บของ	F8	P3	C1.2	-	
G15	ห้องเก็บสัมภาระ	F8	P3	C1.2	-	
G16	ห้องรักษาความปลอดภัย	F9	P2.1	C2.4	B3	
G18	โถงทางเดิน	F4.2	P3	C2.1	B4	
G19	ห้องเก็บสิ่งของเดิม	F2.2	P3	C1.2	B1	
G20	ศูนย์สั่งการดับเพลิง	F9	P2.1	C2.4	B3	
G21	งานระบบ	F2.2	P3	C1.2	B1	
G22	ห้องพักขยะ	F7	P6.1	C2.5	B6	
G23	พื้นที่รับส่งผู้โดยสาร	F5.1	P4.1	C3	B4	
G24	ที่จอดรถห้องพักขยะ	F7	P3	C1.2	B6	
T-G01	ห้องน้ำผู้พิการ	F0	P0	C0	B0	

หมายเลข ห้อง	ชื่อห้อง	ผิวสำเร็จ			บัว เชิง ผนัง	หมายเหตุ
		พื้น	ผนัง	เพดาน		
T-G02	ห้องนำชาย	F0	P0	C0	B0	
T-G03	ห้องนำหญิง	F0	P0	C0	B0	
T-G04	ห้องนำพนักงาน	F4.1	P6.2	C2.2	-	
T-G11	ห้องหัวหน้างาน	F9	P2.1	C2.4	B3	
ระดับชั้น 1						
101	โถงลิฟต์	F5.2	P4.1	C3	B4	
102	โถงลิฟต์ดับเพลิง	F4.2	P3	C2.1	B4	
103	บันไดหนีไฟ ST-01	F2.2	P2.1	C1.2	B2	
104	บันไดหนีไฟ ST-02	F2.2	P2.1	C1.2	B2	
105	โถงทางเดิน	F5.2	P4.1	C3	B4	
106	โถงลิฟต์	F5.2	P4.1	C3	B4	
107	ที่จอดรถ	F3	P2.1	C1.2	B1	
108	ห้องเครื่องกำเนิดไฟฟ้าสำรอง	F6.1	P3	C1.2	B5	
ระดับชั้น 1A						
1A01	โถงทางเดิน	F5.2	P4.1	C3	B4	
1A02	โถงลิฟต์ดับเพลิง	F4.2	P3	C2.1	B4	
1A03	บันไดหนีไฟ ST-01	F2.2	P2.1	C1.2	B2	
1A04	บันไดหนีไฟ ST-02	F2.2	P2.1	C1.2	B2	
1A05	โถงทางเดิน	F5.2	P4.1	C3	B4	
1A06	โถงลิฟต์	F5.2	P4.1	C3	B4	
1A07	ที่จอดรถ	F3	P2.1	C1.2	B1	
ระดับชั้น 2						
201	โถงทางเดิน	F5.2	P4.1	C3	B4	
202	โถงลิฟต์ดับเพลิง	F4.2	P3	C2.1	B4	
203	บันไดหนีไฟ ST-01	F2.2	P2.1	C1.2	B2	
204	บันไดหนีไฟ ST-02	F2.2	P2.1	C1.2	B2	
205	โถงทางเดิน	F5.2	P4.1	C3	B4	
206	โถงลิฟต์	F5.2	P4.1	C3	B4	
207	ที่จอดรถ	F3	P2.1	C1.2	B1	
208	พื้นที่บริการรับจอดรถ	F4.2	P3	C2.1	B4	
209	งานระบบไฟฟ้าหลัก	F6.1	P3	C1.2	B5	
ระดับชั้น 2A						
2A01	ลาดที่จอดรถอัตโนมัติ	F1	P1	C1.1	-	
2A02	โถงลิฟต์ดับเพลิง	F4.2	P3	C2.1	B4	
2A03	บันไดหนีไฟ ST-01	F2.2	P2.1	C1.2	B2	
2A04	บันไดหนีไฟ ST-02	F2.2	P2.1	C1.2	B2	
2A04	โถงทางเดิน	F5.2	P4.1	C3	B4	
2A05	โถงลิฟต์	F5.2	P4.1	C3	B4	
2A06	พื้นที่บริการรับจอดรถ	F5.2	P4.1	C3	B4	
2A07	ที่จอดรถอัตโนมัติ	F3	P2.1	C1.2	B1	
T-2A01	ห้องน้ำพนักงาน	F4.1	P6.2	C2.2	-	
ระดับชั้น 2B						
2B01	โถงลิฟต์ดับเพลิง	F4.2	P3	C2.1	B4	
2B02	บันไดหนีไฟ ST-01	F2.2	P2.1	C1.2	B2	
2B03	บันไดหนีไฟ ST-02	F2.2	P2.1	C1.2	B2	
2B04	ห้องเครื่องทำน้ำเย็น	F6.1	P3	C1.2	B5	
ระดับชั้น 3						
301	โถงลิฟต์ดับเพลิง	F4.2	P3	C2.1	B4	
302	บันไดหนีไฟ ST-01	F2.2	P2.1	C1.2	B2	
303	บันไดหนีไฟ ST-02	F2.2	P2.1	C1.2	B2	
304	บันได ST-03	F2.2	P2.1	C1.2	B2	
305	ที่จอดรถอัตโนมัติ	F2.2	P2.1	C1.2	B2	
ระดับชั้น 3A						
3A01	โถงลิฟต์ดับเพลิง	F4.2	P3	C2.1	B4	
3A02	บันไดหนีไฟ ST-01	F2.2	P2.1	C1.2	B2	
3A03	บันไดหนีไฟ ST-02	F2.2	P2.1	C1.2	B2	
3A04	ที่จอดรถอัตโนมัติ	F2.2	P2.1	C1.2	B2	
3A05	หอยถอยเย็น	F6.1	P3	C1.2	B5	
3A06	บันได ST-03	F2.2	P2.1	C1.2	B2	
ระดับชั้น 4						
401	โถงลิฟต์ดับเพลิง	F4.2	P3	C2.1	B4	
402	บันไดหนีไฟ ST-01	F2.2	P2.1	C1.2	B2	
403	บันไดหนีไฟ ST-02	F2.2	P2.1	C1.2	B2	
404	บันได ST-03	F2.2	P2.1	C1.2	B2	
405	ที่จอดรถอัตโนมัติ	F2.2	P2.1	C1.2	B2	
ระดับชั้น 4A						
4A01	โถงลิฟต์ดับเพลิง	F4.2	P3	C2.1	B4	
4A02	บันไดหนีไฟ ST-01	F2.2	P2.1	C1.2	B2	
4A03	บันไดหนีไฟ ST-02	F2.2	P2.1	C1.2	B2	
4A04	บันได ST-03	F2.2	P2.1	C1.2	B2	

หมายเลข ห้อง	ชื่อห้อง	ผิวสำเร็จ			บัว เชิง ผนัง	หมายเหตุ
		พื้น	ผนัง	เพดาน		
4A05	ที่จอดรถอัตโนมัติ	F2.2	P2.1	C1.2	B2	
ระดับชั้น 5						
501	โถงลิฟต์ดับเพลิง	F4.2	P3	C2.1	B4	
502	บันไดหนีไฟ ST-01	F2.2	P2.1	C1.2	B2	
503	บันไดหนีไฟ ST-02	F2.2	P2.1	C1.2	B2	
504	บันได ST-03	F2.2	P2.1	C1.2	B2	
505	ที่จอดรถอัตโนมัติ	F2.2	P2.1	C1.2	B2	
ระดับชั้น 6 (BALLROOM)						
601	โถงลิฟต์	F0	P0	C0	B0	
602	โถงลิฟต์ดับเพลิง	F4.2	P3	C2.1	B4	
603	โถงบันไดหนีไฟ	F0	P0	C0	B0	
604	บันไดหนีไฟ ST-01	F2.2	P2.1	C1.2	B2	
605	บันไดหนีไฟ ST-02	F2.2	P2.1	C1.2	B2	
606	ห้องแต่งตัวเจ้าสาว	F0	P0	C0	B0	
607	พื้นที่สีเขียว	F2.1	P2.2	-	-	
608	ห้องจัดเลี้ยง	F1	P2	C1		
610	โถงพักคอยห้องจัดเลี้ยง	F0	P0	C0	B0	
612	ห้องเก็บของ	F4.1	P6.2	C2.2	-	
613	ห้องควบคุม	F0	P0	C0	B0	
614	ห้องเก็บของ	F7	P6.1	C2.5	B6	
615	ห้องเก็บของ	F7	P6.1	C2.5	B6	
616	โถงทางเดิน	F0	P0	C0	B0	
617	พื้นที่ล้างจาน	F7	P6.1	C2.5	B6	
618	ครัวสำหรับห้องจัดเลี้ยง	F7	P6.1	C2.5	B6	
619	ครัวเย็น (ปรับอากาศ 18°C)	F0.2	P0.2	C0.2	B0.2	
620	ห้องเย็น	F0.2	P0.2	C0.2	B0.2	
621	ห้องเก็บเพอร์นิเจอร์	F8	P3	C1.2	-	
622	ห้องเตรียมเครื่องดื่ม (ปรับอากาศ)	F7	P6.1	C2.5	B6	
T-601	ห้องน้ำผู้หญิง	F0	P0	C0	B0	
T-602	ห้องน้ำผู้พิการ	F0	P0	C0	B0	
T-603	ห้องน้ำผู้ชาย	F0	P0	C0	B0	
T-604	ห้องน้ำ	F0	P0	C0	B0	
ระดับชั้น 6A						
6A01	โถงลิฟต์ดับเพลิง	F4.2	P3	C2.1	B4	
6A02	บันไดหนีไฟ ST-01	F2.2	P2.1	C1.2	B2	
6A03	บันไดหนีไฟ ST-02	F2.2	P2.1	C1.2	B2	
6A04	งานระบบปรับอากาศ	F6.1	P3	C1.2	B5	
6A05	ห้องสารเคมี	F7	P6.1	C2.5	B6	
6A06	ห้องเย็น	F0.2	P0.2	C0.2	B0.2	
6A07	ห้องเย็น	F0.2	P0.2	C0.2	B0.2	
6A08	โถงทางเดิน	F7	P6.1	C2.5	B6	
6A09	ห้องหัวหน้างาน	F9	P2.1	C2.4	B3	
6A10	ห้องทำงาน	F9	P2.1	C2.4	B3	
6A11	ห้องเย็น	F0.2	P0.2	C0.2	B0.2	
6A12	ห้องเย็น	F0.2	P0.2	C0.2	B0.2	
6A13	ห้องเย็น	F0.2	P0.2	C0.2	B0.2	
6A14	ห้องเก็บเครื่องดื่ม	F7	P6.1	C2.5	B6	
6A15	ห้องเก็บอาหาร	F7	P6.1	C2.5	B6	
6A16	ห้องล้างอุปกรณ์	F7	P6.1	C2.5	B6	
6A17	ห้องเย็น	F0.2	P0.2	C0.2	B0.2	
6A18	ห้องเก็บอาหารทะเล	F7	P6.1	C2.5	B6	
6A19	ห้องเก็บเนื้อสัตว์	F7	P6.1	C2.5	B6	
6A20	ห้องเย็น	F0.2	P0.2	C0.2	B0.2	
6A21	ห้องเย็น	F0.2	P0.2	C0.2	B0.2	
6A22	ห้องเก็บแข็ง	F7	P6.1	C2.5	B6	
6A23	ห้องเย็น	F0.2	P0.2	C0.2	B0.2	
6A24	ห้องเย็น	F0.2	P0.2	C0.2	B0.2	
6A25	ห้องอบขนม	F7	P6.1	C2.5	B6	
6A26	ห้องเบเกอรี่	F7	P6.1	C2.5	B6	
6A27	ห้องเก็บผักและผลไม้	F7	P6.1	C2.5	B6	
6A28	ห้องเย็น	F0.2	P0.2	C0.2	B0.2	
6A29	ห้องเย็น	F0.2	P0.2	C0.2	B0.2	
6A30	ห้องระบบปรับอากาศ	F6.1	P3	C1.2	B5	
ระดับชั้น 7						
701	โถงทางเดิน	F4.2	P2.1	C2.1	B4	
702	โถงลิฟต์ดับเพลิง	F4.2	P3	C2.1	B4	
703	บันไดหนีไฟ ST-01	F2.2	P2.1	C1.2	B2	
704	บันไดหนีไฟ ST-02	F2.2	P2.1	C1.2	B2	
705	ห้องล้างจาน	F7	P6.1	C2.5	B6	

หมายเลข ห้อง	ชื่อห้อง	ผิวสำเร็จ			บัว	หมายเหตุ
		พื้น	ผนัง	เพดาน	ผนัง	
706	งานระบบ	F6.1	P3	C1.2	B5	
707	ทรัพยากรมนุษย์	F9	P2.1	C2.4	B3	
708	สัณภาษณ์	F9	P2.1	C2.4	B3	
709	ส่วนต้อนรับ	F4.2	P2.1	C2.1	B4	
710	ห้องปฐมพยาบาล	F9	P2.1	C2.4	B3	
711	โรงอาหารพนักงาน	F4.2	P2.1	C2.4	B4	
712	ห้องครัวพนักงาน	F7	P6.1	C2.5	B6	
713	ห้องทำงาน	F9	P2.1	C2.4	B3	
714	GM	F9	P2.1	C2.4	B3	
715	ประชาสัมพันธ์	F9	P2.1	C2.4	B3	
716	แผนกอาหารและเครื่องดื่ม	F9	P2.1	C2.4	B3	
717	แคชเชียร์	F9	P2.1	C2.4	B3	
718	งานระบบปรับอากาศ	F6.1	P3	C1.2	B5	
719	ห้องรับรองพนักงาน	F9	P2.1	C2.4	B3	
720	ห้องศูนย์ฟอร์ม	F8	P3	C1.2	-	
721	ห้องผู้จัดการซีกรีด	F8	P3	C1.2	-	
722	ห้องซีกรีด	F7	P6.1	C2.5	B6	
723	ห้องเย็น	F0.2	P0.2	C0.2	B0.2	
724	ห้องเก็บอาหาร	F7	P6.1	C2.5	B6	
725	ห้องหัวหน้างาน	F9	P2.1	C2.4	B3	
T-701	ห้องน้ำชาย	F4.1	P6.2	C2.2	-	
T-702	ห้องน้ำหญิง	F4.1	P6.2	C2.2	-	
T-703	ห้องน้ำชาย	F4.1	P6.2	C2.2	-	
T-704	ห้องน้ำหญิง	F4.1	P6.2	C2.2	-	
ระดับชั้น 8 (GUESTROOM)						
801	โถงลิฟต์	F0	P0	C0	B0	
802	โถงลิฟต์ต้นเพลิง	F4.2	P3	C2.1	B4	
803	บันไดหนีไฟ ST-01	F2.2	P2.1	C1.2	B2	
804	บันไดหนีไฟ ST-02	F2.2	P2.1	C1.2	B2	
805	งานระบบไฟฟ้า	F2.2	P2.1	C1.2	B2	
806	ห้องเก็บของ	F4.2	P3	C2.1	B4	
807	ห้องแม่บ้าน	F4.2	P3	C2.1	B4	
808	ห้องเก็บผ้า	F7	P6.1	C2.5	B6	
809	ห้องพัก	F0	P0	C0	B0	
810	ห้องพัก	F0	P0	C0	B0	
811	ห้องพัก	F0	P0	C0	B0	
812	ห้องพัก	F0	P0	C0	B0	
813	ห้องน้ำ	F0	P0	C0	B0	
814	ห้องพัก	F0	P0	C0	B0	
815	ห้องพัก	F0	P0	C0	B0	
816	ห้องพัก	F0	P0	C0	B0	
817	ห้องพัก	F0	P0	C0	B0	
818	ห้องพัก	F0	P0	C0	B0	
819	ห้องพัก	F0	P0	C0	B0	
820	ห้องพัก	F0	P0	C0	B0	
821	ห้องพัก	F0	P0	C0	B0	
822	ห้องพัก	F0	P0	C0	B0	
823	ห้องพัก	F0	P0	C0	B0	
824	โถงทางเดิน	F0	P0	C0	B0	
825	โถงทางเดิน	F0	P0	C0	B0	
826	ทางเดิน	F4.2	P3	C2.1	B4	
827	ระเบียบ	F0.3	P2.2	-	-	
828	ระเบียบ	F0.3	P2.2	-	-	
T-801	ห้องนำพนักงาน	F4.2	P3	C2.1	B4	

หมายเลข ห้อง	ชื่อห้อง	ผิวสำเร็จ			บัวเชิง		หมายเหตุ
		พื้น	ผนัง	เพดาน	ผนัง		
ระดับชั้น 9 (GUESTROOM)							
901	โถงลิฟต์	F0	P0	C0	B0		
902	โถงลิฟต์ดับเพลิง	F4.2	P3	C2.1	B4		
903	บันไดหนีไฟ ST-01	F2.2	P2.1	C1.2	B2		
904	บันไดหนีไฟ ST-02	F2.2	P2.1	C1.2	B2		
905	ห้องพัก	F0	P0	C0	B0		
906	ห้องพัก	F0	P0	C0	B0		
907	ห้องพัก						
908	ห้องพัก	F0	P0	C0	B0		
909	ห้องพักผู้พิการ	F0	P0	C0	B0		
910	ห้องพัก	F0	P0	C0	B0		
911	ห้องพัก	F0	P0	C0	B0		
912	ห้องพัก	F0	P0	C0	B0		
913	ห้องพัก	F0	P0	C0	B0		
914	ห้องพัก	F0	P0	C0	B0		
915	ห้องพัก	F0	P0	C0	B0		
916	งานระบบ	F6.1	P3	C1.2	B5		
917	ห้องเก็บของ	F4.2	P3	C2.1	B4		
918	ห้องพนักงาน	F4.1	P6.2	C2.2	-		
919	ห้องเก็บผ้า	F4.2	P3	C2.1	B4		
920	ห้องพัก	F0	P0	C0	B0		
921	ห้องพัก	F0	P0	C0	B0		
922	ห้องพัก	F0	P0	C0	B0		
923	ห้องพัก	F0	P0	C0	B0		
924	โถงทางเดิน	F0	P0	C0	B0		
925	โถงทางเดิน	F0	P0	C0	B0		
926	โถงทางเดิน	F4.2	P3	C2.1	B4		

หมายเลข ห้อง	ชื่อห้อง	ผิวสำเร็จ			บัว เชิงผนัง	หมายเหตุ
		พื้น	ผนัง	เพดาน		
ระดับชั้น 24 (ALL DAY DINING)						
2401	โถงลิฟต์	F0	P0	C0	B0	
2402	โถงลิฟต์ดับเพลิง	F4.2	P3	C2.1	B4	
2403	บันไดหนีไฟ ST-01	F2.2	P2.1	C1.2	B2	
2404	บันไดหนีไฟ ST-02	F2.2	P2.1	C1.2	B2	
2405	ร้านอาหารพิเศษ	F0	P0	C0	B0	
2406	ห้องเย็น	F0.2	P0.2	C0.2	B0.2	
2407	คลังลานจ์	F0	P0	C0	B0	
2408	ห้องไฟฟ้า	F6.1	P3	C1.2	B5	
2409	ห้องครัว	F7	P6.1	C2.5	B6	
2410	ที่ล้างจาน	F7	P6.1	C2.5	B6	
2411	โถงทางเดิน	F0	P0	C0	B0	
2412	ห้องเย็น	F0.2	P0.2	C0.2	B0.2	
2413	ห้องล้างจาน	F7	P6.1	C2.5	B6	
2415	ครัวเย็น	F0.2	P0.2	C0.2	B0.2	
2416	ห้องครัว	F7	P6.1	C2.5	B6	
2417	โถงทางเข้า	F7	P6.1	C2.5	B6	
2418	ห้องแม่บ้าน	F4.2	P3	C2.1	B4	
2419	ห้องอาหาร	F0	P0	C0	B0	
T-2401	ห้องน้ำชาย	F0	P0	C0	B0	
T-2402	ห้องน้ำหญิง	F0	P0	C0	B0	
T-2403	ห้องน้ำชาย	F0	P0	C0	B0	
T-2404	ห้องน้ำผู้พิการ	F0	P0	C0	B0	
T-2405	ห้องน้ำหญิง	F0	P0	C0	B0	

ระดับชั้น 25 (WELLNESS)						
2501	โถงลิฟต์	F0	P0	C0	B0	
2502	โถงลิฟต์ดับเพลิง	F4.2	P3	C2.1	B4	
2503	โถงทางเดิน	F4.2	P3	C2.1	B4	
2504	บันไดหนีไฟ ST-01	F2.2	P2.1	C1.2	B2	
2505	บันไดหนีไฟ ST-02	F2.2	P2.1	C1.2	B2	
2506	งานระบบ	F6.1	P3	C1.2	B5	
2507	เตรียมอาหาร	F7	P6.1	C2.5	B6	
2508	ห้องพนักงานทำความสะอาด	F4.2	P3	C2.1	B4	
2509	ห้องทรีตเมนต์คู่	F0	P0	C0	B0	
2510	ห้องทรีตเมนต์เดี่ยว	F0	P0	C0	B0	
2511	ห้องทรีตเมนต์เดี่ยว	F0	P0	C0	B0	
2512	โถงทางเดิน	F0	P0	C0	B0	
2513	ส่วนต้อนรับ	F0	P0	C0	B0	

หมายเลขห้อง	ชื่อห้อง	ผิวสำเร็จ			บัวเชิงผนัง	หมายเหตุ
		พื้น	ผนัง	เพดาน		
2514	สำนักงานและห้องเก็บของ	F0	P0	C0	B0	
2515	WELLNESS CUISINE	F0	P0	C0	B0	
2516	ห้องชาวน้ำ	F0	P0	C0	B0	
2517	ห้องอบไอน้ำ	F0	P0	C0	B0	
2520	ห้องชาวน้ำ	F0	P0	C0	B0	
2521	ห้องอบไอน้ำ	F0	P0	C0	B0	
2522	โถงทางเดิน	F0	P0	C0	B0	
2523	ส่วนต้อนรับ	F0	P0	C0	B0	
2524	จุดบริการ	F0	P0	C0	B0	
2525	ล็อกเกอร์	F0	P0	C0	B0	
2526	ล็อกเกอร์	F0	P0	C0	B0	
2527	ห้องออกกำลังกาย	F0	P0	C0	B0	
2528	ห้องทรีตเมนต์เดี่ยว	F0	P0	C0	B0	
2529	ห้องทรีตเมนต์เดี่ยวพิเศษ	F0	P0	C0	B0	
2531	คิอสต์ลับ	F0	P0	C0	B0	
2532	โถงทางเดิน	F0	P0	C0	B0	
2533	SHOWER	F0	P0	C0	B0	
2536	SHOWER	F0	P0	C0	B0	
2537	ห้องอาบน้ำ	F0	P0	C0	B0	
2538	SHOWER	F0	P0	C0	B0	
2539	SHOWER	F0	P0	C0	B0	
T2501	ห้องน้ำ	F0	P0	C0	B0	
T2502	ห้องน้ำชาย	F0	P0	C0	B0	
T2503	ห้องน้ำหญิง	F0	P0	C0	B0	

ระดับชั้น 26						
2601	งานระบบปั้มน้ำสระว่ายน้ำ	F2.2	P3	C1.2	B1	
2602	ถังเก็บน้ำ	F1	P1	C1.1	-	
2603	ถังเก็บน้ำ	F1	P1	C1.1	-	
2604	ถังเก็บน้ำ	F1	P1	C1.1	-	
2605	ถังเก็บน้ำ	F1	P1	C1.1	-	
2606	ถังเก็บน้ำ	F1	P1	C1.1	-	
2607	โถงลิฟต์ดับเพลิง	F4.2	P3	C2.1	B4	
2608	บันไดหนีไฟ ST-02	F2.2	P2.1	C1.2	B2	
2609	บันไดหนีไฟ ST-01	F2.2	P2.1	C1.2	B2	
2610	EE.	F6.1	P3	C1.2	B5	
2611	ห้องระบบปรับอากาศ	F2.2	P3	C1.2	B1	
2612	ห้องระบบเติมอากาศ	F2.2	P3	C1.2	B1	
2613	ห้องระบบเติมอากาศ	F2.2	P3	C1.2	B1	

ระดับชั้น 27 (SWIMMING POOL)						
2701	โถงลิฟต์	F0	P0	C0	B0	
2702	โถงลิฟต์ดับเพลิง	F4.2	P3	C2.1	B4	
2703	บันไดหนีไฟ ST-01	F2.2	P2.1	C1.2	B2	
2704	บันไดหนีไฟ ST-02	F2.2	P2.1	C1.2	B2	
2705	โถงทางเดิน	F0.3	P0.3	C0.3	-	
2706	สระว่ายน้ำ	F0.3	P0.2	-	-	
2707	วารีบำบัด	F0.3	P0.2	-	-	
2708	ระเบียงซ่อมบำรุง	F2.1	P2.2	-	-	
2709	บาร์	F0.3	P0.3	-	-	
2710	บริการ	F4.1	P6.2	C2.2	-	
2713	ห้องครัว	F7	P6.1	C2.5	B6	
2714	โถงทางเดิน	F0.3	P0.3	C0.3	-	
2715	SHOWER	F0	P0	C0	B0	
2716	SHOWER	F0	P0	C0	B0	
2717	SHOWER	F0	P0	C0	B0	
2718	SHOWER	F0	P0	C0	B0	
T-2701	ห้องน้ำหญิง	F0	P0	C0	B0	
T-2702	ห้องน้ำชาย	F0	P0	C0	B0	

ระดับชั้น 28 (LOBBY)						
2801	โถงลิฟต์	F0	P0	C0	B0	
2802	โถงลิฟต์ดับเพลิง	F4.2	P3	C2.1	B4	
2803	บันไดหนีไฟ ST-01	F2.2	P2.1	C1.2	B2	
2804	บันไดหนีไฟ ST-02	F2.2	P2.1	C1.2	B2	
2805	โถงต้อนรับ	F0	P0	C0	B0	
2806	สำนักงาน	F9	P2.1	C2.4	B3	
2807	เตรียมอาหาร	F7	P6.1	C2.5	B6	
2808	โถงทางเดิน	F0	P0	C0	B0	

หมายเลขห้อง	ชื่อห้อง	ผิวสำเร็จ			บัวเชิงผนัง	หมายเหตุ
		พื้น	ผนัง	เพดาน		
T-2801	ห้องน้ำชาย	F0	P0	C0	B0	
T-2802	ห้องน้ำผู้พิการ	F0	P0	C0	B0	
T-2803	ห้องน้ำหญิง	F0	P0	C0	B0	

ระดับชั้น 29						
2901	โถงลิฟต์ดับเพลิง	F4.2	P3	C2.1	B4	
2902	บันไดหนีไฟ ST-01	F2.2	P2.1	C1.2	B2	
2903	บันไดหนีไฟ ST-02	F2.2	P2.1	C1.2	B2	
2904	ห้องเก็บของ	F8	P3	C1.2	-	
T-2901	ห้องน้ำหญิง	F4.1	P6.2	C2.2	-	
T-2902	ห้องน้ำชาย	F4.1	P6.2	C2.2	-	

ระดับชั้นคาดฟ้า						
3001	โถงลิฟต์	F0	P0	C0	B0	
3002	โถงบริการ	F7	P6.1	C2.5	B6	
3003	บันไดหนีไฟ ST-01	F2.2	P2.1	C1.2	B2	
3004	บันไดหนีไฟ ST-02	F2.2	P2.1	C1.2	B2	
3005	ห้องเครื่องระบบลิฟต์	F2.2	P3	C1.2	B1	
3006	ห้องเครื่องระบบลิฟต์	F2.2	P3	C1.2	B1	
3007	โถงบันไดวน	F0	P0	C0	B0	
3008	บาร์คาดฟ้า	F0	P0	C0	B0	
3009	ส่วนต้อนรับ	F0	P0	C0	B0	
3010	ทางเดิน	F0	P0	C0	B0	
3011	ส่วนต้อนรับ	F0	P0	C0	B0	
T-3001	ห้องน้ำหญิง	F0	P0	C0	B0	
T-3002	ห้องน้ำผู้พิการ	F0	P0	C0	B0	
T-3003	ห้องน้ำชาย	F0	P0	C0	B0	

ระดับชั้น 10X10						
R-01	พื้นที่10 X 10	F0.3	P2.2	-	-	
R-02	บาร์คาดฟ้า	F0.3	P2.2	-	-	
R-03	บาร์คาดฟ้า	F0.3	P2.2	-	-	
R-04	หลังคา ค.ส.ล.	F2.1	P2.2	-	-	
R-05	บาร์คาดฟ้า	F0.3	P2.2	-	-	
R-06	หลังคา ค.ส.ล.	F0.3	P2.2	-	-	
R-07	ทางเดิน	F0.3	P2.2	-	-	

รายการวัสดุผิวสำเร็จ

วัสดุผิวพื้น

- F0.1 พื้น ค.ส.ล. เพลียผิว (รองานตกแต่งภายใน)
- F0.2 พื้น ค.ส.ล. เพลียผิว (รองานที่ปรึกษางานครัว)
- F0.3 พื้น ค.ส.ล. เพลียผิว (รองานภูมิสถาปัตยกรรม)
- F1 พื้น ค.ส.ล. ปรับระดับ ทำผิวขัดเรียบ
- F2.1 พื้น ค.ส.ล. เทคอนกรีตเสริมเหล็กปรับระดับ ทำผิวขัดมัน
- F2.2 พื้น ค.ส.ล. เทปูนทรายปรับระดับ ทำผิวขัดมัน
- F2.3 พื้น ค.ส.ล. เทปูนทรายปรับระดับ ทำผิวขัดมัน โรยกรวดแม่น้ำ สีดำ ขนาดเส้นผ่านศูนย์กลาง 30-50 มม. สูง 100 มม.
- F3 พื้น ค.ส.ล. ทำผิว FLOOR HARDENER สีเทามาตรฐาน ผิวด้าน อัตราส่วน 5 กก./ตร.ม.
- F4.1 พื้น ค.ส.ล. เทปูนทรายปรับระดับ ปูกระเบื้อง PORCELAIN ระบุนุ่นและสีภายหลัง ผิวเรียบ ขนาด 600x600 มม.
- F4.2 พื้น ค.ส.ล. เทปูนทรายปรับระดับ ปูกระเบื้อง PORCELAIN ระบุนุ่นและสีภายหลัง ผิวด้าน ขนาด 600x600 มม.
- F5.1 พื้น ค.ส.ล. เทปูนทรายปรับระดับ ปูหินแกรนิต COBBLE STONE ต่างประเทศ คำนวณโดยผิวป่าไว้พื้นไฟ ขนาด 100x100 มม.หนา 50 มม.
- F5.2 พื้น ค.ส.ล. เทปูนทรายปรับระดับ ปูหินอ่อนต่างประเทศ ระบุนสี ผิว และขนาดภายหลัง หนา 20 มม.
- F6 พื้น ค.ส.ล. เทปูนทรายปรับระดับ ทำผิวเคลือบ EPOXY ชนิด SELF LEVELING สีเทา หนา 2 มม.
- F7 พื้น ค.ส.ล. เทปูนทรายปรับระดับ ทำผิวเคลือบ POLYURETHANE ชนิด SELF LEVELING สีเทา หนา 2 มม.
- F8 พื้น ค.ส.ล. เทปูนทรายปรับระดับ ทำผิวขัดมัน ปูกระเบื้องยาง ระบุนุ่น สีและขนาดภายหลัง
- F9 พื้น ค.ส.ล. เทปูนทรายปรับระดับ ทำผิวขัดมัน ปูพรม CARPET TILE ระบุนุ่น สีและขนาดภายหลัง

วัสดุผิวผนัง

- P0.1 รองานตกแต่งภายใน
- P0.2 รองานที่ปรึกษางานครัว
- P0.3 รองานภูมิสถาปัตยกรรม
- P1 คอมนกรีตแต่งผิวเรียบ
- P2.1 ทาสี
- P2.2 ทาสี
- P3 ทาสีน้ำมันสูง 2000 มม. ตอมบนทาสีน้ำ
- P4.1 บัว ALUMINIUM COMPOSITE PANEL สีลายไม้ ระบุสีภายหลัง หนา 4 มม. รอยต่อเว้นร่อง 10 มม.
- ยาแนวด้วย NON-STAINING SILICONE SEALANT แบ่งแนว ตามแบบ
- โครงคร่าวเหล็ก ขนาดตามแบบ ติดตั้งตามมาตรฐานผู้ผลิต เสนอแบบขออนุมัติก่อนดำเนินการ
- P5 ยิปซัมบอร์ด ชนิดทนไฟ ขอบลาด ระบุความหนาภายหลัง จาบริยต่อเรียบ ทาสี
- โครงคร่าวเหล็กชุบสังกะสี ติดตั้งตามมาตรฐานผู้ผลิต
- P6.1 ปูกระเบื้อง PORCELAIN ระบุนุ่น สีและผิวภายหลัง ขนาด 600x600 มม.
- P6.2 ปูกระเบื้อง PORCELAIN ระบุนุ่น สีและผิวภายหลัง ขนาด 600x600 มม.

วัสดุผิวเพดาน

- C0.1 รองานตกแต่งภายใน
- C0.2 รองานที่ปรึกษางานครัว
- C1.1 ห้องพื้นคอนกรีตแต่งผิวเรียบ
- C1.2 ห้องพื้นคอนกรีตแต่งผิวเรียบ ทาสี
- C2.1 ยิปซัมบอร์ด ชนิดธรรมดา ขอบลาด หนา 9 มม. จาบริยต่อเรียบ ทาสี
- C2.2 ยิปซัมบอร์ด ชนิดทนความชื้น ขอบลาด หนา 12 มม. จาบริยต่อเรียบ ทาสี
- โครงคร่าวเหล็กชุบสังกะสี ติดตั้งตามมาตรฐานผู้ผลิต
- C2.3 ยิปซัมบอร์ดชนิดเคลือบผิวหน้าด้วยใยแก้ว รุ่น GLASROC X ขอบลาด หนา 12.5 มม. พร้อมวัสดุสำหรับฉาบเต็มแผ่น ทาสี
- โครงคร่าวเหล็กชุบสังกะสี ติดตั้งตามมาตรฐานผู้ผลิต
- C2.4 ACOUSTIC BOARD ชนิด MINERAL FIBER ขอบบั้งใบเล็ก ขนาด 600x1200 มม. ความหนาไม่น้อยกว่า 15 มม.
- โครงคร่าว T-BAR เหล็กชุบสังกะสีเคลือบสีขาว ติดตั้งตามมาตรฐานผู้ผลิต
- C2.5 ยิปซัมบอร์ด ชนิดทนความชื้น ภูมิหน้าด้วย VINYL หนา 12 มม. ขนาด 600x600 มม.
- โครงคร่าว T-BAR เหล็กชุบสังกะสีเคลือบสีขาว # 600x600 มม. ติดตั้งตามมาตรฐานผู้ผลิต
- C3 บัว ALUMINIUM COMPOSITE PANEL ลายไม้ ระบุสีภายหลัง หนา 4 มม. รอยต่อเว้นร่อง 10 มม.
- ยาแนวด้วย NON-STAINING SILICONE SEALANT แบ่งแนว ตามแบบ
- โครงคร่าวเหล็ก ขนาดตามแบบ ติดตั้งตามมาตรฐานผู้ผลิต เสนอแบบขออนุมัติก่อนดำเนินการ

วัสดุบัวเชิงผนัง

- B0.1 รองานตกแต่งภายใน
- B0.2 รองานที่ปรึกษางานครัว
- B1 ทำผิวขัดมัน สูง 100 มม. เขาะร่องแบ่งแนว กว้าง 10 มม. ลึก 5 มม.
- B2 ทำผิวขัดมัน สูง 100 มม. ลึกลงแนววัสดุผนัง 10 มม.
- B3 อะลูมิเนียม ระบุนสีภายหลัง สูง 100 มม.
- B4 กระเบื้องรุ่นเดียวกับพื้น สูง 100 มม. ปูเรียบเสมอผิวผนัง
- B5 ทำผิวเคลือบ EPOXY สูง 100 มม.
- B6 ทำผิวเคลือบ POLYURETHANE สูง 100 มม.

OWNER
LUXURY HOTEL DEVELOPMENT
SUKHUMVIT 38 CO., LTD.

DESIGNER

ARCHITECTS 49 LIMITED
81 SUKHUMVIT 26
BANGKOK 10110 THAILAND
T + 66 (0) 2260 4370
F + 66 (0) 2259 3872
E A49@A49.CO.TH
W A49.CO.TH



K.C.S. & ASSOCIATES CO. LTD.
22ND FLOOR, CHARN ISSARA TOWER II
2522/267 NEW PETCHABURI ROAD, BANGKAPI,
HUAY KWANG, BAKOK 10310 THAILAND
T +66 (0) 2308 2481 5
F +66 (0) 2308 2485




MEC PRO DESIGN CO. LTD.
567 BUILDING 4TH FLOOR 1X SOI 51
SUAN LUANG, BANGKOK 10250 THAILAND
T +66 (0) 2170 8029
+66 (0) 37 034 8917
E MECPRO.DESIGN@GMAIL.COM




P LANDSCAPE CO. LTD.
59/3 SUKHUMVIT 39, KLONGTON NUA,
WATTANA, BANGKOK 10110 THAILAND
T (622) 261 3700 TO 9
F (622) 238 3388
E INFO@PLANDSCAPE.COM
W WWW.PLANDSCAPE.COM



4/18/2026 3:14:53 PM

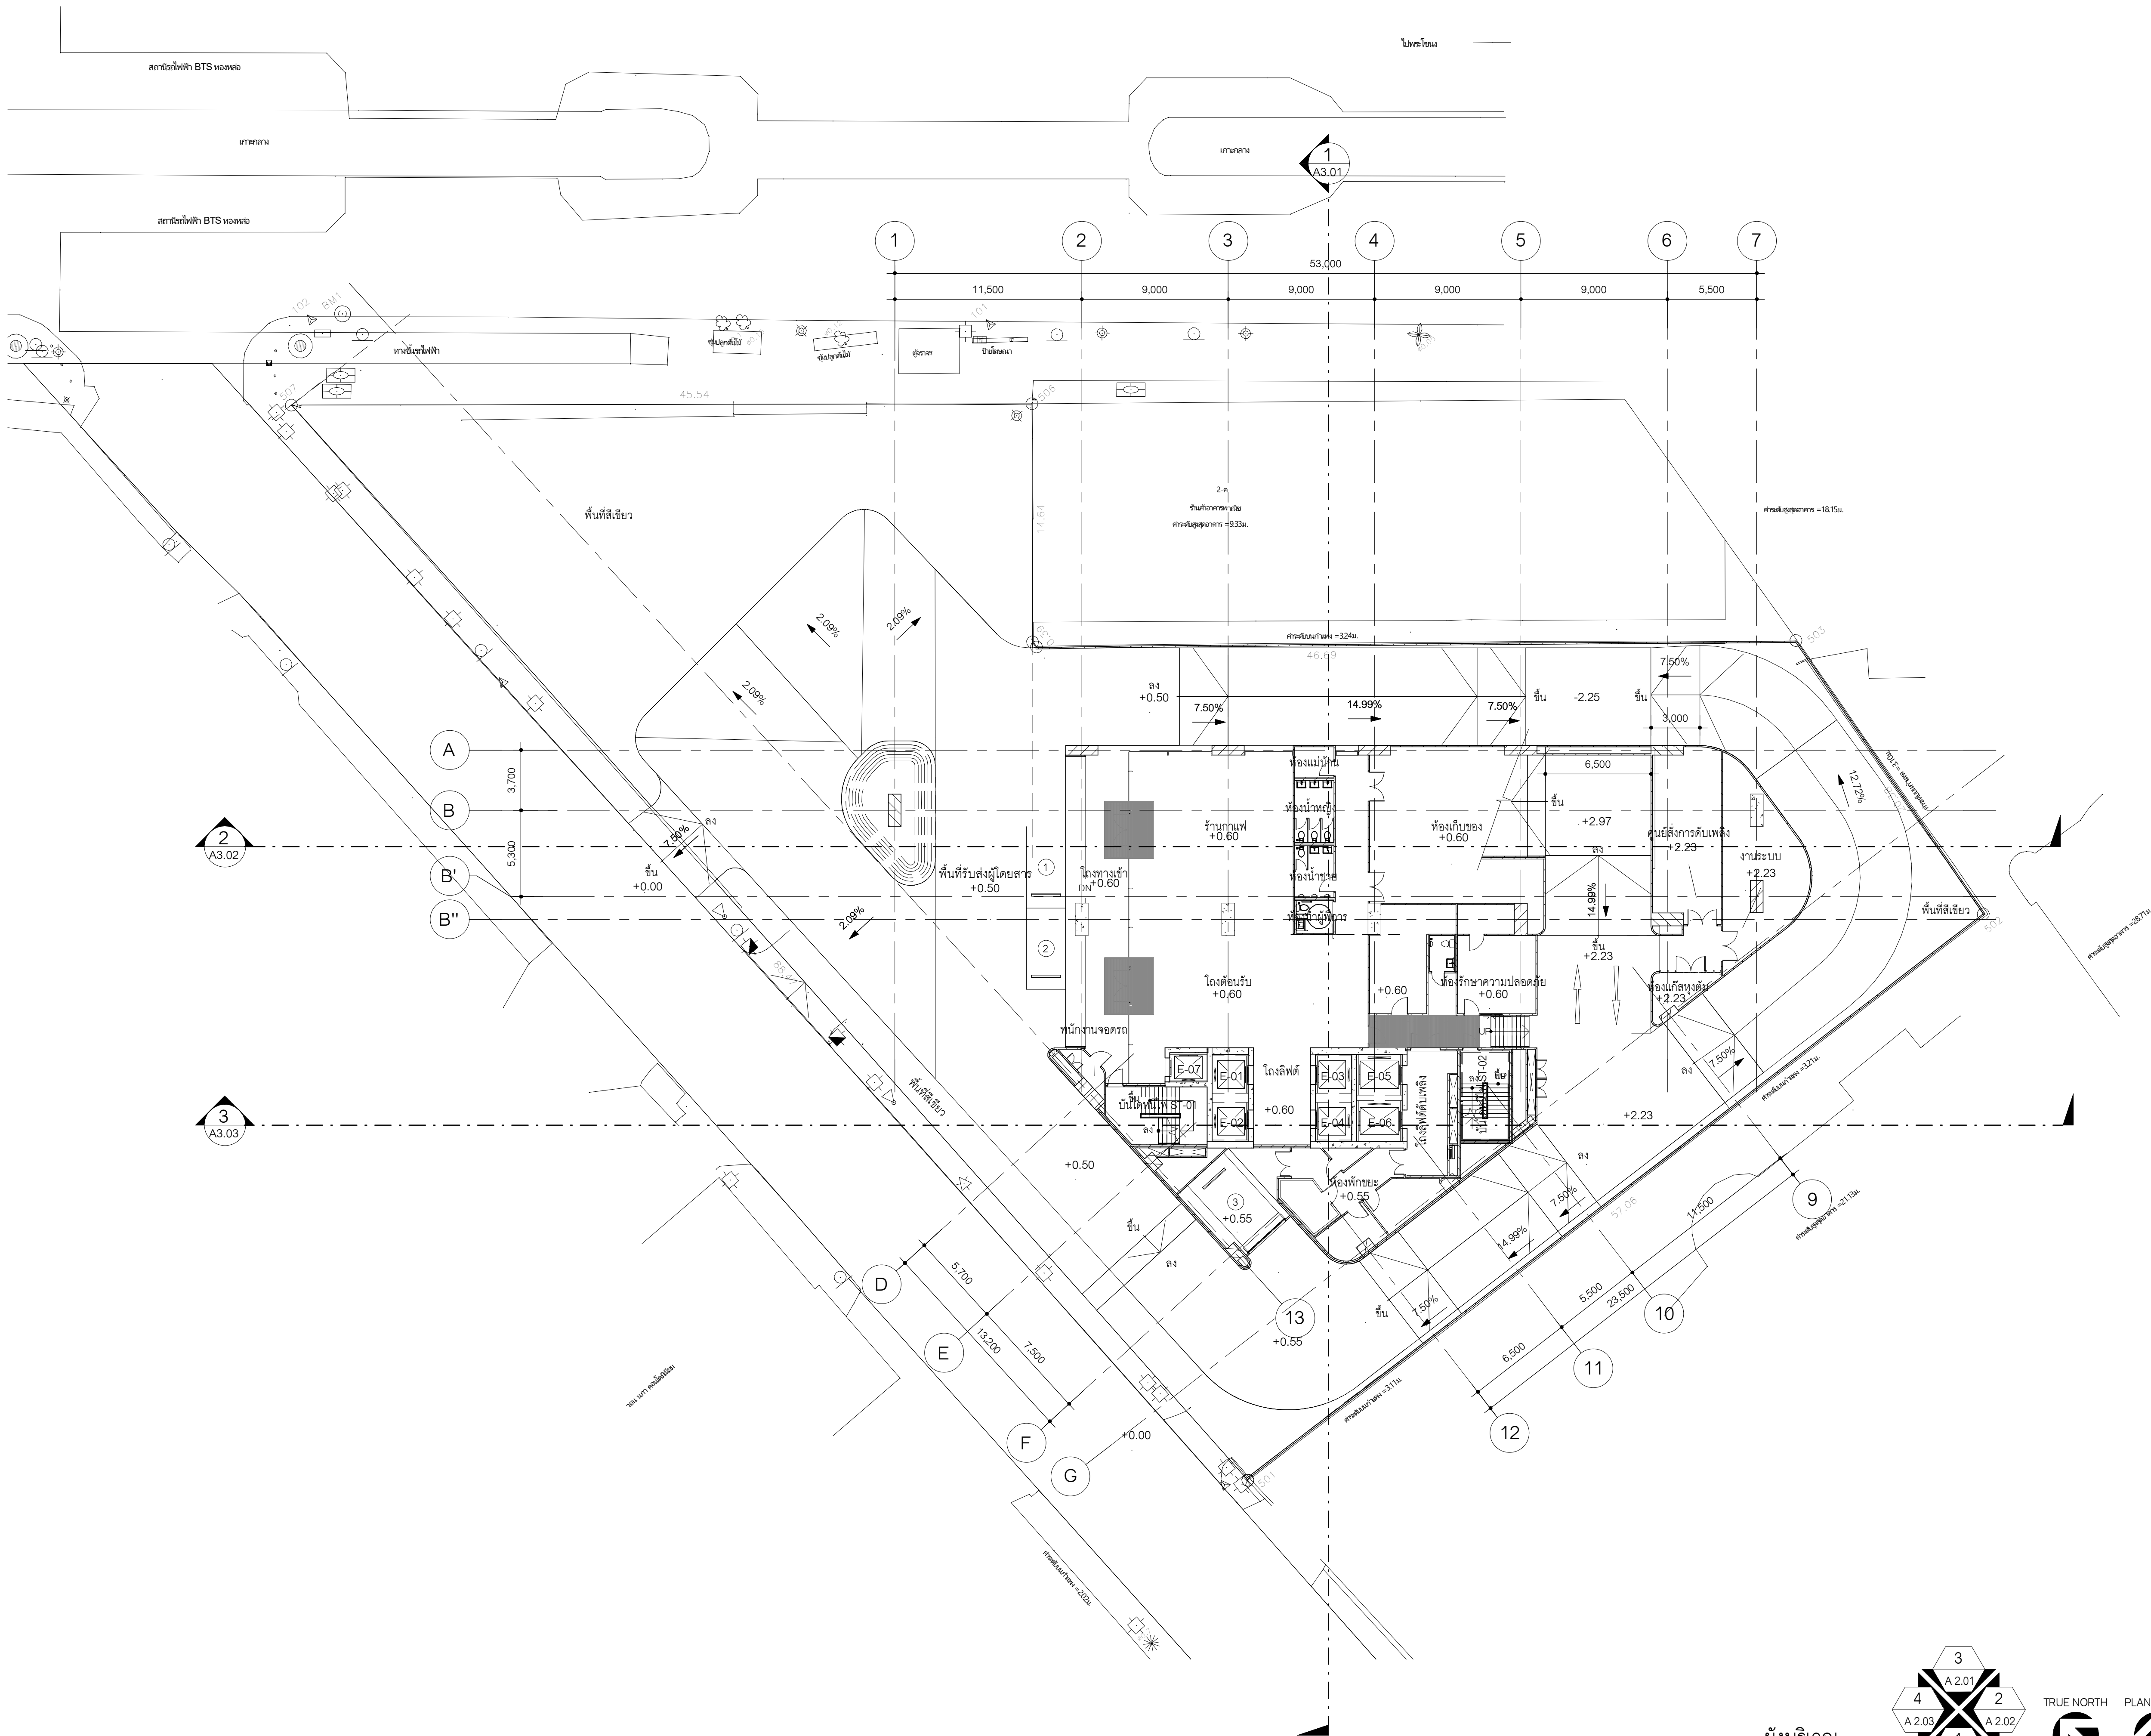

ผังบริเวณ
มาตราส่วน 1 : 200

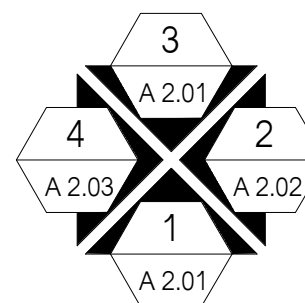

TRUE NORTH
PLAN NORTH

OWNER
LUXURY HOTEL DEVELOPMENT
SUKHUMVIT 38 CO., LTD.

DESIGNER
ARCHITECTS 49 LIMITED
81 SUKHUMVIT 26
BANGKOK 10110 THAILAND
T + 66 (0) 2260 4370
F + 66 (0) 2259 3872
E A49@A49.CO.TH
W A49.CO.TH

A 49

K.C.S. & ASSOCIATES CO. LTD.
22ND FLOOR, CHARN ISSARA TOWER II
2592/267 NEW PETCHABURI ROAD, BANGKAPI,
HUAY KWANG, BANGKOK 10310 THAILAND
T +66 (0) 2308 2481 5
F +66 (0) 2308 2485

KCS
K.C.S. & ASSOCIATES CO. LTD.

MEC PRO DESIGN CO. LTD.
567 BUILDING 4TH FLOOR 1X SOI 51
SUAN LUANG, BANGKOK 10250 THAILAND
T +66 (0) 2170 8029
F (622) 238 3388
E INFO@PLANDSCAPE.COM
W WWW.PLANDSCAPE.COM

MEC PRO
DESIGN

P.LANDSCAPE CO. LTD.
59/3 SUKHUMVIT 39, KLONGTON NUA,
WATTANA, BANGKOK 10110 THAILAND
T (622) 261 3700 TO 9
F (622) 238 3388
E INFO@PLANDSCAPE.COM
W WWW.PLANDSCAPE.COM

pla

ARCHITECTS
ที่ปรึกษา วรวิทย์วรรณ วรณ.509
นางสาววิทย์ อธิวิเศษ วรณ.720
นายวิเศษ อธิวิเศษ วรณ.769
นายวิเศษ อธิวิเศษ วรณ.3432
นายวิเศษ อธิวิเศษ วรณ.3347
นายวิเศษ อธิวิเศษ วรณ.20910
นายวิเศษ อธิวิเศษ วรณ.23830
นายวิเศษ อธิวิเศษ วรณ.27171

SIGNED

STRUCTURAL ENGINEER
นายวิเศษ อธิวิเศษ วรณ.1023
นายวิเศษ อธิวิเศษ วรณ.9572
นายวิเศษ อธิวิเศษ วรณ.15169
นายวิเศษ อธิวิเศษ วรณ.69140

SIGNED

ELECTRICAL ENGINEER
นายวิเศษ อธิวิเศษ วรณ.1118
นายวิเศษ อธิวิเศษ วรณ.1188
นายวิเศษ อธิวิเศษ วรณ.63548

SIGNED

MECHANICAL ENGINEER
นายวิเศษ อธิวิเศษ วรณ.3566
นายวิเศษ อธิวิเศษ วรณ.51088
นายวิเศษ อธิวิเศษ วรณ.52030

SIGNED

ENVIRONMENTAL ENGINEER
นายวิเศษ อธิวิเศษ วรณ.625
นายวิเศษ อธิวิเศษ วรณ.112
นายวิเศษ อธิวิเศษ วรณ.7507

SIGNED

SANITARY ENGINEER
นายวิเศษ อธิวิเศษ วรณ.1118
นายวิเศษ อธิวิเศษ วรณ.1188
นายวิเศษ อธิวิเศษ วรณ.63548

SIGNED

LANDSCAPE ARCHITECT
นายวิเศษ อธิวิเศษ วรณ.108

SIGNED

GENERAL NOTE
1. THIS DRAWING IS THE PROPERTY OF ARCHITECTS 49 LIMITED OR
ONE OF ITS AFFILIATES. IT IS ISSUED SUBJECT TO RETURN UPON
DEMAND AND IS NOT TO BE USED EXCEPT IN CONNECTION WITH THE
PROJECT FOR WHICH IT IS INTENDED.
2. DO NOT SCALE THIS DRAWING. USE FIGURED DIMENSIONS ONLY.
3. ไม่ให้ใช้คำตัดสินที่เกินกว่าที่กำหนดไว้ข้างต้น ห้ามคัดลอกแบบ

PROJECT NAME
THE OKURA PRESTIGE
SUKHUMVIT BANGKOK HOTEL
AND SPA

DRAWING TITLE
ผังบริเวณ


ISSUE/REVISION
NO DESCRIPTION BY DATE
1 แก้ไขแบบสถาปัตย์ A49 17/04/2569

CHECK BY DRAWING NO.

ARCHITECT SIGNED
PD
PA
JC

A0.08

DRAWN BY Author SCALE: 1 : 200
PRINTED DATE 17/04/2569 REF. FILE

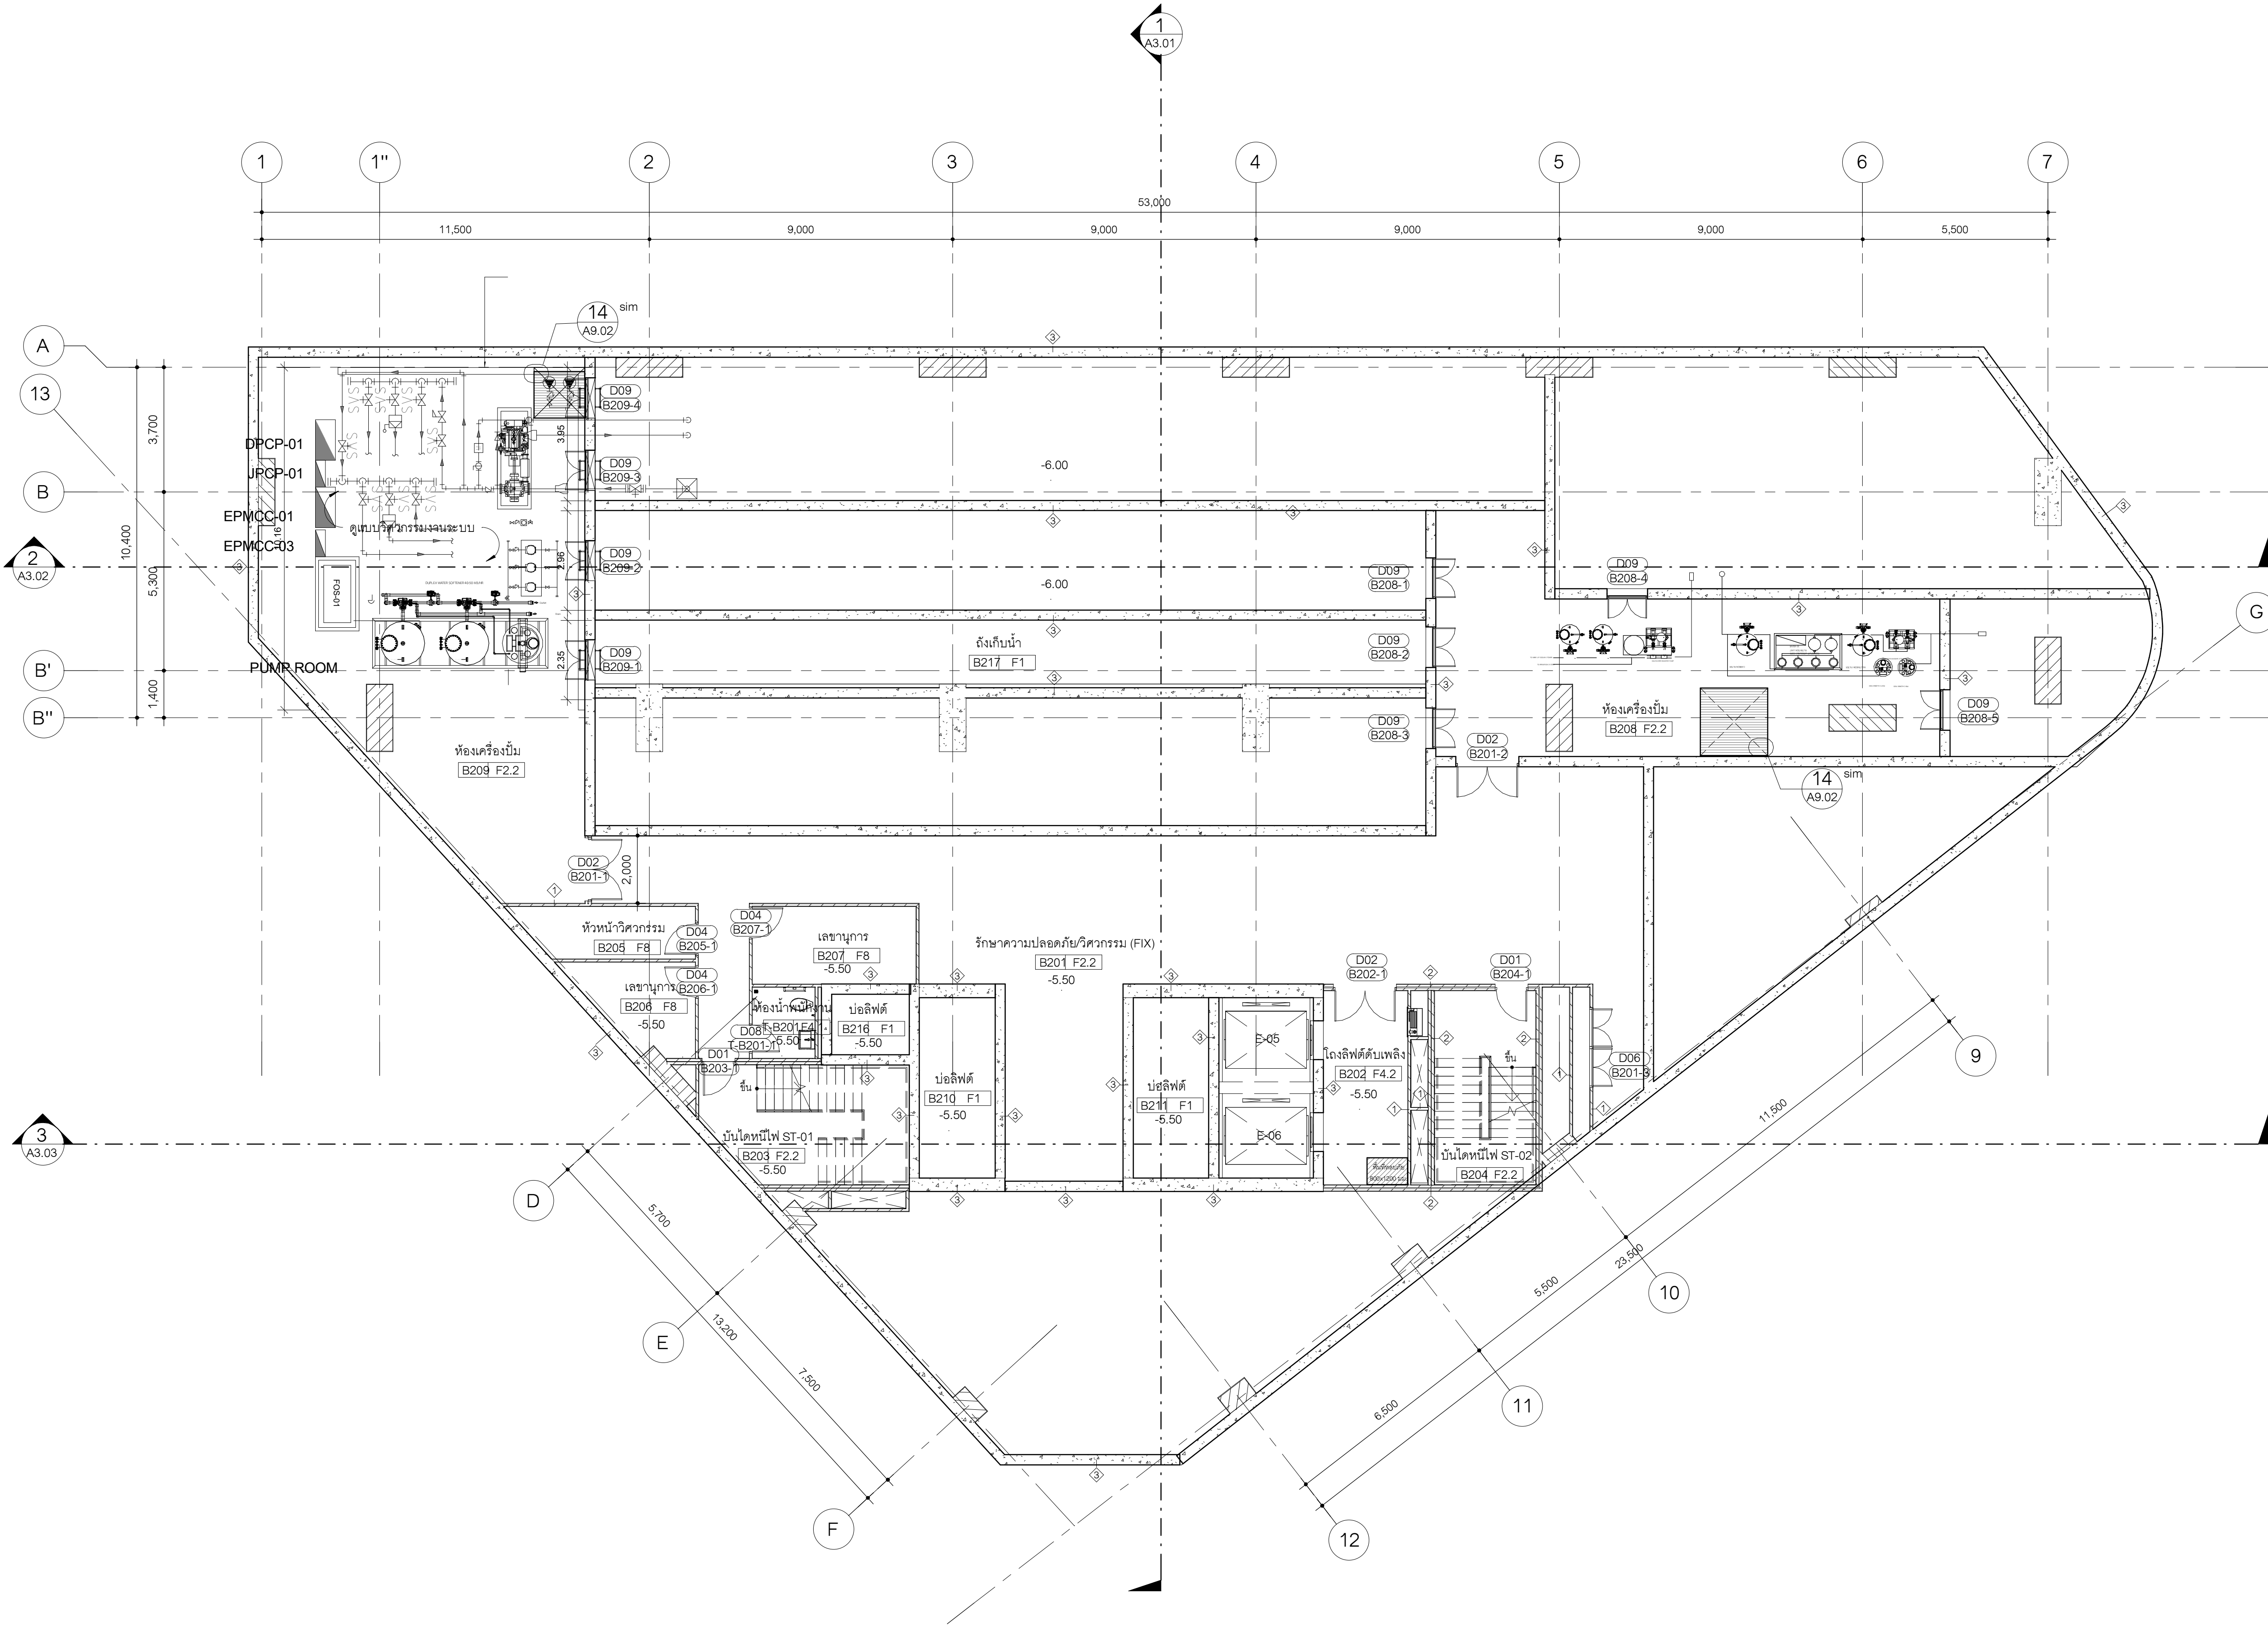

OWNER
LUXURY HOTEL DEVELOPMENT
SUKHUMVIT 38 CO., LTD.

DESIGNER
ARCHITECTS 49 LIMITED
81 SUKHUMVIT 26
BANGKOK 10110 THAILAND
T + 66 (0) 2260 4370
F + 66 (0) 2259 3872
E A49@A49.CO.TH
W A49.CO.TH

K.C.S. & ASSOCIATES CO. LTD.
22ND FLOOR, CHARN ISSARA TOWER II
2522/267 NEW PETCHABURI ROAD, BANGKAPI,
HUAY KWANG, BANGKOK 10310 THAILAND
T +66 (0) 2308 2481 5
F +66 (0) 2308 2485

MEC PRO DESIGN CO. LTD.
567 BUILDING 4TH FLOOR SUKUMVIT 38
SUAN LUANG, BANGKOK 10250 THAILAND
T +66 (0) 2170 8029
F (622) 238 5888
E MECPRO.DESIGN@GMAIL.COM

P.LANDSCAPE CO. LTD.
59/3 SUKHUMVIT 39, KLONGTON NUA,
WATTANA, BANGKOK 10110 THAILAND
T (622) 261 3700 TO 9
F (622) 238 5888
E INFO@PLANDSCAPE.COM
W WWW.PLANDSCAPE.COM

ARCHITECTS
พริษฐ์ วงศ์ไชยวรรณ วสท.509
เนตรศศิษฐ์ อารีมิตร วสท.720
จารุวิมล ธีรพัฒน์ วสท.769
พิชญพร ธีรพัฒน์ วสท.3432
สุภากร ศรีสมบุญ วสท.3347
ปาริชาติ หิชนันท์ วสท.20910
ศรพร ศิริพาน วสท.23830
วันวิมล พูลสวัสดิ์ วสท.27171

STRUCTURAL ENGINEER
การุญ จันทวงศ วสท.1023
กุลธิ จันทวงศ สท.9572
ภาณุ สายรวมญาติ สท.15169
อภิสิทธิ์ สมอียง กย.69140

ELECTRICAL ENGINEER
ชาน นิ่มนง วท.1118
ทนศักดิ์ พิศุทธิ์ สท.1386
ธนวัฒน์ น้อยจ้อย ภาท.63548

MECHANICAL ENGINEER
เบน ไซพงษ์ สท.3566
ณัฏฐา วิเชียรพทยาคม ภา.51088
วิภากร บุญนิยม ภา.52030

ENVIRONMENTAL ENGINEER
ทรงวุฒิ วิเศษศิลป์ สท.625
เบน ไซพงษ์ สท.112
วสุ ละลายบป สท.7507

SANITARY ENGINEER
ชื่อ นามสกุล เลขใบอนุญาต

LANDSCAPE ARCHITECT
นัทธ วรรณศิลป์ สท.108

GENERAL NOTE
1. THIS DRAWING IS THE PROPERTY OF ARCHITECTS 49 LIMITED OR ONE OF ITS AFFILIATES. IT IS ISSUED SUBJECT TO RETURN UPON DEMAND AND IS NOT TO BE USED EXCEPT IN CONNECTION WITH THE PROJECT FOR WHICH IT IS INTENDED.
2. DO NOT SCALE THIS DRAWING. USE FIGURED DIMENSIONS ONLY.
ให้ใช้ค่าเลขที่กำกับไว้เท่านั้น ห้ามวัดจากแบบ

PROJECT NAME
THE OKURA PRESTIGE
SUKHUMVIT BANGKOK HOTEL
AND SPA


DRAWING TITLE
ผังพื้นที่ B2

ISSUE/REVISION
NO DESCRIPTION BY DATE
1 แบบแปลนอาคาร A49 17/04/2569

CHECK BY
ARCHITECT SIGNED
PD
PA
JC
DRAWN BY Author
PRINTED DATE 17/04/2569
SCALE: 1:100
REF. FILE

DRAWING NO.

A1.01

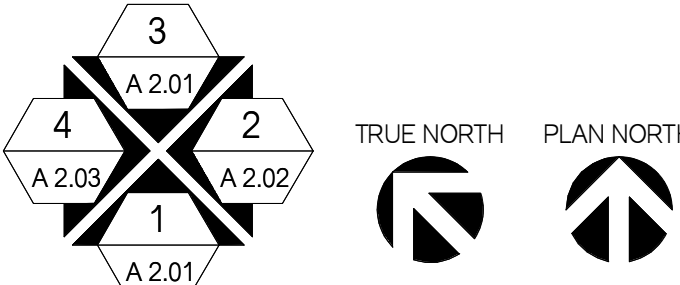

ผังพื้นที่ B2
มาตราส่วน 1:100