



4/18/2026 3:15:02 PM

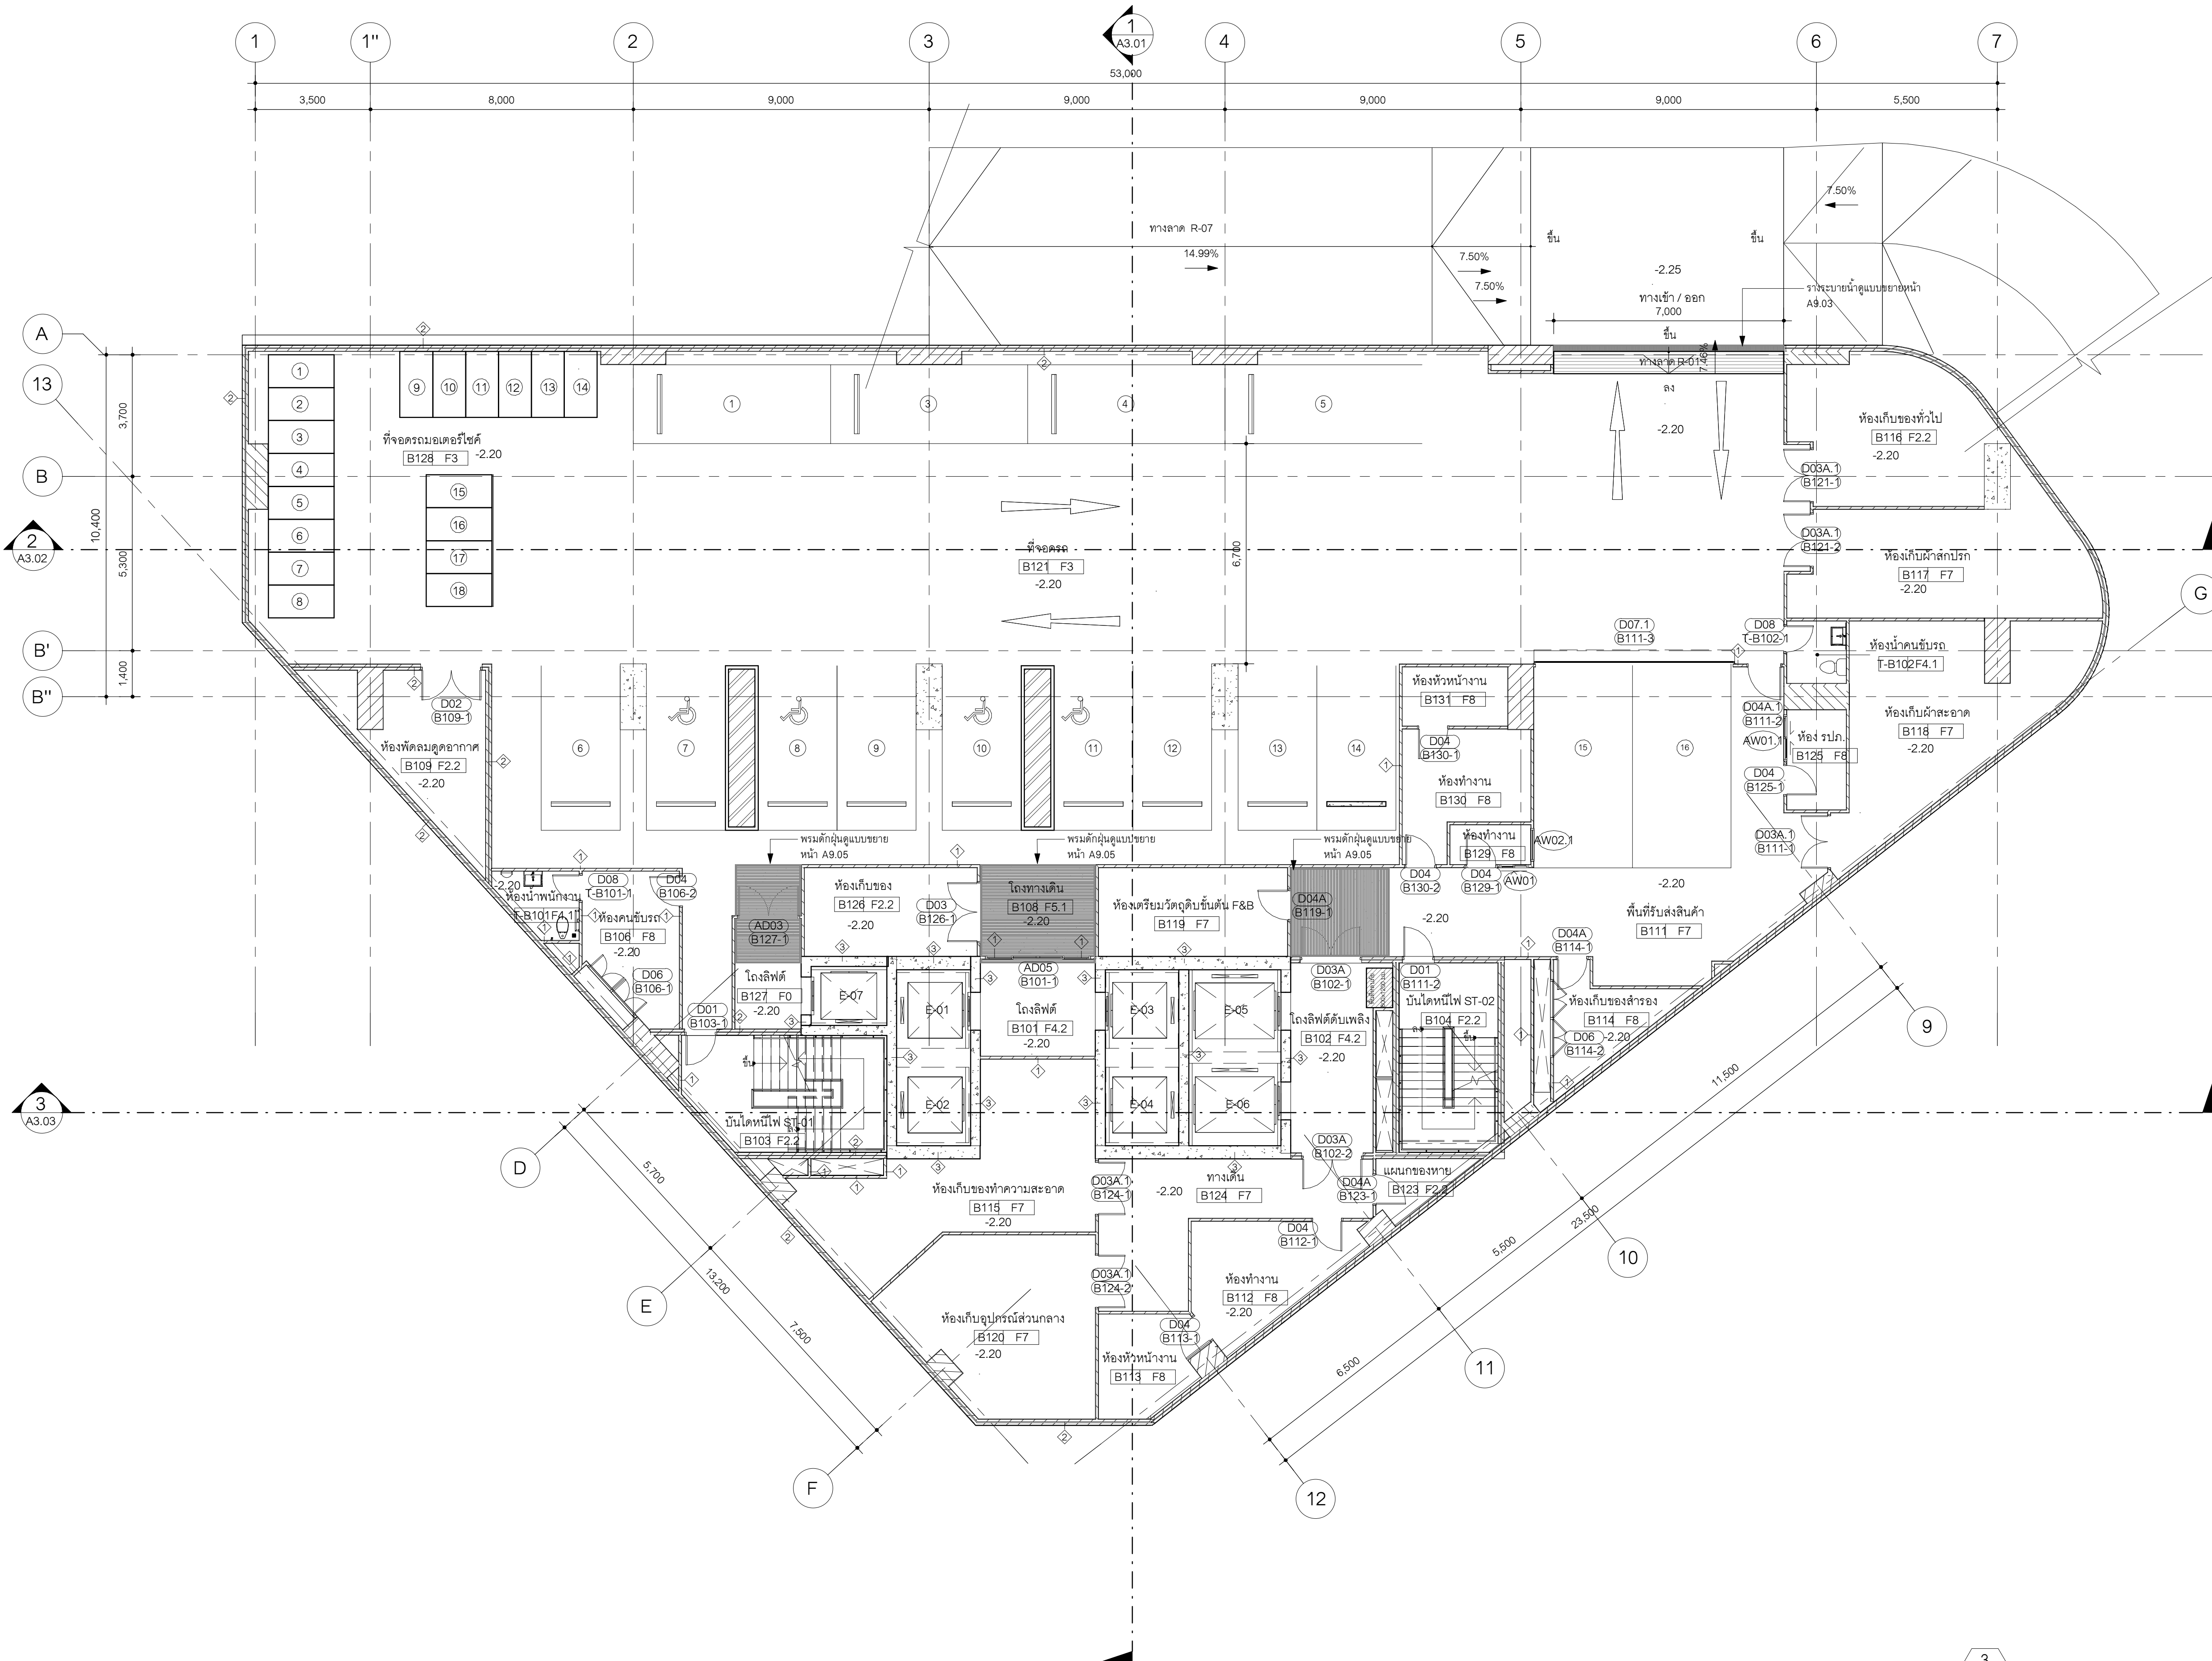

ผังพื้นที่ B1
มาตราส่วน 1:100

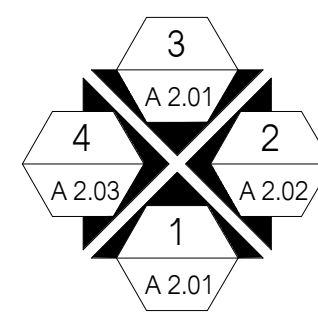

TRUE NORTH
PLAN NORTH

OWNER
LUXURY HOTEL DEVELOPMENT
SUKHUMVIT 38 CO., LTD.

DESIGNER
ARCHITECTS 49 LIMITED
81 SUKHUMVIT 26
BANGKOK 10110 THAILAND
T + 66 (0) 2260 4370
F + 66 (0) 2259 3872
E A49@A49.CO.TH
W A49.CO.TH

K.C.S. & ASSOCIATES CO. LTD.
22ND FLOOR, CHARN ISSARA TOWER II
2502/267 NEW PETCHABURI ROAD, BANGKAPI,
HUAY KWANG, BANGKOK 10310 THAILAND
T +66 (0) 2308 2481 5
F +66 (0) 2308 2485

MEC PRO DESIGN CO. LTD.
567 BUILDING 4TH FLOOR, SUKUMVIT 38
SUAN LUANG, BANGKOK 10250 THAILAND
T +66 (0) 2170 8029
F +66 (0) 2170 8029
E MECPRO.DESIGN@GMAIL.COM

P.LANDSCAPE CO. LTD.
59/3 SUKHUMVIT 39, KLONGTON NUA,
WATTANA, BANGKOK 10110 THAILAND
T (622) 261 3700 TO 9
F (622) 258 3388
E INFO@PLANDSCAPE.COM
W WWW.PLANDSCAPE.COM

ARCHITECTS
ที่ปรึกษา วรวิทย์วรรณ วรณ.509
นางศศิวิทย์ อธิวิธิต วรณ.720
นางสาวจิราพร อธิวิธิต วรณ.769
นางสาวอริยาพร อธิวิธิต วรณ.3432
นางสาวศศิวิทย์ อธิวิธิต วรณ.3347
นางสาวอริยาพร อธิวิธิต วรณ.20910
นางสาวศศิวิทย์ อธิวิธิต วรณ.23830
นางสาวอริยาพร อธิวิธิต วรณ.27171

STRUCTURAL ENGINEER
นายวิชาญ จันทวงศ์ วรณ.1023
นายวิชาญ จันทวงศ์ วรณ.9572
นายวิชาญ จันทวงศ์ วรณ.15169
นายวิชาญ จันทวงศ์ วรณ.69140

ELECTRICAL ENGINEER
นายวิชาญ จันทวงศ์ วรณ.1118
นายวิชาญ จันทวงศ์ วรณ.1188
นายวิชาญ จันทวงศ์ วรณ.63548

MECHANICAL ENGINEER
นายวิชาญ จันทวงศ์ วรณ.3566
นายวิชาญ จันทวงศ์ วรณ.51088
นายวิชาญ จันทวงศ์ วรณ.52030

ENVIRONMENTAL ENGINEER
นางวิชาญ จันทวงศ์ วรณ.625
นายวิชาญ จันทวงศ์ วรณ.112
นายวิชาญ จันทวงศ์ วรณ.7507

SANITARY ENGINEER
นายวิชาญ จันทวงศ์ วรณ.1118
นายวิชาญ จันทวงศ์ วรณ.1188
นายวิชาญ จันทวงศ์ วรณ.63548

LANDSCAPE ARCHITECT
นายวิชาญ จันทวงศ์ วรณ.108

GENERAL NOTE
1. THIS DRAWING IS THE PROPERTY OF ARCHITECTS 49 LIMITED OR ONE OF ITS AFFILIATES. IT IS ISSUED SUBJECT TO RETURN UPON DEMAND AND IS NOT TO BE USED EXCEPT IN CONNECTION WITH THE PROJECT FOR WHICH IT IS INTENDED.
2. DO NOT SCALE THIS DRAWING. USE FIGURED DIMENSIONS ONLY.
ให้ใช้ค่าตัวเลขที่กำหนดไว้เท่านั้น ห้ามวัดจากแบบ

PROJECT NAME
THE OKURA PRESTIGE
SUKHUMVIT BANGKOK HOTEL
AND SPA

DRAWING TITLE
ผังพื้นที่ B1

ISSUE/REVISION
NO DESCRIPTION BY DATE
1 แก้ไขแบบสถาปัตย์ A49 17/04/2569


CHECK BY **DRAWING NO.**

ARCHITECT SIGNED
PD
PA
JC

DRAWN BY Author SCALE: 1:100
PRINTED DATE 17/04/2569 REF. FILE

A1.02

4/18/2026 3:15:07 PM

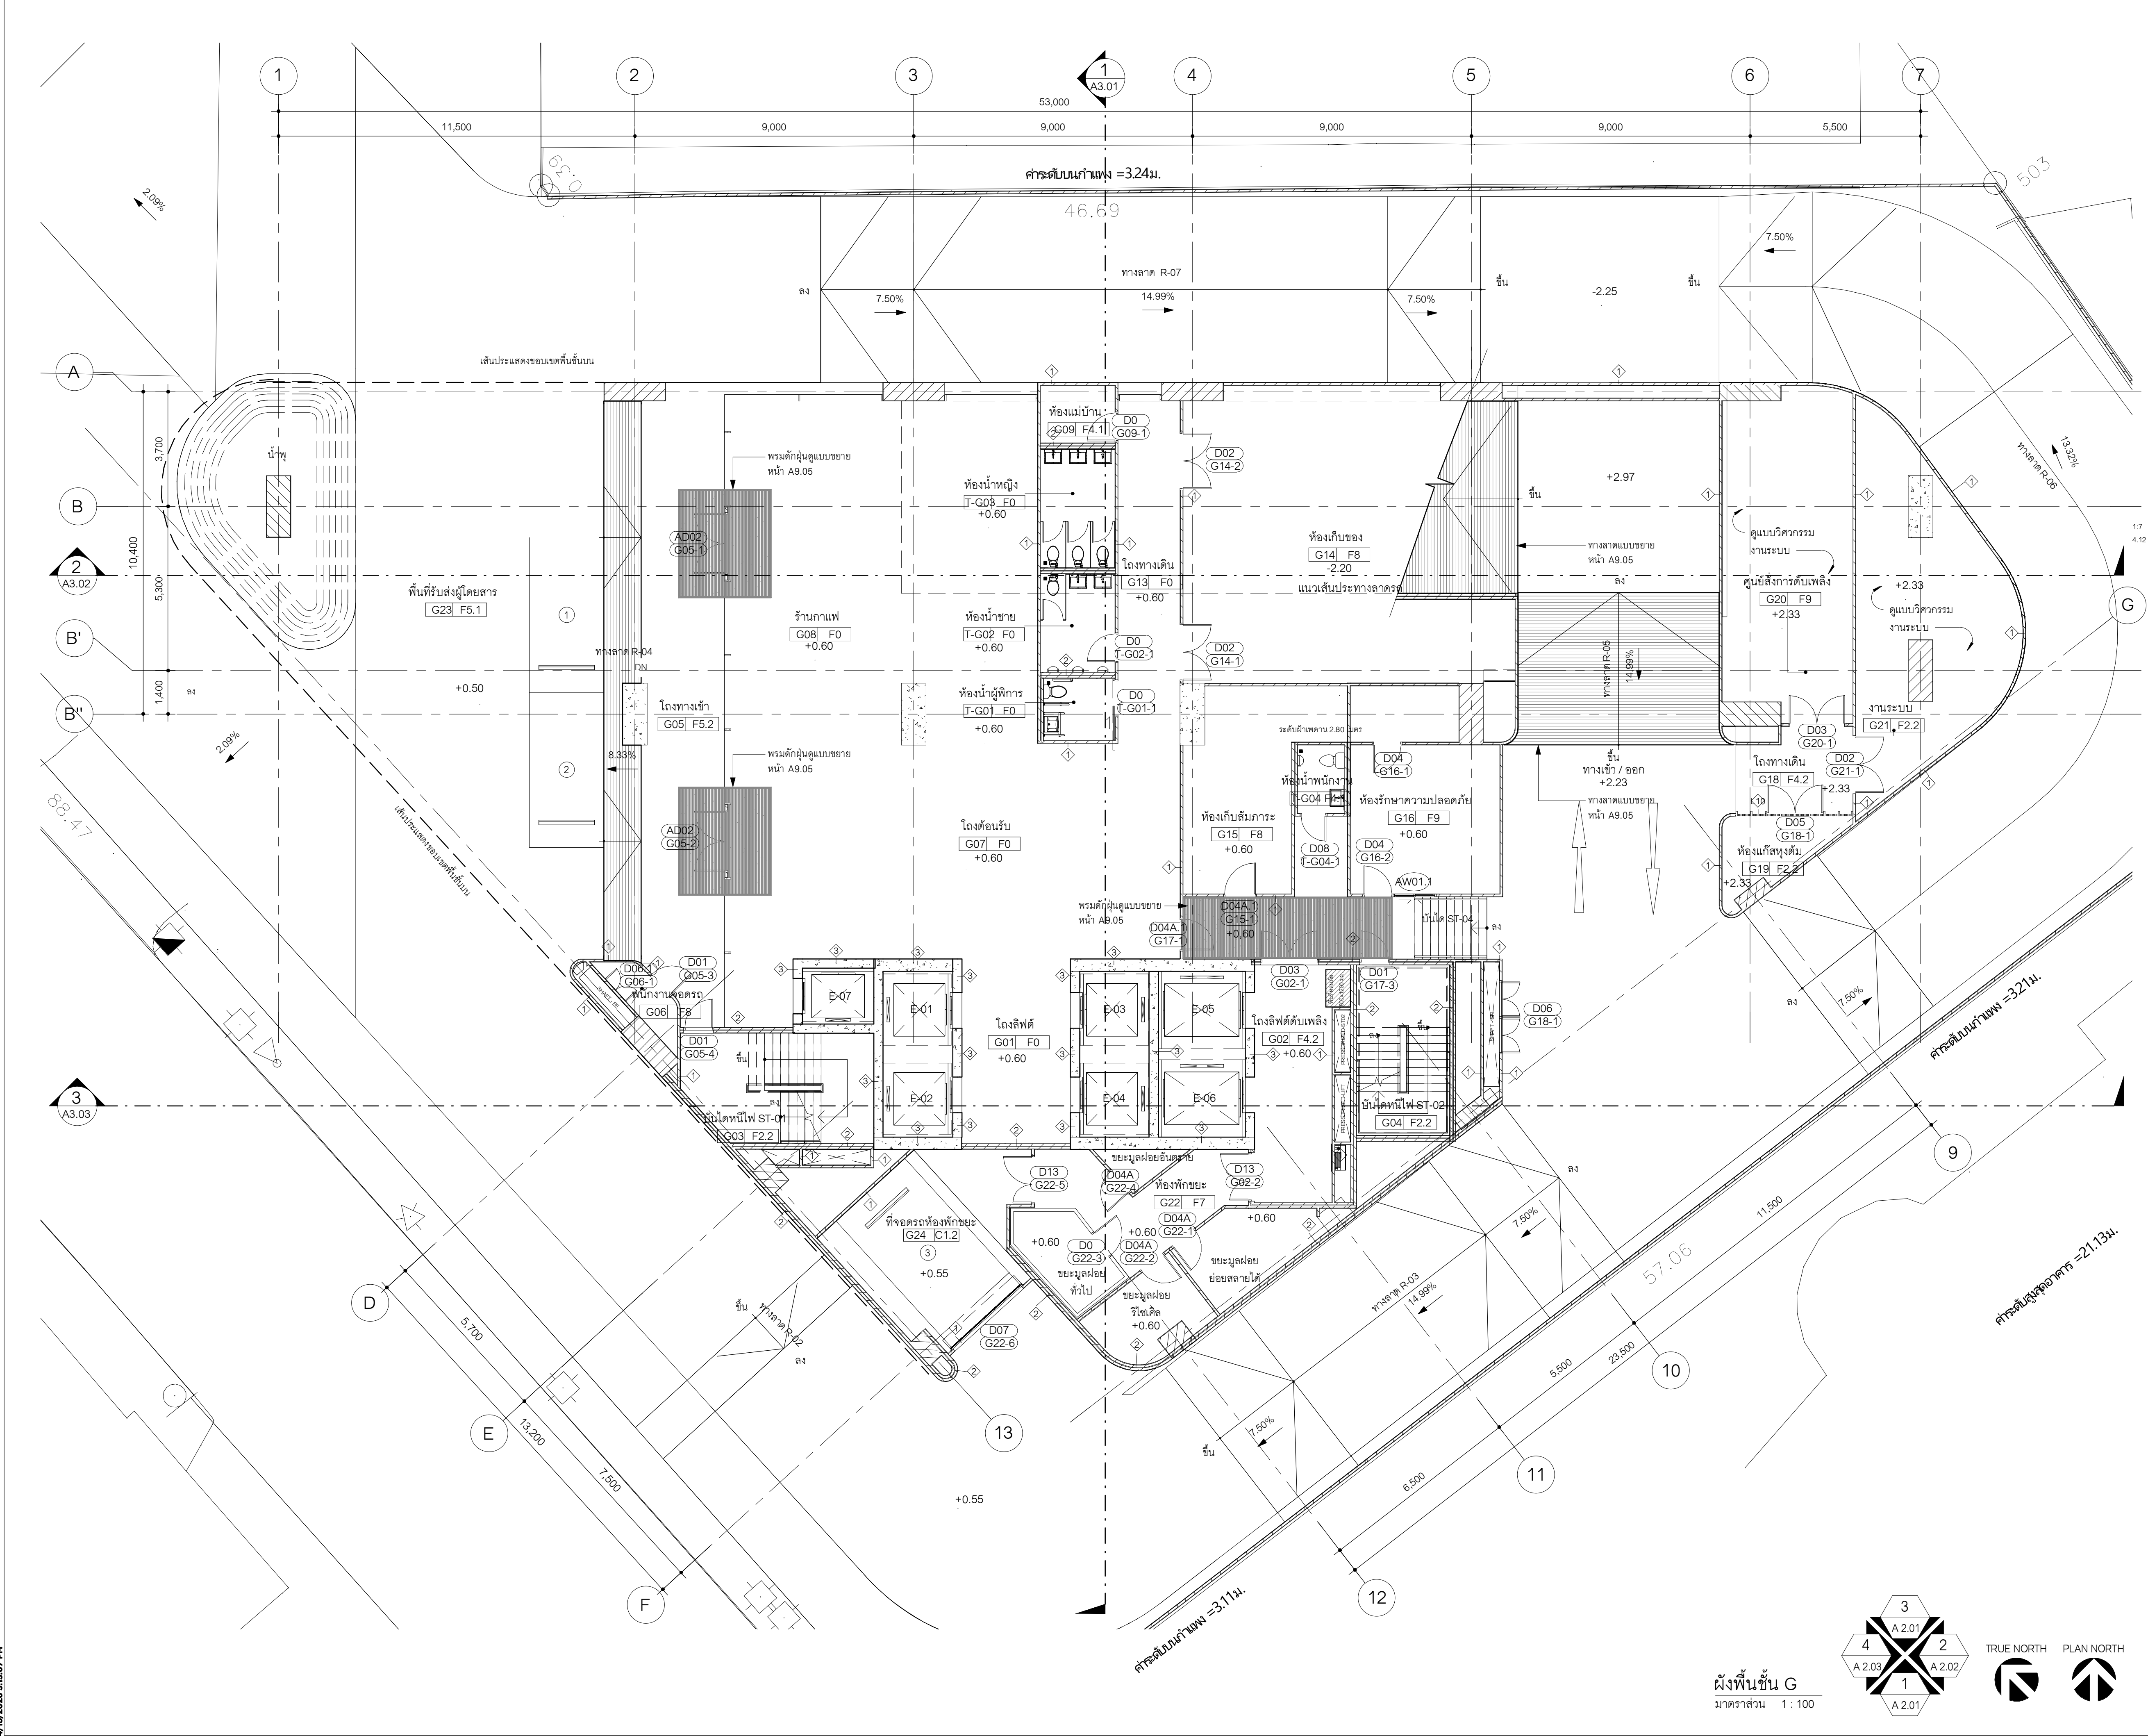

OWNER
LUXURY HOTEL DEVELOPMENT
SUKHUMVIT 38 CO., LTD.

DESIGNER
ARCHITECTS 49 LIMITED
81 SUKHUMVIT 26
BANGKOK 10110 THAILAND
T + 66 (0) 2260 4370
F + 66 (0) 2259 3872
E A49@A49.CO.TH
W A49.CO.TH

K.C.S. & ASSOCIATES CO. LTD.
22ND FLOOR, CHARN ISSARA TOWER II
2522/267 NEW PETCHABURI ROAD, BANGKAPI,
HUAY KWANG, BANGKOK 10310 THAILAND
T + 66 (0) 2308 2481 5
F + 66 (0) 2308 2485

MEC PRO DESIGN CO. LTD.
567 BUILDING 4TH FLOOR, SUKUMVIT 38
SUAN LUANG, BANGKOK 10250 THAILAND
T + 66 (0) 2170 8029
F + 66 (0) 37 034 8917
E MECPRO.DESIGN@GMAIL.COM

P.LANDSCAPE CO. LTD.
59/3 SUKHUMVIT 39, KLONGTON NUA,
WATTANA, BANGKOK 10110 THAILAND
T (622) 261 3700 TO 9
F (622) 238 3388
E INFO@PLANDSCAPE.COM
W WWW.PLANDSCAPE.COM

ARCHITECTS
ที่ปรึกษา: วรวิทย์วรรณ วรณ.509
เนรมิตวิทย์ อธิวิตร วรณ.720
จารุวิมล อธิวิตร วรณ.769
พินิจพร อธิวิตร วรณ.3432
สุภากร ศรีสมบุญ วรณ.3347
ปรีดีศ หิมนันท์ วรณ.20910
ศรพร ศิริพนธ์ วรณ.23830
วันธนา พูลสวัสดิ์ วรณ.27171

STRUCTURAL ENGINEER
การยู่: จันทราวุธ วรณ.1023
กุลธิกร จันทราวุธ วรณ.9572
ภาณุ สายรวมญาติ วรณ.15169
อภิสิทธิ์ สมอียง วรณ.69140

ELECTRICAL ENGINEER
ชาน: นิติกร วรณ.1118
เนรมิตวิทย์ พินิจพร วรณ.1586
ธนวิวัฒน์ น้อยจ้อย วรณ.63548

MECHANICAL ENGINEER
เนต: ไชยพงษ์ วรณ.3566
ณภัทร วิเชียรพทยาคม วรณ.51088
วิภากร บุญนิยม วรณ.52030

ENVIRONMENTAL ENGINEER
ทรงวุฒิ วิเศษศิลป์ วรณ.625
เนต: ไชยพงษ์ วรณ.112
วสุ ลลลลลลลล วรณ.7507

SANITARY ENGINEER
ชื่อ: นามสกุล เลขใบอนุญาต

LANDSCAPE ARCHITECT
ที่ปรึกษา: รณวิทย์วรรณ วรณ.108

GENERAL NOTE
1. THIS DRAWING IS THE PROPERTY OF ARCHITECTS 49 LIMITED OR ONE OF ITS AFFILIATES. IT IS ISSUED SUBJECT TO RETURN UPON DEMAND AND IS NOT TO BE USED EXCEPT IN CONNECTION WITH THE PROJECT FOR WHICH IT IS INTENDED.
2. DO NOT SCALE THIS DRAWING. USE FIGURED DIMENSIONS ONLY.
ให้ใช้ตัวเลขที่กำหนดไว้เท่านั้น ห้ามวัดจากแบบ

PROJECT NAME
THE OKURA PRESTIGE
SUKHUMVIT BANGKOK HOTEL
AND SPA

DRAWING TITLE
ผังพื้นที่ G


ISSUE/REVISION
NO DESCRIPTION BY DATE
1 แบบแปลนอาคาร A49 17/04/2569


CHECK BY
ARCHITECT SIGNED
PD
PA
JC

DRAWING NO.
A1.04

DRAWN BY: Author SCALE: 1:100
PRINTED DATE: 17/04/2569 REF. FILE

ผังพื้นที่ G
มาตราส่วน 1:100

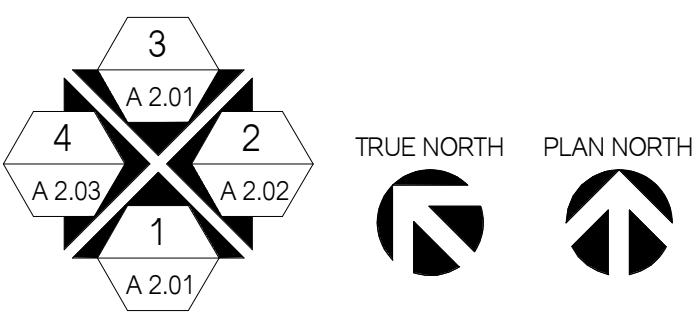

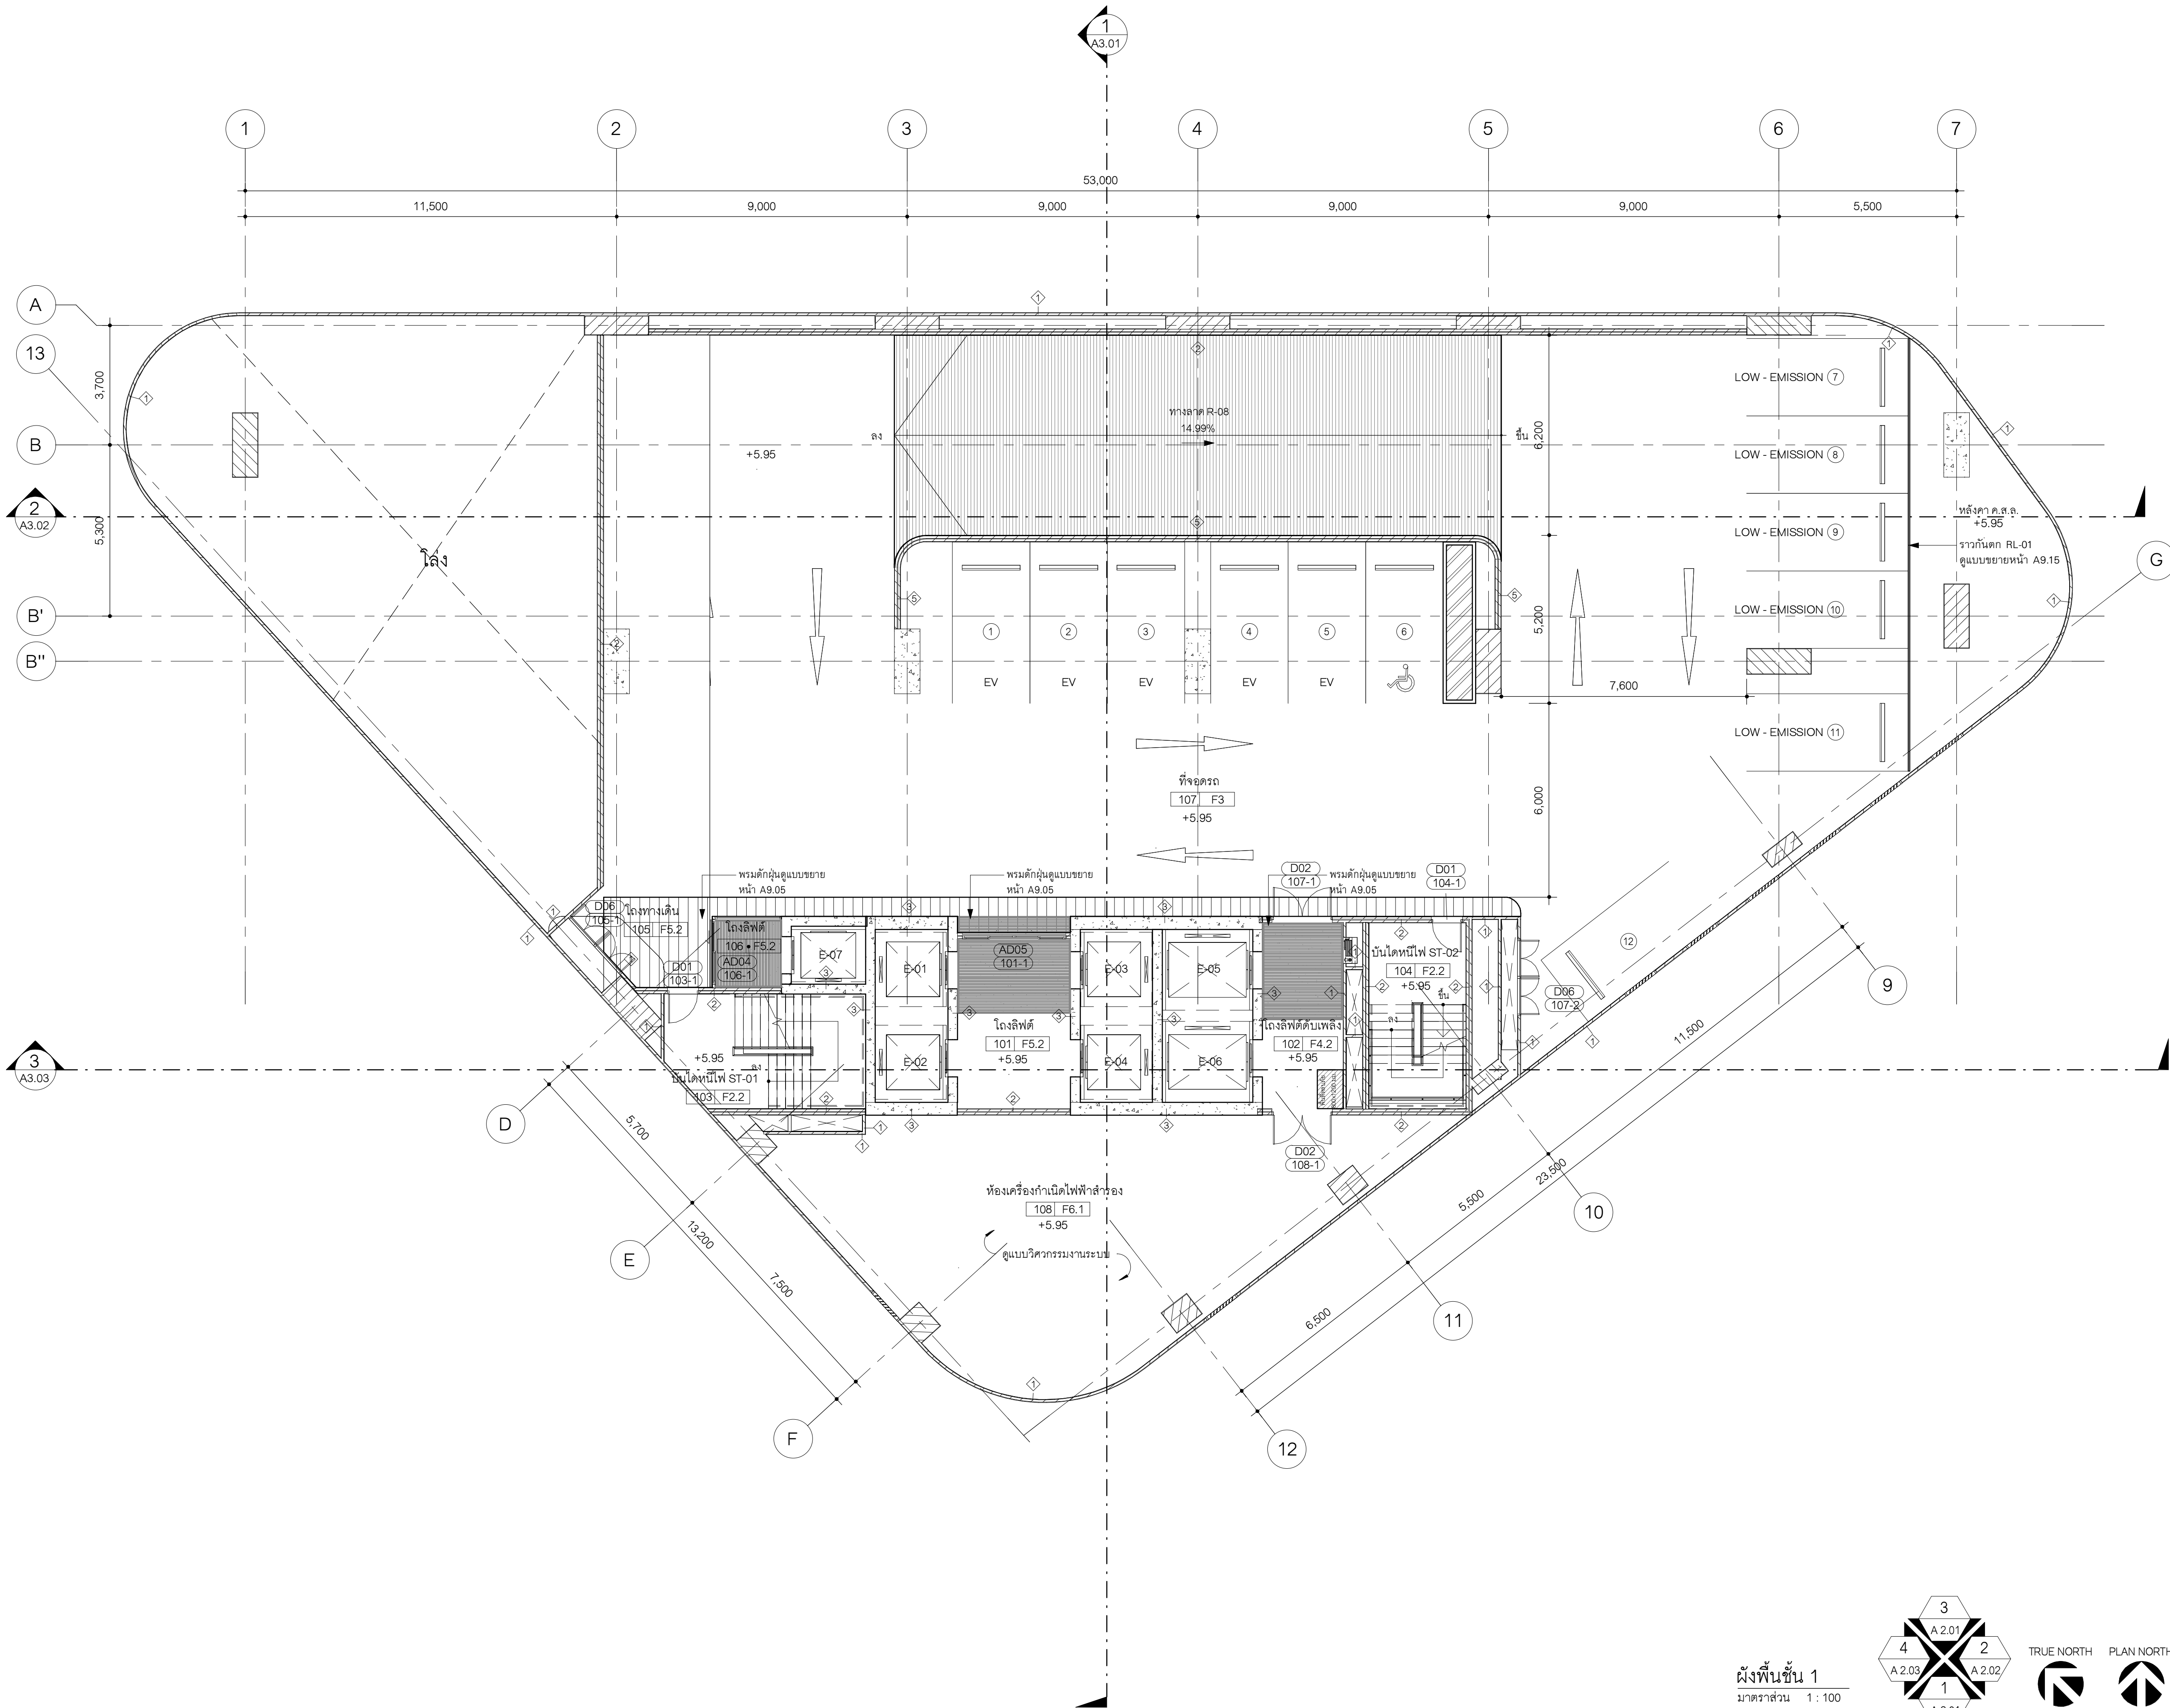

OWNER
LUXURY HOTEL DEVELOPMENT
SUKHUMVIT 38 CO., LTD.

DESIGNER
ARCHITECTS 49 LIMITED
81 SUKHUMVIT 26
BANGKOK 10110 THAILAND
T + 66 (0) 2260 4370
F + 66 (0) 2259 3872
E A49@A49.CO.TH
W A49.CO.TH

K.C.S. & ASSOCIATES CO. LTD.
22ND FLOOR, CHARN ISSARA TOWER II
2522/267 NEW PETCHABURI ROAD, BANGKAPI,
HUAY KWANG, BANGKOK 10310 THAILAND
T +66 (0) 2308 2481 5
F +66 (0) 2308 2485

MEC PRO DESIGN CO. LTD.
567 BUILDING 4TH FLOOR, SUKUMVIT 38
SUAN LUANG, BANGKOK 10250 THAILAND
T +66 (0) 2170 8029
F +66 (0) 37 034 8917
E MECPRO.DESIGN@GMAIL.COM

P.LANDSCAPE CO. LTD.
59/3 SUKHUMVIT 39, KLONGTON NUA,
WATTANA, BANGKOK 10110 THAILAND
T (622) 261 3700 TO 9
F (622) 238 3388
E INFO@PLANDSCAPE.COM
W WWW.PLANDSCAPE.COM

ARCHITECTS
พิธี วงศ์สุวรรณ วส. 509
เนรศักดิ์ อธิวิตร วส. 720
จารุวัฒน์ อธิวิตร วส. 769
พิณพร อธิวิตร วส. 3432
สุภากร ศรีสมบุญ วส. 3347
ปาริชาติ หิมนันโย วส. 20910
ศรพร ศิริพาน วส. 23830
วันรณ พูลสวัสดิ์ วส. 27171

STRUCTURAL ENGINEER
ภาณุ จันทวงษ์ ว. 1023
กุลธิ จันทวงษ์ ส. 9572
ภาณุ สายรวมญาติ ส. 15169
อภิสิทธิ์ สมอ้ง ก. 69140

ELECTRICAL ENGINEER
ชาน นิตย ว. 1118
ทนศักดิ์ พิศุทธิ์ ส. 1586
ธนวัฒน์ น้อยจ้อย ก. 63548

MECHANICAL ENGINEER
เบน ไซพงษ์ ส. 3566
ณภัทร วิเชียรพทยาณ ก. 51086
วิฑรศักดิ์ บุญโคตร ก. 52030

ENVIRONMENTAL ENGINEER
ทรงวุฒิ วิเศษศิลป์ ส. 625
เบน ไซพงษ์ ก. 112
วสุ ละลายน ก. 7507

SANITARY ENGINEER
ช่อ นามสกุล เลขใบอนุญาต

LANDSCAPE ARCHITECT
นัทธ วรรณสินใจ ส. 108

GENERAL NOTE
1. THIS DRAWING IS THE PROPERTY OF ARCHITECTS 49 LIMITED OR ONE OF ITS AFFILIATES. IT IS ISSUED SUBJECT TO RETURN UPON DEMAND AND IS NOT TO BE USED EXCEPT IN CONNECTION WITH THE PROJECT FOR WHICH IT IS INTENDED.
2. DO NOT SCALE THIS DRAWING. USE FIGURED DIMENSIONS ONLY.
ให้ใช้ค่าเลขที่กำกับไว้เท่านั้น ห้ามวัดจากแบบ

PROJECT NAME
THE OKURA PRESTIGE
SUKHUMVIT BANGKOK HOTEL
AND SPA

DRAWING TITLE
ผังพื้นที่ 1


ISSUE/REVISION
NO DESCRIPTION BY DATE
1 แบบแปลนสถาปัตย์ A49 17/04/2569

CHECK BY DRAWING NO.

ARCHITECT SIGNED
PM
PD
PA
JC

DRAWN BY Author SCALE: 1:100
PRINTED DATE 17/04/2569 REF. FILE

ผังพื้นที่ 1
มาตราส่วน 1 : 100

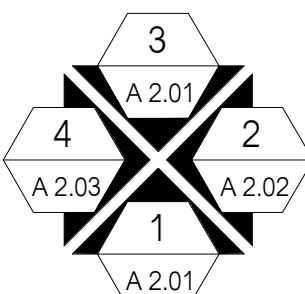

TRUE NORTH PLAN NORTH

A1.05

OWNER
LUXURY HOTEL DEVELOPMENT
SUKHUMVIT 38 CO., LTD.

DESIGNER
ARCHITECTS 49 LIMITED
81 SUKHUMVIT 26
BANGKOK 10110 THAILAND
T + 66 (0) 2260 4370
F + 66 (0) 2259 3872
E A49@A49.CO.TH
W A49.CO.TH

K.C.S. & ASSOCIATES CO. LTD.
22ND FLOOR, CHARN ISSARA TOWER II
2522/267 NEW PETCHABURI ROAD, BANGKAPI,
HUAY KWANG, BAKOK 10310 THAILAND
T +66 (0) 2308 2481 5
F +66 (0) 2308 2485

MEC PRO DESIGN CO. LTD.
567 BUILDING 4TH FLOOR, SUKUMVIT 38
SUAN LUANG, BANGKOK 10250 THAILAND
T +66 (0) 2170 8029
F +66 (0) 37 034 8917
E MECPRO.DESIGN@GMAIL.COM

P.LANDSCAPE CO. LTD.
59/3 SUKHUMVIT 39, KLONGTONG NUA,
WATTANA, BANGKOK 10110 THAILAND
T (622) 261 3700 TO 9
F (622) 238 3388
E INFO@PLANDSCAPE.COM
W WWW.PLANDSCAPE.COM

ARCHITECTS
พิธี วงศ์วิเศษวรรณ วสท.509
เนตรศศิธร อธิวิเศษ วสท.720
จารุวิมล อธิวิเศษ วสท.769
พิณพร อธิวิเศษ วสท.3432
สุภากร ศรีสมบุญ วสท.3347
ปรีดี พิณนโธ วสท.20910
ศรพร ศิริพาน วสท.23830
วริชรา นุสสุวดี วสท.27171

STRUCTURAL ENGINEER
กาญจนา จันทวงศ วสท.1023
กุลธิ จันทวงศ สท.9572
ภาสกร สายรวมญาติ สท.15169
อภิสิทธิ์ สมอียง สท.69140

ELECTRICAL ENGINEER
ชาน นิมิต วสท.1118
พนศักดิ์ พิศุสสา สท.1586
ธนวัฒน์ น้อยจ้อย วกท.63548

MECHANICAL ENGINEER
เบนต ไชยพงษ์ สท.3566
ณภัทร วิเชียรพทยาตม วกท.51088
วิฑรศักดิ์ บุญนิเทศ วกท.52030

ENVIRONMENTAL ENGINEER
ทรงวุฒิ วิเศษศิลป์ สท.625
เบนต ไชยพงษ์ สท.112
วสุ สละยาบป สท.7507

SANITARY ENGINEER
ชื่อ นามสกุล เลขใบอนุญาต

LANDSCAPE ARCHITECT
นัทธกร รณนทีโชจน์ สท.108

GENERAL NOTE
1. THIS DRAWING IS THE PROPERTY OF ARCHITECTS 49 LIMITED OR ONE OF ITS AFFILIATES. IT IS ISSUED SUBJECT TO RETURN UPON DEMAND AND IS NOT TO BE USED EXCEPT IN CONNECTION WITH THE PROJECT FOR WHICH IT IS INTENDED.
2. DO NOT SCALE THIS DRAWING. USE FIGURED DIMENSIONS ONLY.
โปรดใช้ค่าตัวเลขที่กำหนดไว้เท่านั้น ห้ามวัดจากแบบ

PROJECT NAME
THE OKURA PRESTIGE
SUKHUMVIT BANGKOK HOTEL
AND SPA


DRAWING TITLE
ผังพื้นที่ 1A

ISSUE/REVISION
NO DESCRIPTION BY DATE
1 แก้ไขแบบสถาปัตย์ A49 17/04/2569



CHECK BY DRAWING NO.


ARCHITECT SIGNED
PM
PD
PA
JC

DRAWN BY Author SCALE: 1:100
PRINTED DATE 17/04/2569 REF. FILE

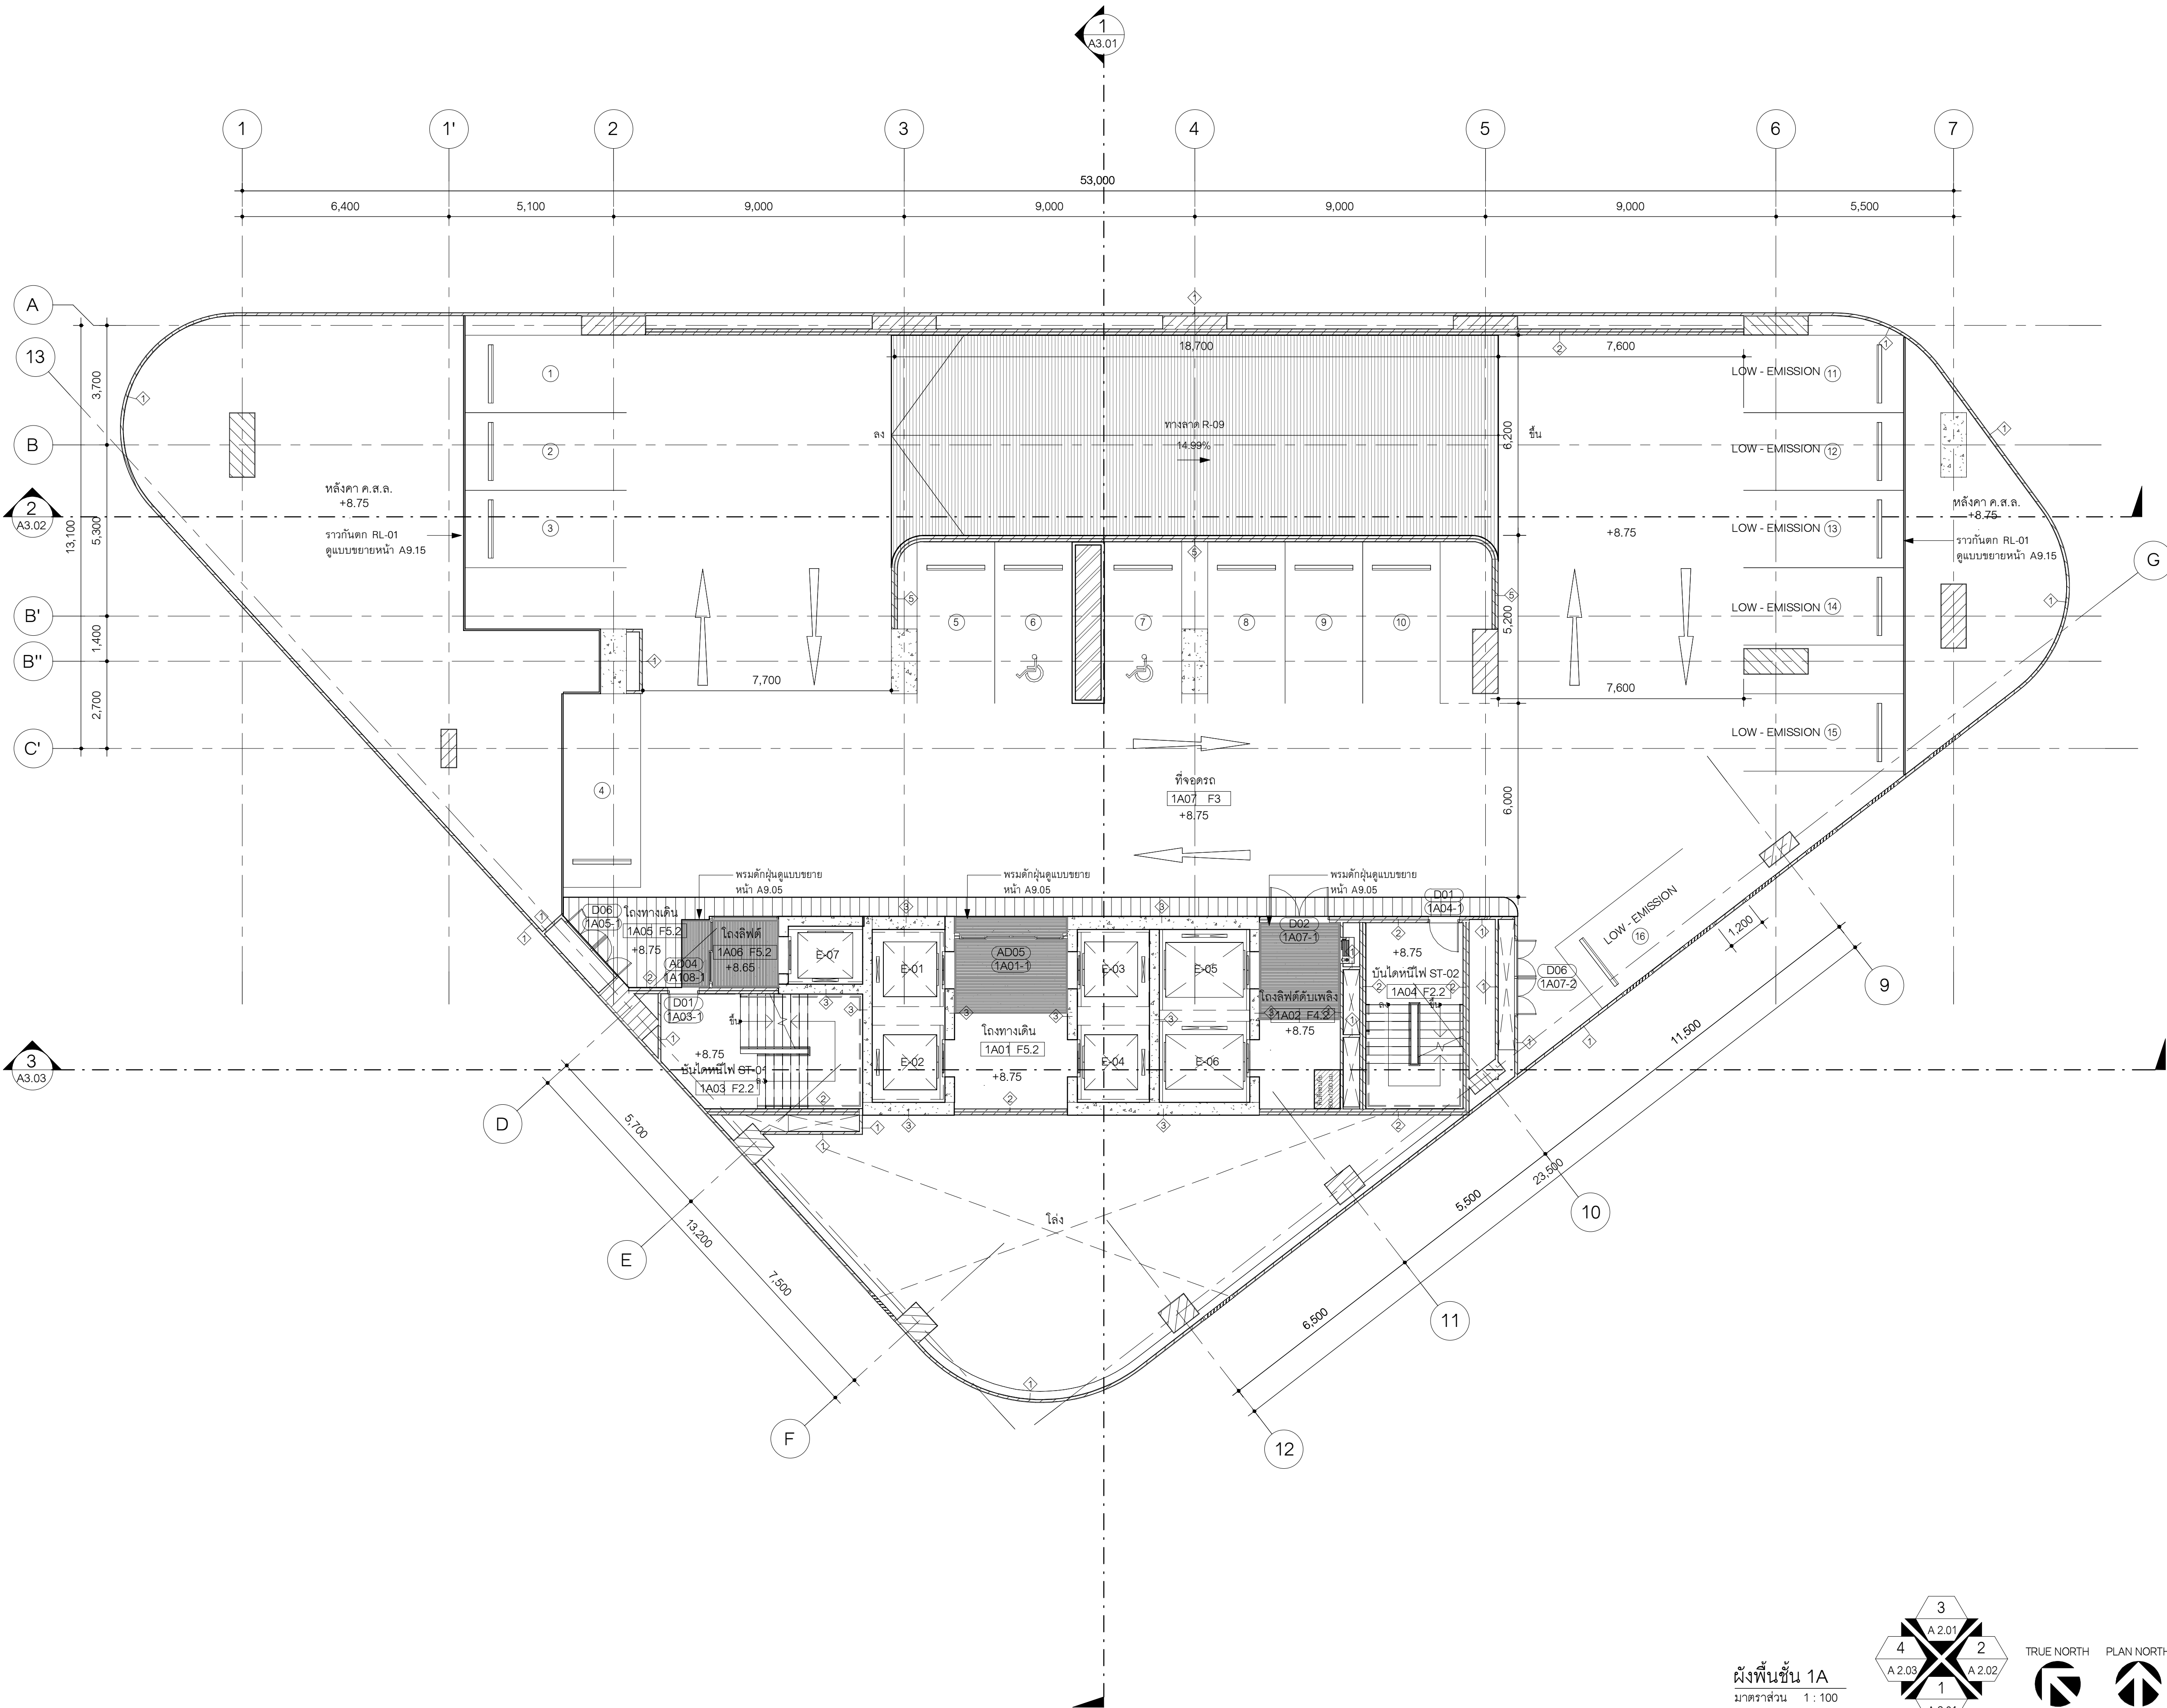

ผังพื้นที่ 1A
มาตราส่วน 1 : 100

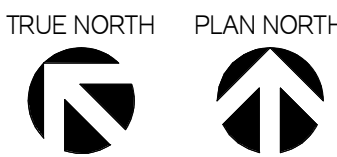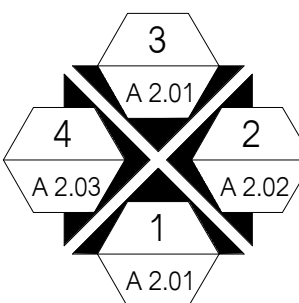

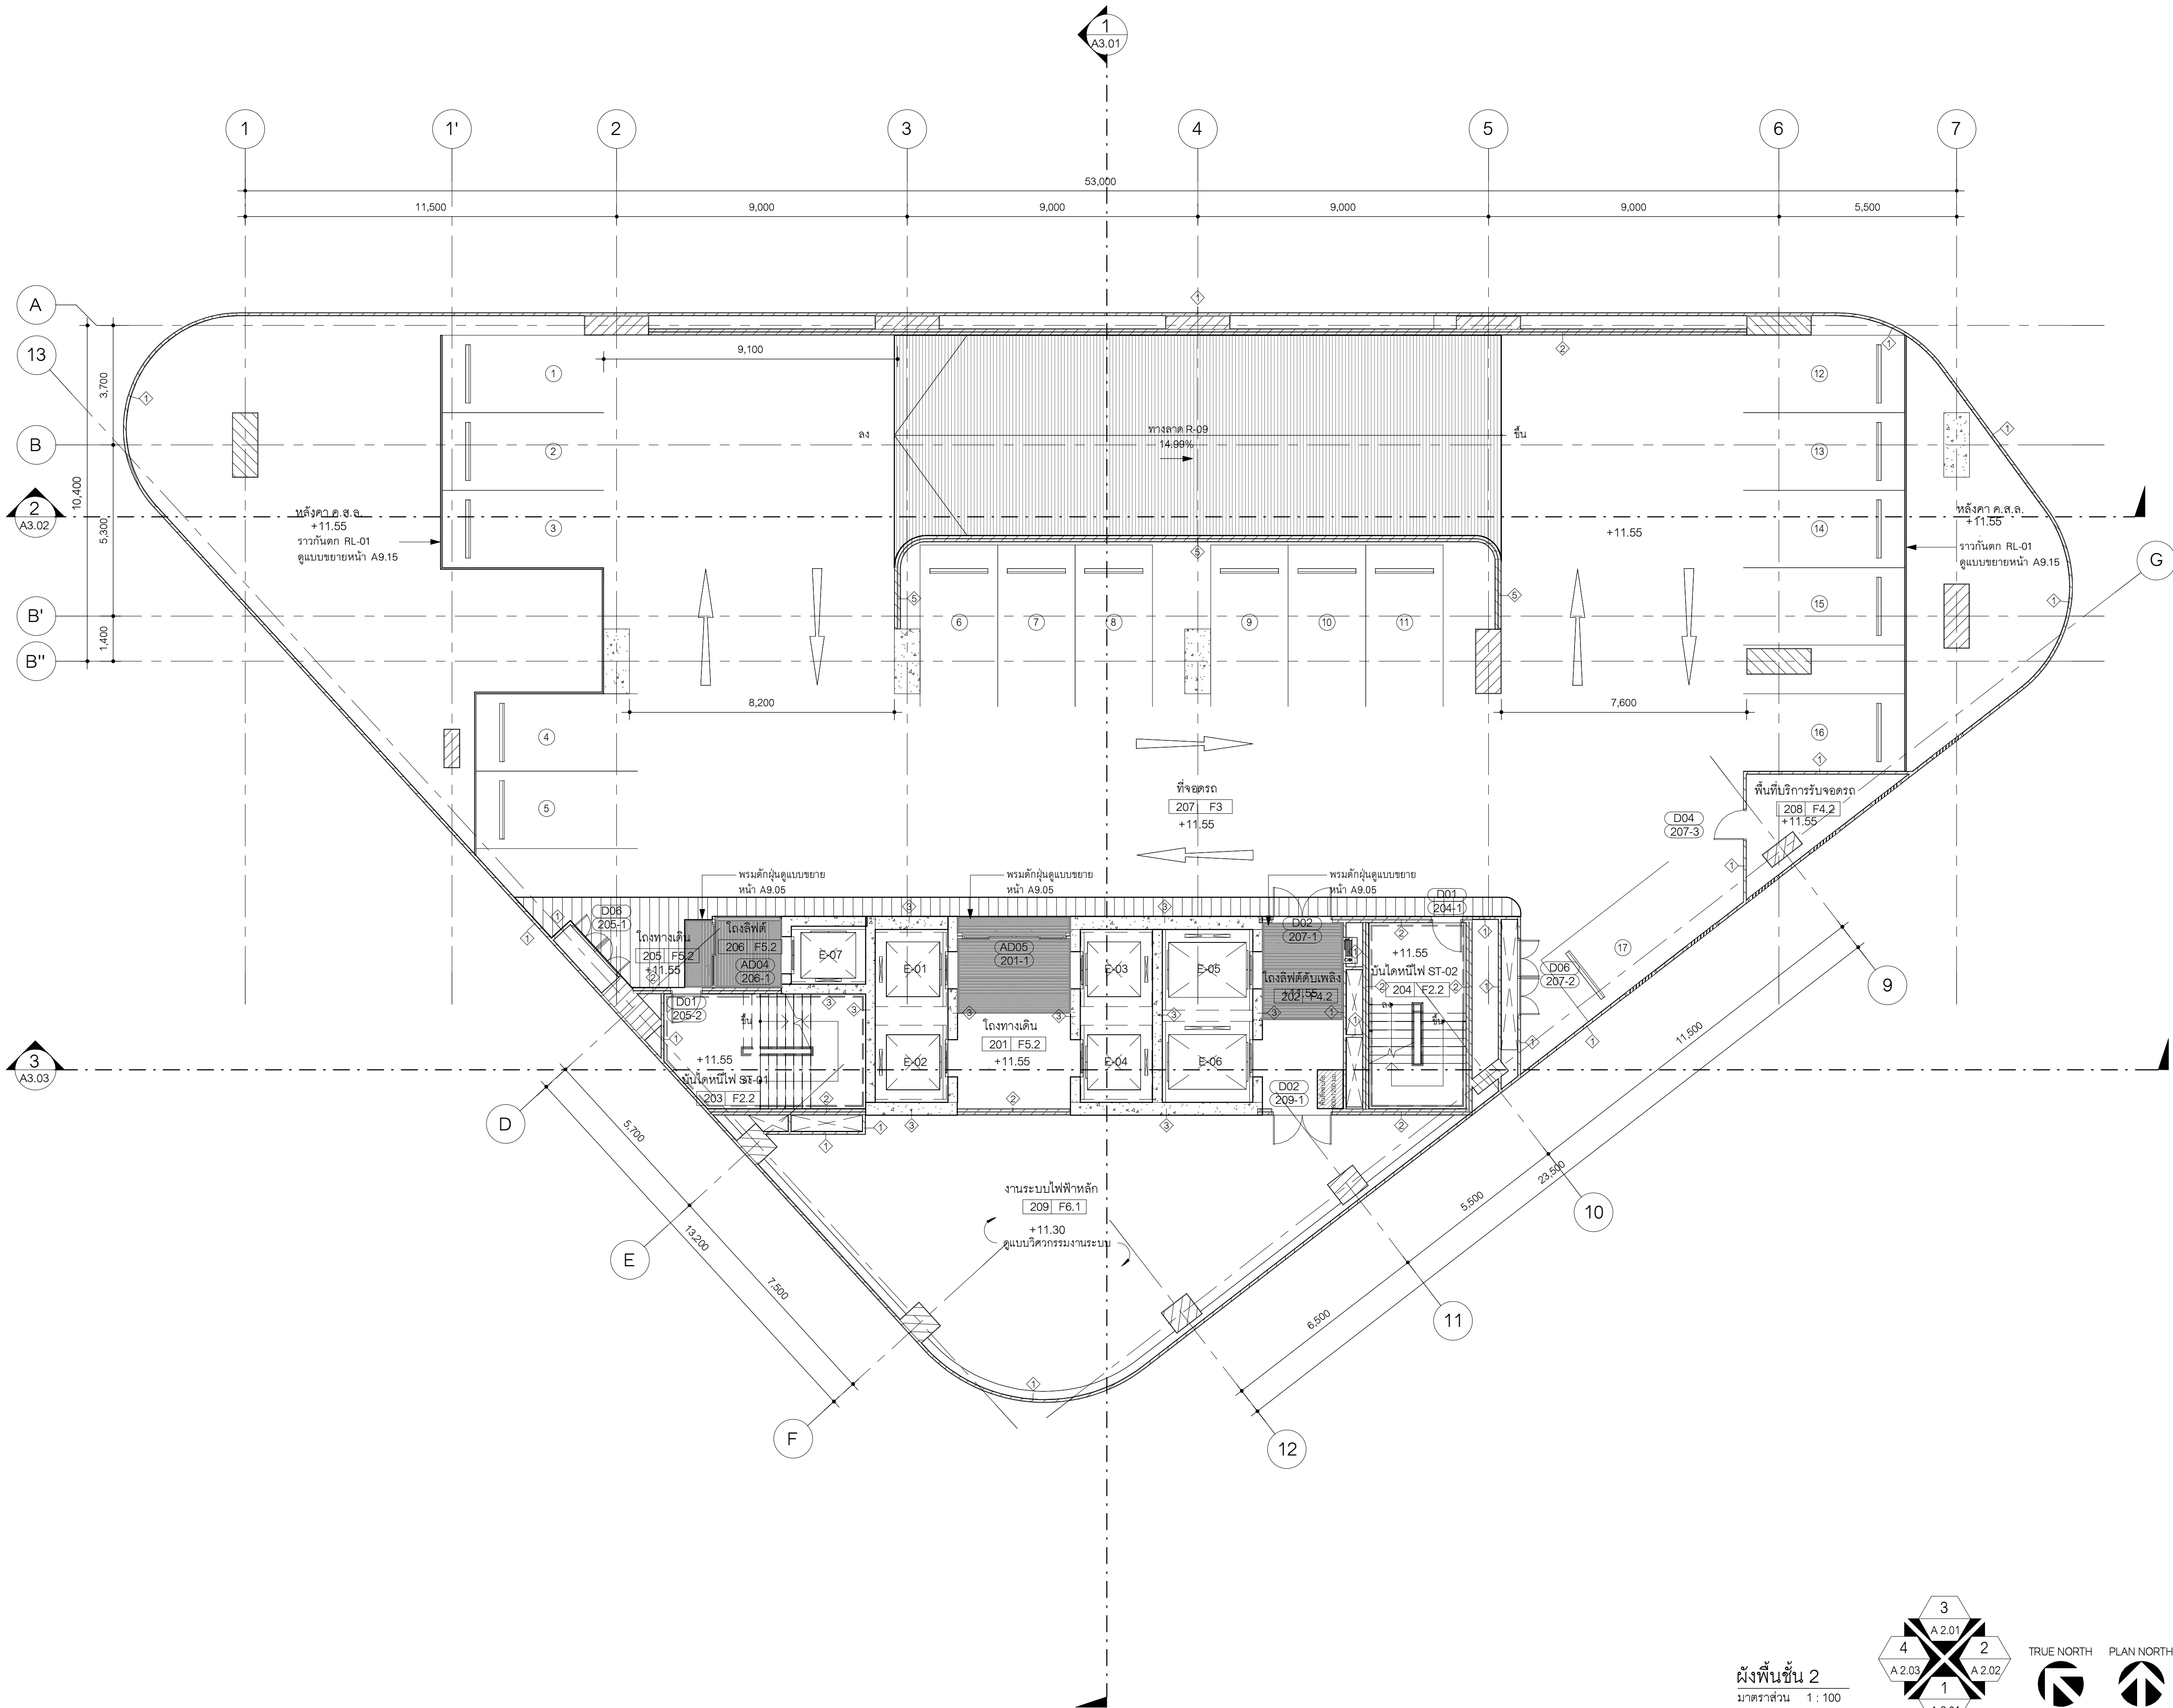

OWNER
LUXURY HOTEL DEVELOPMENT
SUKHUMVIT 38 CO., LTD.

DESIGNER
ARCHITECTS 49 LIMITED
81 SUKHUMVIT 26
BANGKOK 10110 THAILAND
T + 66 (0) 2260 4370
F + 66 (0) 2259 3872
E A49@A49.CO.TH
W A49.CO.TH

K.C.S. & ASSOCIATES CO. LTD.
22ND FLOOR, CHARN ISSARA TOWER II
2522/267 NEW PETCHABURI ROAD, BANGKAPI,
HUAY KWANG, BAKOK 10310 THAILAND
T +66 (0) 2308 2481 5
F +66 (0) 2308 2485

MEC PRO DESIGN CO. LTD.
567 BUILDING 4TH FLOOR, SUAN LUANG, BANGKOK 10250 THAILAND
T +66 (0) 2170 8029
F +66 (0) 37 034 8917
E MECPRO.DESIGN@GMAIL.COM

P.LANDSCAPE CO. LTD.
59/3 SUKHUMVIT 39, KLONGTON NUA,
WATTANA, BANGKOK 10110 THAILAND
T (622) 261 3700 TO 9
F (622) 238 3388
E INFO@PLANDSCAPE.COM
W WWW.PLANDSCAPE.COM

ARCHITECTS
พริษฐ์ วงศ์วรธรรม วสท.509
เนตรศศิธร อธิวิตร วสท.720
จารุวิมล อธิวิตร วสท.769
พริษฐ์ อธิวิตร วสท.3432
สุภากร ศรีสมบุญ วสท.3347
ปรีดี ตันนินโย วสท.20910
ศรพร ศิริพาน วสท.23830
วันรณ พูลสวัสดิ์ วสท.27171

STRUCTURAL ENGINEER
กาญจนา จันทวงษ์ วบ.1023
กุลธิ จันทวงษ์ สบ.9572
ภาณุ สายรวมญาติ สบ.15169
อภิสิทธิ์ สมอียง กบ.69140

ELECTRICAL ENGINEER
ชาน นิมิต วท.1118
ทนศักดิ์ พิศุสสง สท.1586
ธนวัฒน์ น้อยจ้อย ภทก.63548

MECHANICAL ENGINEER
เบน ไซพงษ์ สท.3566
ณภัทร วิเชียรพทยาคม ภท.51086
วิฑรศักดิ์ บุญนิยม ภท.52030

ENVIRONMENTAL ENGINEER
ทรงวุฒิ วิเศษศิลป์ สท.625
เบน ไซพงษ์ สท.112
วสุ สละยาบป สท.7507

SANITARY ENGINEER
ชื้อ นามสกุล เสงี่ยมญาติ

LANDSCAPE ARCHITECT
นัทธ วรรณสิน โฉม สท.108

GENERAL NOTE
1. THIS DRAWING IS THE PROPERTY OF ARCHITECTS 49 LIMITED OR ONE OF ITS AFFILIATES. IT IS ISSUED SUBJECT TO RETURN UPON DEMAND AND IS NOT TO BE USED EXCEPT IN CONNECTION WITH THE PROJECT FOR WHICH IT IS INTENDED.
2. DO NOT SCALE THIS DRAWING. USE FIGURED DIMENSIONS ONLY.
ให้ใช้ค่าตัวเลขที่กำหนดไว้เท่านั้น ห้ามวัดจากแบบ


PROJECT NAME
THE OKURA PRESTIGE
SUKHUMVIT BANGKOK HOTEL
AND SPA

DRAWING TITLE
ผังพื้นที่ 2

ISSUE/REVISION
NO DESCRIPTION BY DATE
1 แบบแปลนอาคาร A49 17/04/2569

CHECK BY
ARCHITECT SIGNED
PD
PA
JC
DRAWN BY Author
PRINTED DATE 17/04/2569
SCALE: 1:100
REF. FILE

DRAWING NO.
A1.07

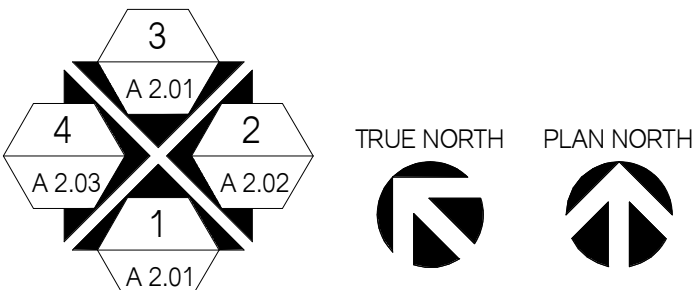

ผังพื้นที่ 2
มาตราส่วน 1:100

OWNER
LUXURY HOTEL DEVELOPMENT
SUKHUMVIT 38 CO., LTD.

DESIGNER
ARCHITECTS 49 LIMITED
81 SUKHUMVIT 26
BANGKOK 10110 THAILAND
T + 66 (0) 2260 4370
F + 66 (0) 2259 3872
E A49@A49.CO.TH
W A49.CO.TH

K.C.S. & ASSOCIATES CO. LTD.
22ND FLOOR, CHARN ISSARA TOWER II
2592/267 NEW PETCHABURI ROAD, BANGKAPI,
HUAY KWANG, BANGKOK 10310 THAILAND
T +66 (0) 2308 2481 5
F +66 (0) 2308 2485

MEC PRO DESIGN CO. LTD.
567 BUILDING 4TH FLOOR, SUAN LUANG, BANGKOK 10250 THAILAND
T +66 (0) 2170 8029
F +66 (0) 37 034 8917
E MECPRO.DESIGN@GMAIL.COM

P LANDSCAPE CO. LTD.
59/3 SUKHUMVIT 39, KLONGTON NUA,
WATTANA, BANGKOK 10110 THAILAND
T (622) 261 3700 TO 9
F (622) 238 3388
E INFO@PLANDSCAPE.COM
W WWW.PLANDSCAPE.COM

ARCHITECTS
พิธี วงศ์วิมลวรรณ วสท.509
เนรศักดิ์ อธิวิตร วสท.720
จารุวัฒน์ อธิวิตร วสท.769
พิณพร อธิวิตร วสท.3432
สุภากร ศรีสมบูรณ์ วสท.3347
ปาริชาติ หิมนันโย วสท.20910
ศรพร ศิริพาน วสท.23830
วันธนา พูลสวัสดิ์ วสท.27171

STRUCTURAL ENGINEER
กาญจนา จันทวงษ์ วสท.1023
กุลธิรา จันทวงษ์ สท.9572
ภาณุ สายรวมญาติ สท.15169
อภิสิทธิ์ สมอียง กษ.69140

ELECTRICAL ENGINEER
ชาน นิมิตร์ วท.1118
พนศักดิ์ พิศุสสง วท.1586
ธนวัฒน์ น้อยจ้อย วท.63548

MECHANICAL ENGINEER
เบนต์ ไชยพันธ์ สท.3566
ณภัทร วิเชียรพทยาคม กท.51086
วิฑรศักดิ์ บุญโคตร กท.52030

ENVIRONMENTAL ENGINEER
ทรงวุฒิ วิเศษศิลป์ สท.625
เบนต์ ไชยพันธ์ สท.112
วสุ ละลายอบป กท.7507

SANITARY ENGINEER
ธีธ นามสกุล เลขใบอนุญาต

LANDSCAPE ARCHITECT
นัทธกร รณนทีโนจันทร์ สท.108

GENERAL NOTE
1. THIS DRAWING IS THE PROPERTY OF ARCHITECTS 49 LIMITED OR ONE OF ITS AFFILIATES. IT IS ISSUED SUBJECT TO RETURN UPON DEMAND AND IS NOT TO BE USED EXCEPT IN CONNECTION WITH THE PROJECT FOR WHICH IT IS INTENDED.
2. DO NOT SCALE THIS DRAWING. USE FIGURED DIMENSIONS ONLY.
โปรดใช้ค่าเลขที่กำหนดไว้เท่านั้น ห้ามวัดจากแบบ

PROJECT NAME
THE OKURA PRESTIGE
SUKHUMVIT BANGKOK HOTEL
AND SPA

DRAWING TITLE
ผังพื้นที่ 2A

ISSUE/REVISION
NO DESCRIPTION BY DATE
1 แก้ไขแบบสถาปัตย์ A49 17/04/2569

CHECK BY DRAWING NO.

ARCHITECT SIGNED
PM
PD
PA
JC

DRAWN BY Author SCALE: 1:100
PRINTED DATE 17/04/2569 REF. FILE

A 49

KCS
K.C.S. & ASSOCIATES CO. LTD.

MEC PRO
DESIGN

pla

SIGNED

SIGNED


SIGNED

SIGNED

SIGNED

SIGNED

SIGNED

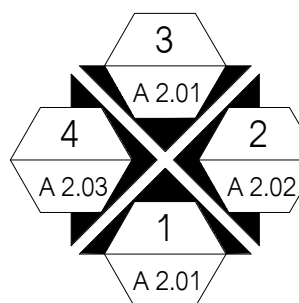

TRUE NORTH PLAN NORTH

ผังพื้นที่ 2A
มาตราส่วน 1:100

OWNER
LUXURY HOTEL DEVELOPMENT
SUKHUMVIT 38 CO., LTD.

DESIGNER
ARCHITECTS 49 LIMITED
81 SUKHUMVIT 26
BANGKOK 10110 THAILAND
T + 66 (0) 2260 4370
F + 66 (0) 2259 3872
E A49@A49.CO.TH
W A49.CO.TH

K.C.S. & ASSOCIATES CO. LTD.
22ND FLOOR, CHARN ISSARA TOWER II
2522/267 NEW PETCHABURI ROAD, BANGKAPI,
HUAY KWANG, BANGKOK 10310 THAILAND
T +66 (0) 2308 2481 5
F +66 (0) 2308 2485

MEC PRO DESIGN CO. LTD.
567 BUILDING 4TH FLOOR, SUKUMVIT 38
SUAN LUANG, BANGKOK 10250 THAILAND
T +66 (0) 2170 8029
F +66 (0) 37 034 8917
E MECPRO.DESIGN@GMAIL.COM

P.LANDSCAPE CO. LTD.
59/3 SUKHUMVIT 39, KLONKONG NUA,
WATTANA, BANGKOK 10110 THAILAND
T (622) 261 3700 TO 9
F (622) 258 3388
E INFO@PLANDSCAPE.COM
W WWW.PLANDSCAPE.COM

ARCHITECTS
พริษฐ์ วงศ์วิเศษวรรณ วสท.509
เนตรศศิษฐ์ อธิวิเศษ วสท.720
จารุวัฒน์ อธิวิเศษ วสท.769
พิชญพร อธิวิเศษ วสท.3432
สุชภา ศรีสมบูรณ์ วสท.3347
ปวิศร์ ชื่นนันทน์ วสท.20910
ศรพร ศิริพาน วสท.23830
วรินทร์ พูลสวัสดิ์ วสท.27171

STRUCTURAL ENGINEER
กาญจนา จันทวงษ์ วสท.1023
กุลธิรา จันทวงษ์ สท.9572
ภาณุ สายรวมญาติ สท.15169
อภิสิทธิ์ สมอียง สท.69140

ELECTRICAL ENGINEER
ชานน นิ่มนง วท.1118
ชนัดดี พิชัยสง สท.1386
ชนวิวัฒน์ น้อยจ้อย วกท.63548

MECHANICAL ENGINEER
เบนศ ไชยพงษ์ สท.3566
ณภัทร วิเชียรพทยาคม วกท.51086
วิฑรศักดิ์ บุญนิคม วกท.52030

ENVIRONMENTAL ENGINEER
ทรงวุฒิ วิเศษศิลป์ สท.625
เบนศ ไชยพงษ์ สท.112
วสุ ละลายบาลี สท.7507

SANITARY ENGINEER
ชื่อ นามสกุล เลขใบอนุญาต

LANDSCAPE ARCHITECT
นัทธกร รณาศรีโพธิ์ สท.108

GENERAL NOTE
1. THIS DRAWING IS THE PROPERTY OF ARCHITECTS 49 LIMITED OR ONE OF ITS AFFILIATES. IT IS ISSUED SUBJECT TO RETURN UPON DEMAND AND IS NOT TO BE USED EXCEPT IN CONNECTION WITH THE PROJECT FOR WHICH IT IS INTENDED.
2. DO NOT SCALE THIS DRAWING. USE FIGURED DIMENSIONS ONLY.
ให้ใช้ตัวเลขที่กำหนดไว้เท่านั้น ห้ามวัดจากแบบ

PROJECT NAME
THE OKURA PRESTIGE
SUKHUMVIT BANGKOK HOTEL
AND SPA


DRAWING TITLE
ผังพื้นที่ 2B

ISSUE/REVISION
NO DESCRIPTION BY DATE
1 แก้ไขแบบอาคาร A49 17/04/2569


CHECK BY DRAWING NO.


ARCHITECT SIGNED
PD
PA
JC
A1.09

DRAWN BY Author SCALE: 1:100
PRINTED DATE 17/04/2569 REF. FILE


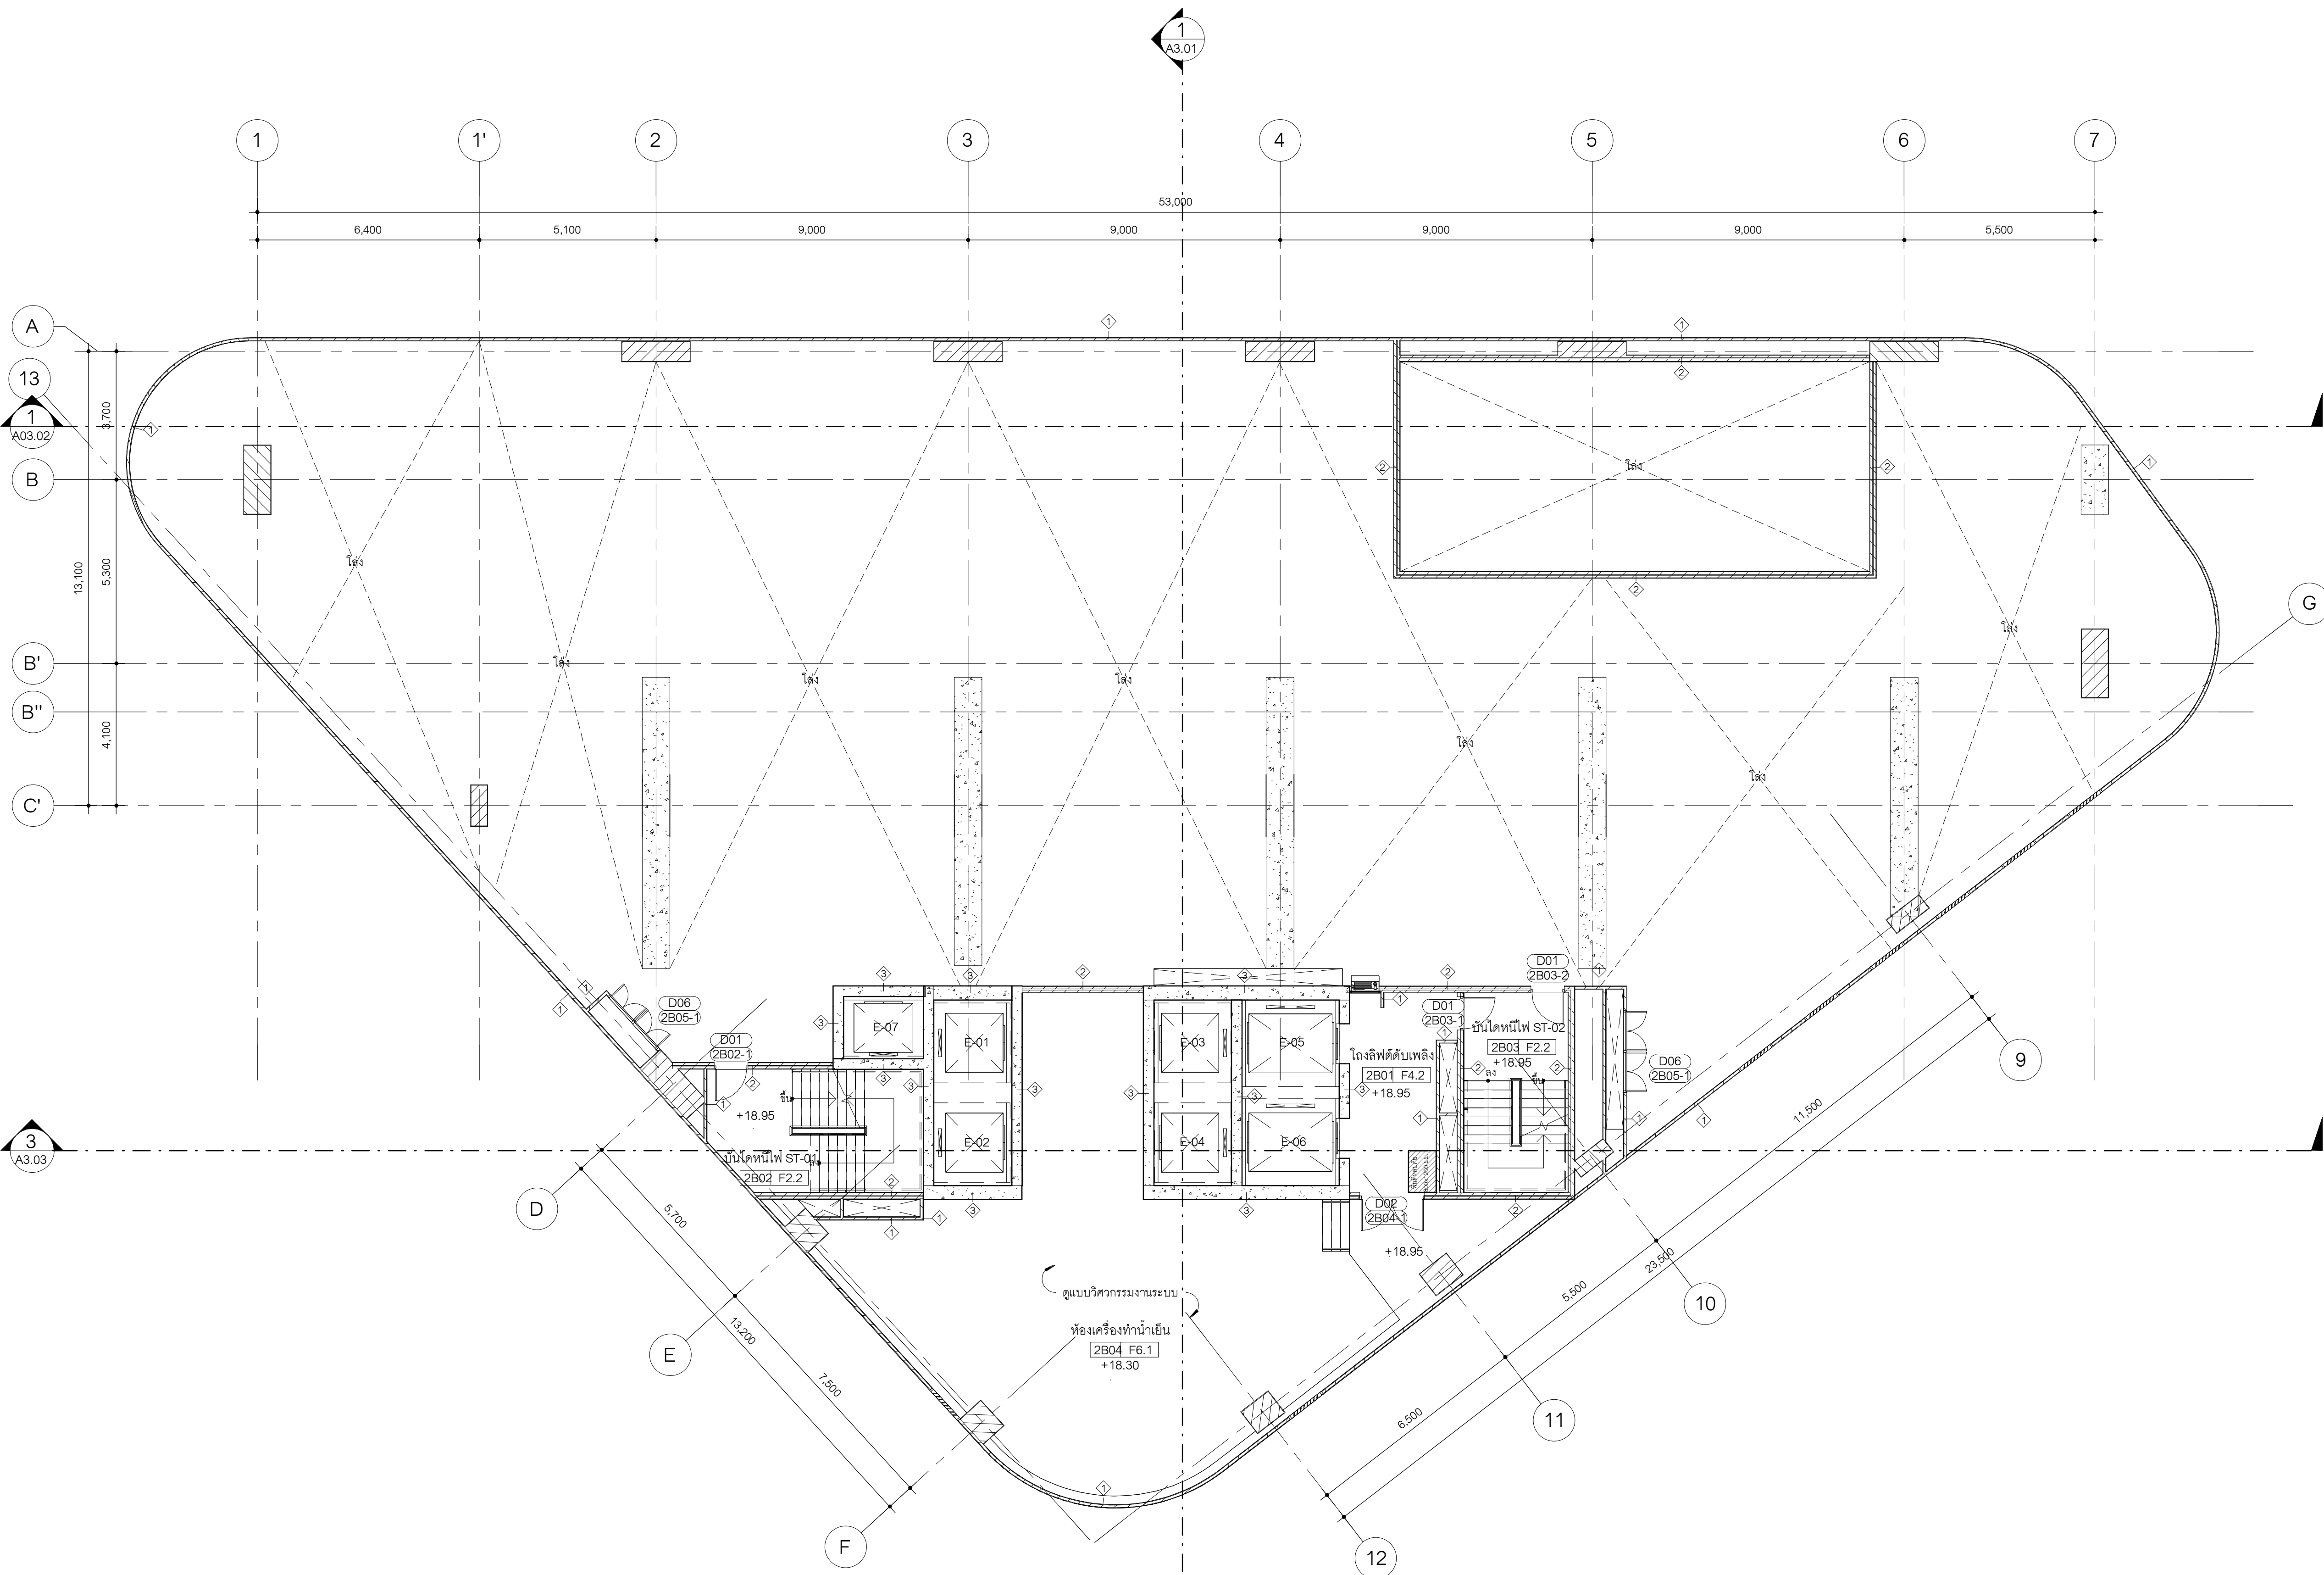


ผังพื้นที่ 2B
มาตราส่วน 1 : 100

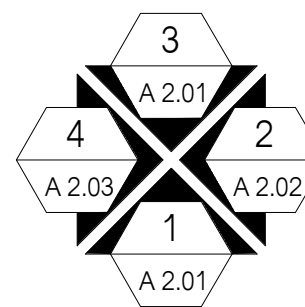

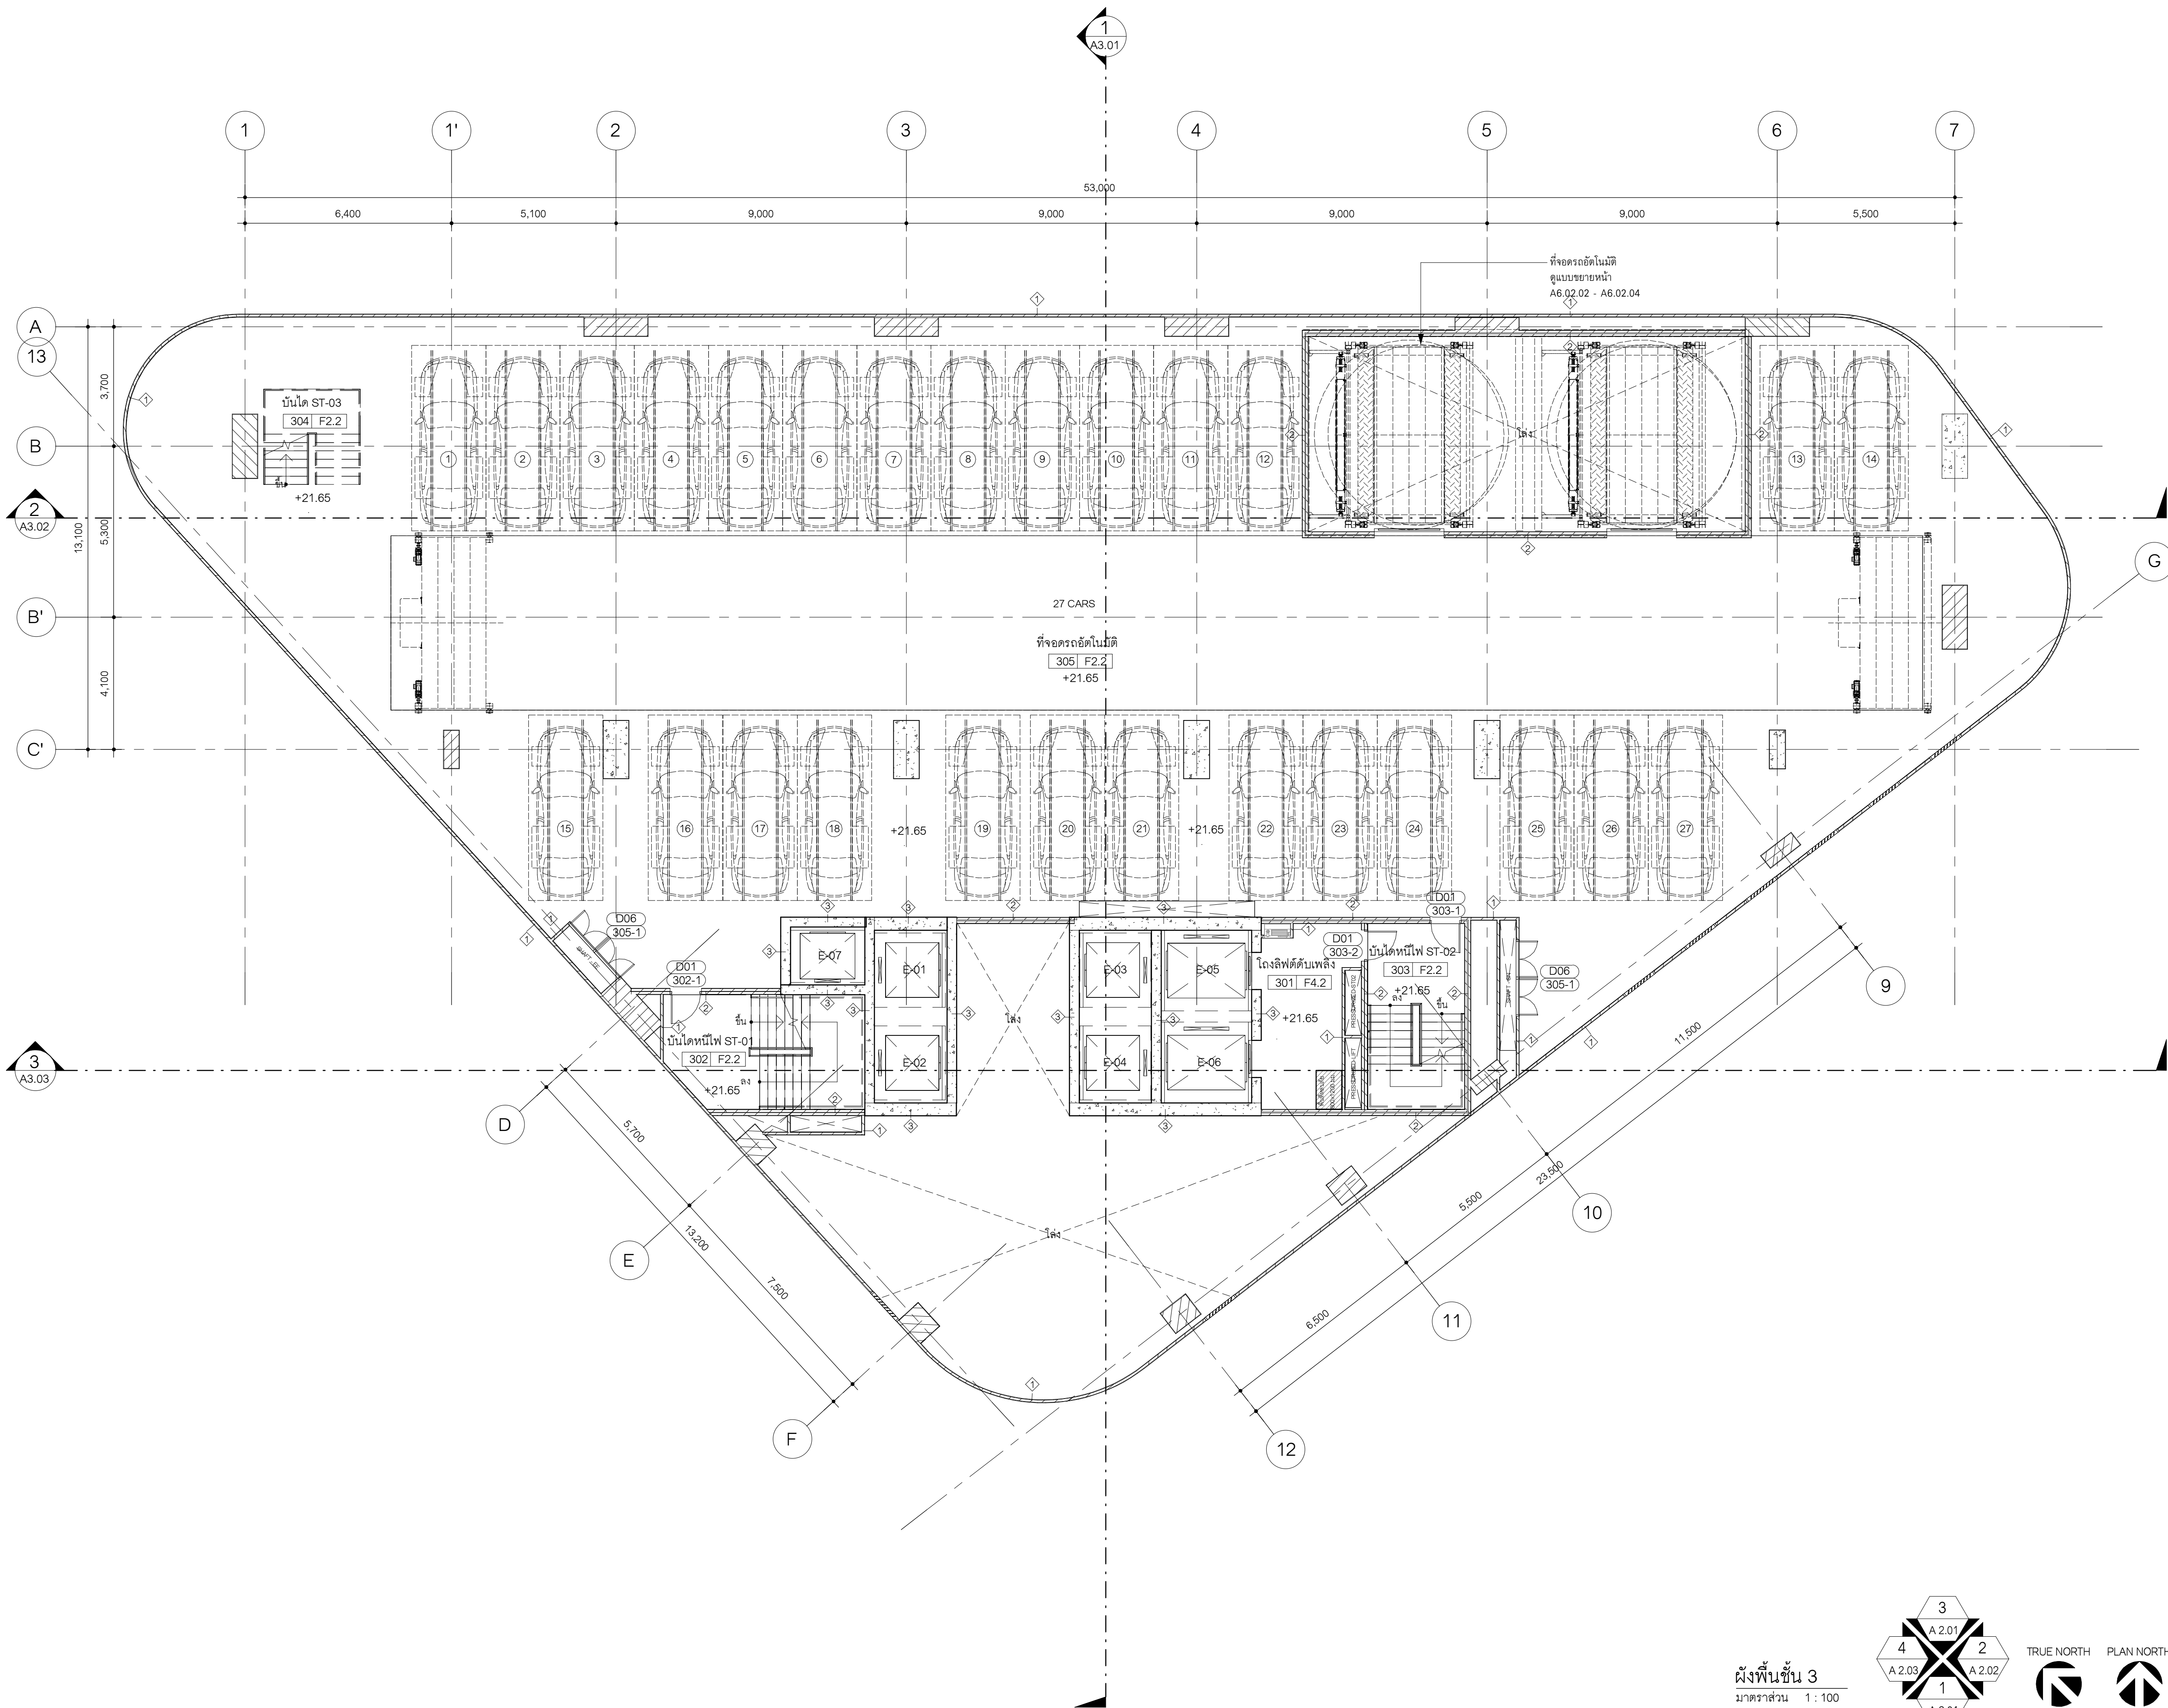

ผังพื้นที่ 3
มาตราส่วน 1 : 100

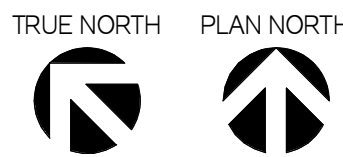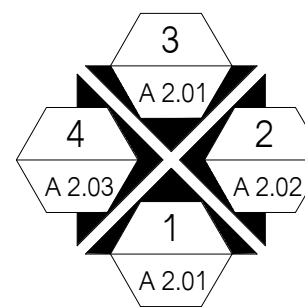

OWNER
LUXURY HOTEL DEVELOPMENT
SUKHUMVIT 38 CO., LTD.

DESIGNER
ARCHITECTS 49 LIMITED
81 SUKHUMVIT 26
BANGKOK 10110 THAILAND
T + 66 (0) 2260 4370
F + 66 (0) 2259 3872
E A49@A49.CO.TH
W A49.CO.TH

A | 49

K.C.S. & ASSOCIATES CO. LTD.
22ND FLOOR, CHARN ISSARA TOWER II
2522/267 NEW PETCHABURI ROAD, BANGKAPI,
HUAY KWANG, BAKOK 10310 THAILAND
T +66 (0) 2308 2481 5
F +66 (0) 2308 2485

KCS
K.C.S. & ASSOCIATES CO. LTD.

MEC PRO DESIGN CO. LTD.
567 BUILDING 4TH FLOOR, SUK 51
SUAN LUANG, BANGKOK 10250 THAILAND
T +66 (0) 2170 8029
F +66 (0) 37 034 8917
E MECPRO.DESIGN@GMAIL.COM

MEC PRO
DESIGN

P.LANDSCAPE CO. LTD.
59/3 SUKHUMVIT 39, KLONKONG NUA,
WATTANA, BANGKOK 10110 THAILAND
T (622) 261 3700 TO 9
F (622) 238 3388
E INFO@PLANDSCAPE.COM
W WWW.PLANDSCAPE.COM

pla | | |

ARCHITECTS
ที่ปรึกษา วรวิทย์วรรณ วรณ.509
เนรมิตวิทย์ อธิวิตร วรณ.720
จารุวิมล อธิวิตร วรณ.769
พิชญพร อธิวิตร วรณ.3432
สุภากร ศรีสมบุญ วรณ.3347
ปวิศร์ พิณนโวย วรณ.20910
ศรพร ศิริพาน วรณ.23830
วริชธรณ์ พูลสวัสดิ์ วรณ.27171

SIGNED

STRUCTURAL ENGINEER
ทนาย จันทวงศ วรณ.1023
กุลสิริ จันทวงศ สร.9572
ภาสกร สายรวมญาติ สร.15169
อภิสิทธิ์ สมอียง สร.69140

SIGNED

ELECTRICAL ENGINEER
ชาน นิมิตกร วรณ.1118
พนศักดิ์ พิศุสสง สร.1386
ธนวิวัฒน์ น้อยจ้อย วรณ.63548

SIGNED

MECHANICAL ENGINEER
เบนต์ ไชยพงษ์ สร.3566
ณภัทร วิเชียรพทยาคม วรณ.51086
วิฑรศักดิ์ บุญโคตร วรณ.52030

SIGNED

ENVIRONMENTAL ENGINEER
ทรงวุฒิ วิเศษศิลป์ สร.625
เบนต์ ไชยพงษ์ สร.112
วสุ สดสายศิลป์ สร.7507

SIGNED

SANITARY ENGINEER
ชื่อ นามสกุล เลขใบอนุญาต

SIGNED

LANDSCAPE ARCHITECT
บริษัท วรรณศิลป์ จำกัด สร.108

SIGNED

GENERAL NOTE
1. THIS DRAWING IS THE PROPERTY OF ARCHITECTS 49 LIMITED OR ONE OF ITS AFFILIATES. IT IS ISSUED SUBJECT TO RETURN UPON DEMAND AND IS NOT TO BE USED EXCEPT IN CONNECTION WITH THE PROJECT FOR WHICH IT IS INTENDED.
2. DO NOT SCALE THIS DRAWING. USE FIGURED DIMENSIONS ONLY.
โปรดใช้ค่าเลขที่กำหนดไว้เท่านั้น ห้ามวัดจากแบบ

PROJECT NAME
THE OKURA PRESTIGE
SUKHUMVIT BANGKOK HOTEL
AND SPA

DRAWING TITLE
ผังพื้นที่ 3

ISSUE/REVISION
NO DESCRIPTION BY DATE
1 แบบแปลนสถาปัตย์ A49 17/04/2569


CHECK BY **DRAWING NO.**

ARCHITECT SIGNED
PM
PD
PA
JC

A1.10

DRAWN BY Author SCALE: 1 : 100
PRINTED DATE 17/04/2569 REF. FILE

4/18/2026 3:18:37 PM

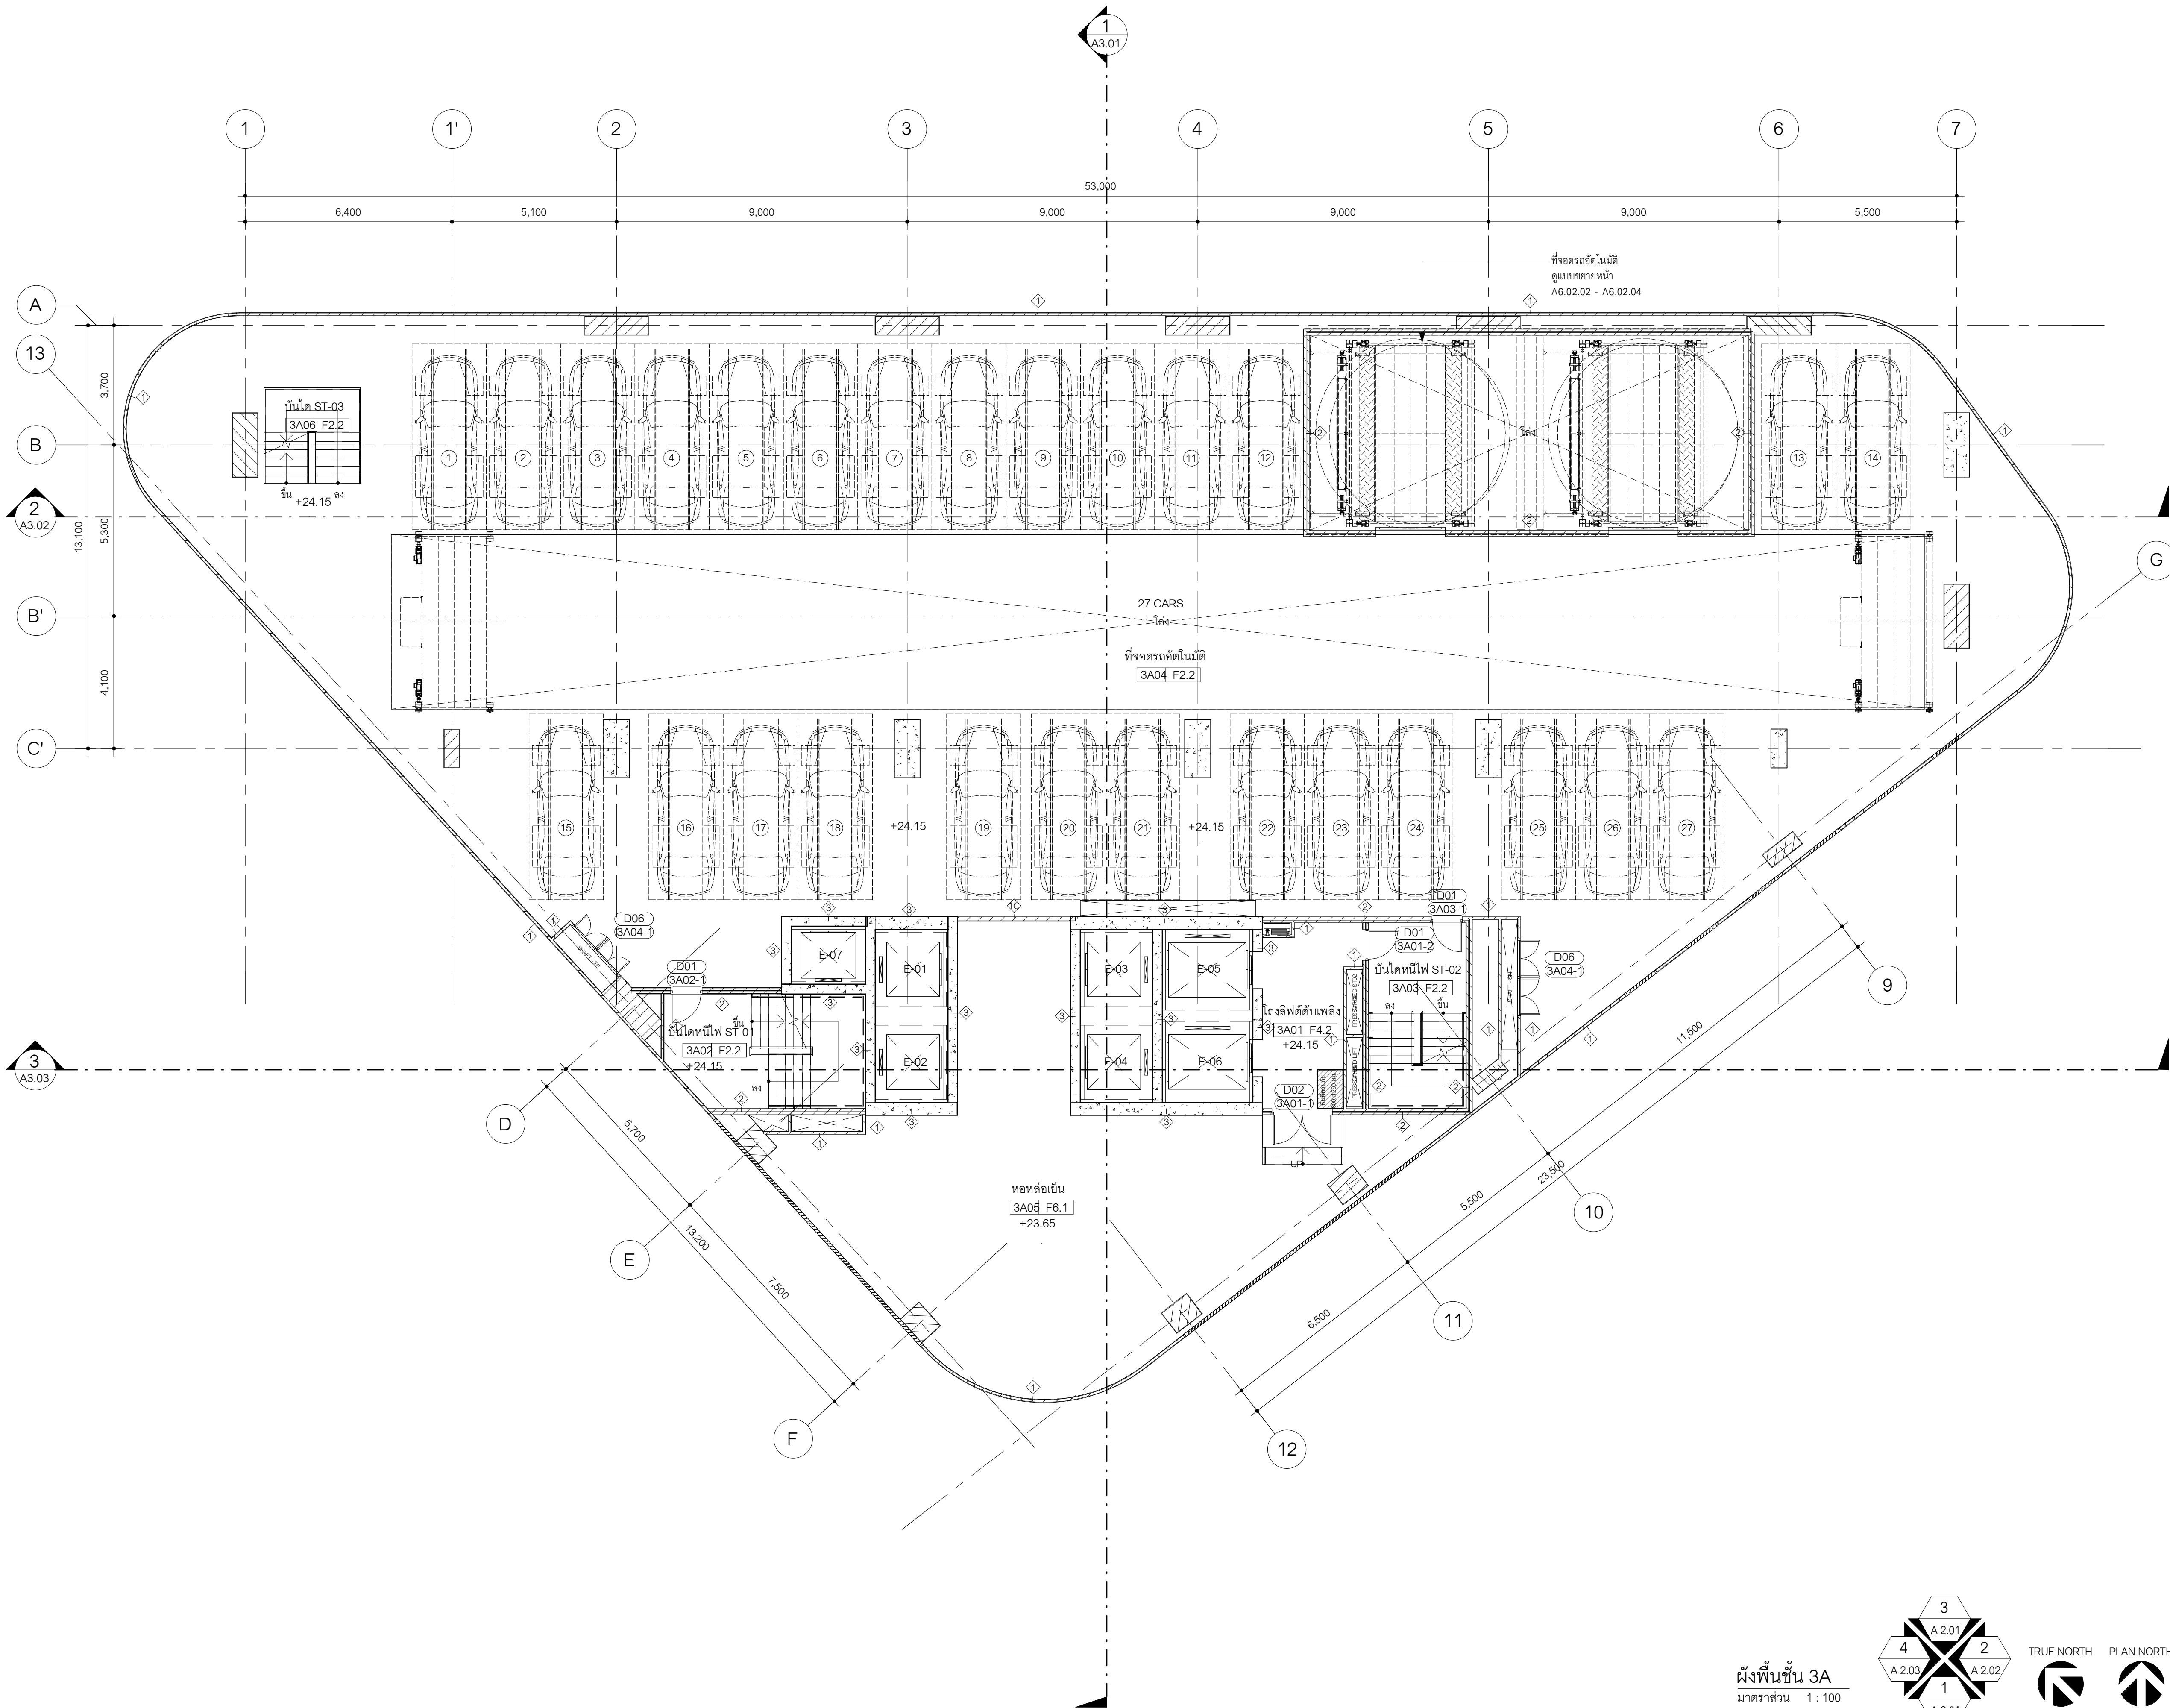

OWNER
LUXURY HOTEL DEVELOPMENT
SUKHUMVIT 38 CO., LTD.

DESIGNER
ARCHITECTS 49 LIMITED
81 SUKHUMVIT 26
BANGKOK 10110 THAILAND
T + 66 (0) 2260 4370
F + 66 (0) 2259 3872
E A49@A49.CO.TH
W A49.CO.TH

K.C.S. & ASSOCIATES CO. LTD.
22ND FLOOR, CHARN ISSARA TOWER II
2522/267 NEW PETCHABURI ROAD, BANGKAPI,
HUAY KWANG, BAKOK 10310 THAILAND
T + 66 (0) 2308 2481 5
F + 66 (0) 2308 2485

MEC PRO DESIGN CO. LTD.
567 BUILDING 4TH FLOOR, 1X SOI 51
SUAN LUANG, BANGKOK 10250 THAILAND
T + 66 (0) 2170 8029
F + 66 (0) 37 034 8917
E MECPRO.DESIGN@GMAIL.COM

P.LANDSCAPE CO. LTD.
59/3 SUKHUMVIT 39, KLONLON NUA,
WATTANA, BANGKOK 10110 THAILAND
T (622) 261 3700 TO 9
F (622) 238 3388
E INFO@PLANDSCAPE.COM
W WWW.PLANDSCAPE.COM

ARCHITECTS
ที่ปรึกษา วรวิทย์วรรณ วรณ.509
เนรมิตวิทย์ อธิวิตร วรณ.720
จารุวิมล อธิวิตร วรณ.769
พิชญพร อธิวิตร วรณ.3432
สุภากร ศรีสมบุญ วรณ.3347
ปาริชาติ หิมนันโย วรณ.20910
ศรพร ศิริพาน วรณ.23830
วันธรรณ์ พูลสวัสดิ์ วรณ.27171

STRUCTURAL ENGINEER
ทนาย จันทราวุธ วรณ.1023
กุลศิริ จันทราวุธ สร.9572
ภาณุ สายรวมญาติ สร.15169
อภิสิทธิ์ สมอ้ง สร.69140

ELECTRICAL ENGINEER
ชาน นิมิตกร วรณ.1118
ชนัดดา สร.1386
ชนวิวัฒน์ น้อยจ้อย วรณ.63548

MECHANICAL ENGINEER
เบนต ไชยพงษ์ สร.3566
ณภัทร วิเชียรเทพาคุณ สร.51086
วิฑรศักดิ์ บุญโคตร สร.52030

ENVIRONMENTAL ENGINEER
ทรงวุฒิ วิเศษศิลป์ สร.625
เบนต ไชยพงษ์ สร.112
วสุ สร.7507

SANITARY ENGINEER
ชื่อ นามสกุล เลขใบอนุญาต

LANDSCAPE ARCHITECT
นัทธกร รณศิริโพธิ์ สร.108

GENERAL NOTE
1. THIS DRAWING IS THE PROPERTY OF ARCHITECTS 49 LIMITED OR ONE OF ITS AFFILIATES. IT IS ISSUED SUBJECT TO RETURN UPON DEMAND AND IS NOT TO BE USED EXCEPT IN CONNECTION WITH THE PROJECT FOR WHICH IT IS INTENDED.
2. DO NOT SCALE THIS DRAWING. USE FIGURED DIMENSIONS ONLY.
โปรดใช้ค่าตัวเลขที่กำหนดไว้เท่านั้น ห้ามวัดจากแบบ

PROJECT NAME
THE OKURA PRESTIGE
SUKHUMVIT BANGKOK HOTEL
AND SPA

DRAWING TITLE
ผังพื้นที่ 3A


ISSUE/REVISION
NO DESCRIPTION BY DATE
1 แบบแปลนอาคาร A49 17/04/2569

CHECK BY DRAWING NO.

ARCHITECT SIGNED
PM
PD
PA
JC
A1.11

DRAWN BY Author SCALE: 1:100
PRINTED DATE 17/04/2569 REF. FILE

ผังพื้นที่ 3A
มาตราส่วน 1:100

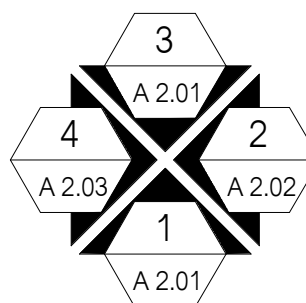

TRUE NORTH
PLAN NORTH

OWNER
LUXURY HOTEL DEVELOPMENT
SUKHUMVIT 38 CO., LTD.

DESIGNER
ARCHITECTS 49 LIMITED
81 SUKHUMVIT 26
BANGKOK 10110 THAILAND
T + 66 (0) 2260 4370
F + 66 (0) 2259 3872
E A49@A49.CO.TH
W A49.CO.TH

K.C.S. & ASSOCIATES CO. LTD.
22ND FLOOR, CHARN ISSARA TOWER II
2522/267 NEW PETCHABURI ROAD, BANGKAPI,
HUAY KWANG, BAKOK 10310 THAILAND
T +66 (0) 2308 2481 5
F +66 (0) 2308 2485

MEC PRO DESIGN CO. LTD.
567 BUILDING 4TH FLOOR, 1X SOI 51
SUAN LUANG, BANGKOK 10250 THAILAND
T +66 (0) 2170 8029
F +66 (0) 37 034 8917
E MECPRO.DESIGN@GMAIL.COM

P.LANDSCAPE CO. LTD.
59/3 SUKHUMVIT 39, KLONGTON NUA,
WATTANA, BANGKOK 10110 THAILAND
T (622) 261 3700 TO 9
F (622) 238 5588
E INFO@PLANDSCAPE.COM
W WWW.PLANDSCAPE.COM

ARCHITECTS
พริษฐ์ วงศ์ไชยวรรณ วสท.509
ณรงค์ชัย อธิวิตร วสท.720
จารุวัฒน์ อภิรมย์ศิริ วสท.769
พิชญพร อภิรมย์ศิริ วสท.3432
สุภากร ศรีสมบุญ วสท.3347
ปรีติศักดิ์ จันทร์นวล วสท.20910
ศรพร ศิริพาน วสท.23830
วรินทร์ณัน พูลสวัสดิ์ วสท.27171

STRUCTURAL ENGINEER
กาญจนา จันทวงษ์ วบ.1023
กุลธิรา จันทวงษ์ สบ.9572
ภาณุ สายรวมญาติ สบ.15169
อภิสิทธิ์ สมอ้ง กบ.69140

ELECTRICAL ENGINEER
ชานน นิ่มนง พท.1118
ชนัดดีศรี พท.1386
ชนวิวัฒน์ น้อยจ้อย พท.63548

MECHANICAL ENGINEER
ธนศ ไชยพงษ์ สท.3566
ณภัทร วิเชียรเมตตาคุณ ภท.51086
วิฑูรย์ บุญวิเศษ ภท.52030

ENVIRONMENTAL ENGINEER
ทรงวุฒิ วิเศษศิลป์ สท.625
ธนศ ไชยพงษ์ ภท.112
วสุ ละลายบาป ภท.7507

SANITARY ENGINEER
ชื่อ นามสกุล เลขใบอนุญาต

LANDSCAPE ARCHITECT
นัทธี วรรณสินธ์ สท.108

GENERAL NOTE
1. THIS DRAWING IS THE PROPERTY OF ARCHITECTS 49 LIMITED OR ONE OF ITS AFFILIATES. IT IS ISSUED SUBJECT TO RETURN UPON DEMAND AND IS NOT TO BE USED EXCEPT IN CONNECTION WITH THE PROJECT FOR WHICH IT IS INTENDED.
2. DO NOT SCALE THIS DRAWING. USE FIGURED DIMENSIONS ONLY.
โปรดใช้ค่าตัวเลขที่กำหนดไว้เท่านั้น ห้ามวัดจากแบบ

PROJECT NAME
THE OKURA PRESTIGE
SUKHUMVIT BANGKOK HOTEL
AND SPA


DRAWING TITLE
ผังพื้นที่ 4

ISSUE/REVISION
NO DESCRIPTION BY DATE
1 แบบแปลนอาคาร A49 17/04/2569

CHECK BY DRAWING NO.

ARCHITECT SIGNED
PM
PD
PA
JC

DRAWN BY Author SCALE: 1:100
PRINTED DATE 17/04/2569 REF. FILE

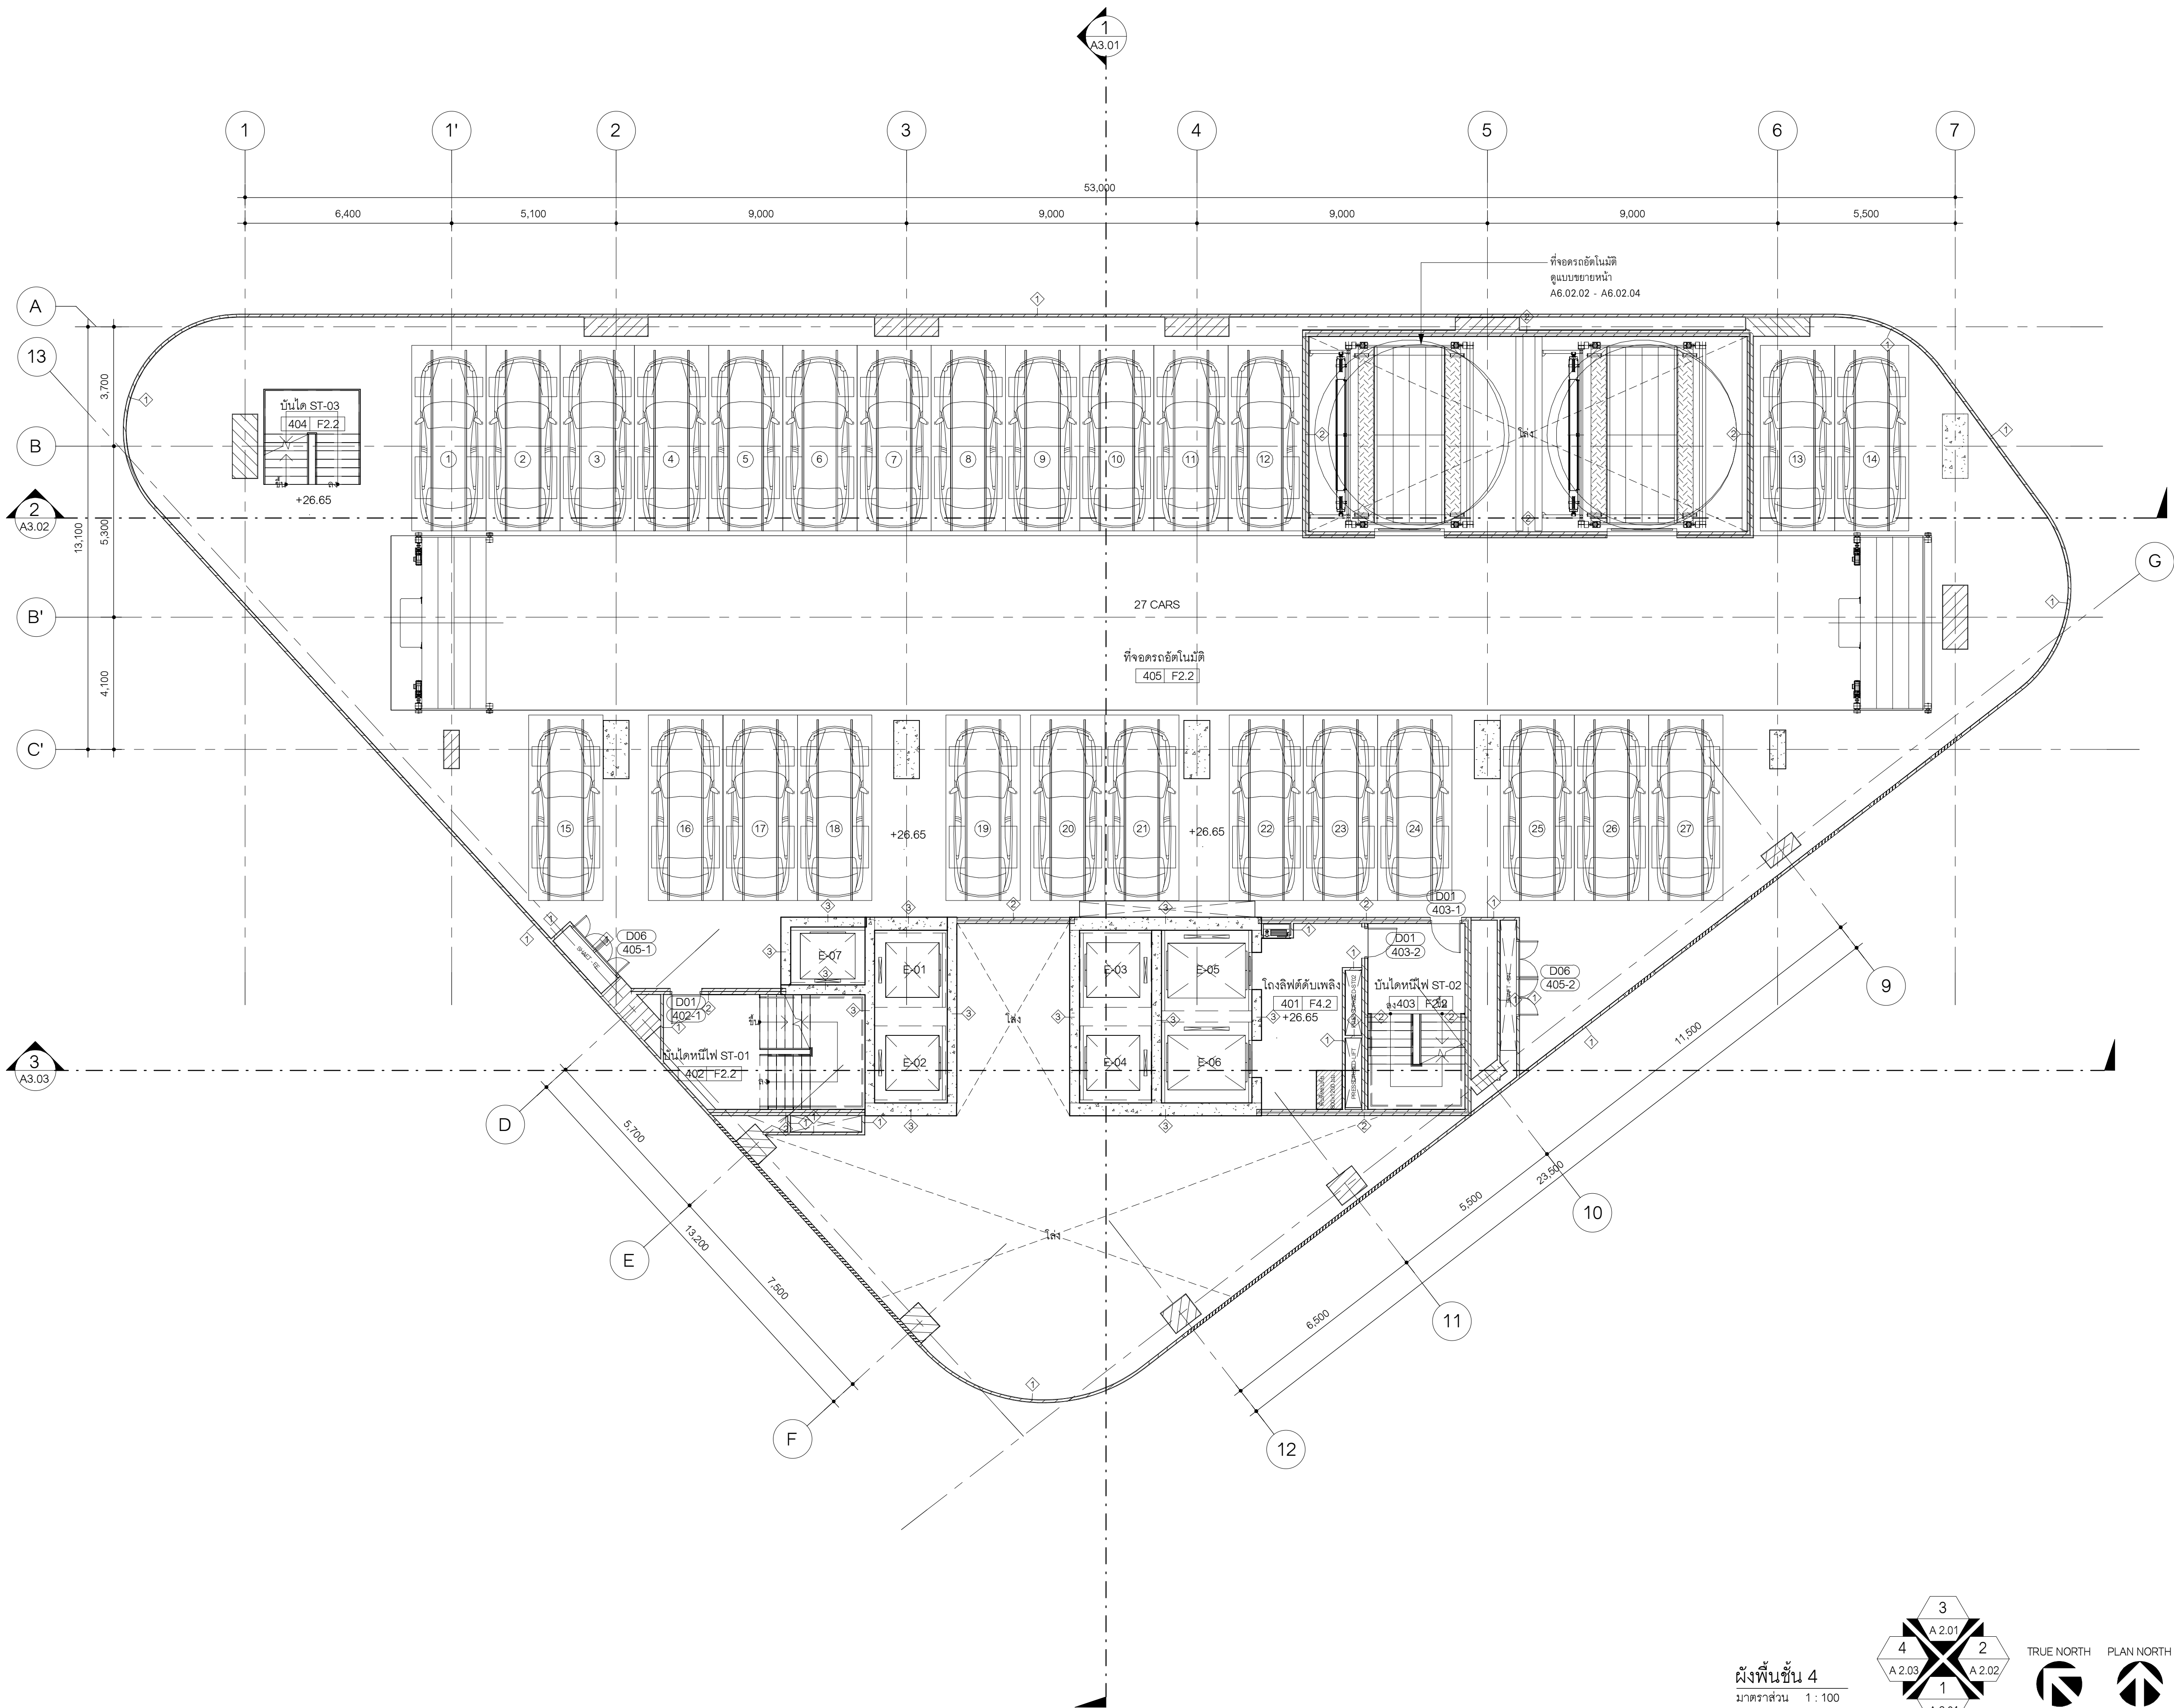

ผังพื้นที่ 4
มาตราส่วน 1 : 100

