

OWNER
LUXURY HOTEL DEVELOPMENT
SUKHUMVIT 38 CO., LTD.

DESIGNER
ARCHITECTS 49 LIMITED
81 SUKHUMVIT 26
BANGKOK 10110 THAILAND
T + 66 (0) 2260 4370
F + 66 (0) 2259 3872
E A49@A49.CO.TH
W A49.CO.TH

K.C.S. & ASSOCIATES CO. LTD.
22ND FLOOR, CHARN ISSARA TOWER II
2522/267 NEW PETCHABURI ROAD, BANGKAPI,
HUAY KWANG, BANGKOK 10310 THAILAND
T +66 (0) 2308 2481 5
F +66 (0) 2308 2485

MEC PRO DESIGN CO. LTD.
567 BUILDING 4TH FLOOR, SUKUMVIT 38
SUAN LUANG, BANGKOK 10250 THAILAND
T +66 (0) 2170 8029
F +66 (0) 2170 8917
E MECPRO.DESIGN@GMAIL.COM

P.LANDSCAPE CO. LTD.
59/3 SUKHUMVIT 39, KLONLON NUA,
WATTANA, BANGKOK 10110 THAILAND
T (622) 261 3700 TO 9
F (622) 238 3388
E INFO@PLANDSCAPE.COM
W WWW.PLANDSCAPE.COM

ARCHITECTS
พริษฐ์ วงศ์ไวศยวรรณ วสท.509
เนรศักดิ์ อารีมิตร วสท.720
จารุวัฒน์ อภิรมย์สวัสดิ์ วสท.769
พิณพชร อภิรมย์สวัสดิ์ วสท.3432
สุภากร ศรีสมบุญ วสท.3347
ปรีติศักดิ์ ชื่นนันทน์ วสท.20910
ศรพร ศิริพาน วสท.23830
วริศรณัน พูลสวัสดิ์ วสท.27171

STRUCTURAL ENGINEER
กาญจนา จันทวงษ์ วท.1023
กุลธิรา จันทวงษ์ สท.9572
ภาณุ สายรวมญาติ สท.15169
อภิสิทธิ์ สมอียง สท.69140

ELECTRICAL ENGINEER
ชานน นิ่มตรง วท.1118
ชนัดดา พิธีสุข สท.1386
ชนวิวัฒน์ น้อยจ้อย วท.63548

MECHANICAL ENGINEER
เบนซ์ ไชยพงษ์ สท.3566
ณภัทร วิเชียรเมตตาคุณ วท.51086
วิฑูรย์ บุญนิเทศ วท.52030

ENVIRONMENTAL ENGINEER
ทรงวุฒิ วิเศษศิลป์ สท.625
เบนซ์ ไชยพงษ์ สท.112
วสุ ละลายอบป สท.7507

SANITARY ENGINEER
ช่อ นามสกุล เลขใบอนุญาต

LANDSCAPE ARCHITECT
นัทธกร รณศิริโนโจน สท.108

GENERAL NOTE
1. THIS DRAWING IS THE PROPERTY OF ARCHITECTS 49 LIMITED OR ONE OF ITS AFFILIATES. IT IS ISSUED SUBJECT TO RETURN UPON DEMAND AND IS NOT TO BE USED EXCEPT IN CONNECTION WITH THE PROJECT FOR WHICH IT IS INTENDED.
2. DO NOT SCALE THIS DRAWING. USE FIGURED DIMENSIONS ONLY.
โปรดใช้ค่าตัวเลขที่กำหนดไว้เท่านั้น ห้ามวัดจากแบบ

PROJECT NAME
THE OKURA PRESTIGE
SUKHUMVIT BANGKOK HOTEL
AND SPA


DRAWING TITLE
ผังพื้นที่ 4A

ISSUE/REVISION
NO DESCRIPTION BY DATE
1 แบบแปลนอาคาร A49 17/04/2569


CHECK BY DRAWING NO.

ARCHITECT SIGNED
PD
PA
JC
A1.13

DRAWN BY Author SCALE: 1:100
PRINTED DATE 17/04/2569 REF. FILE

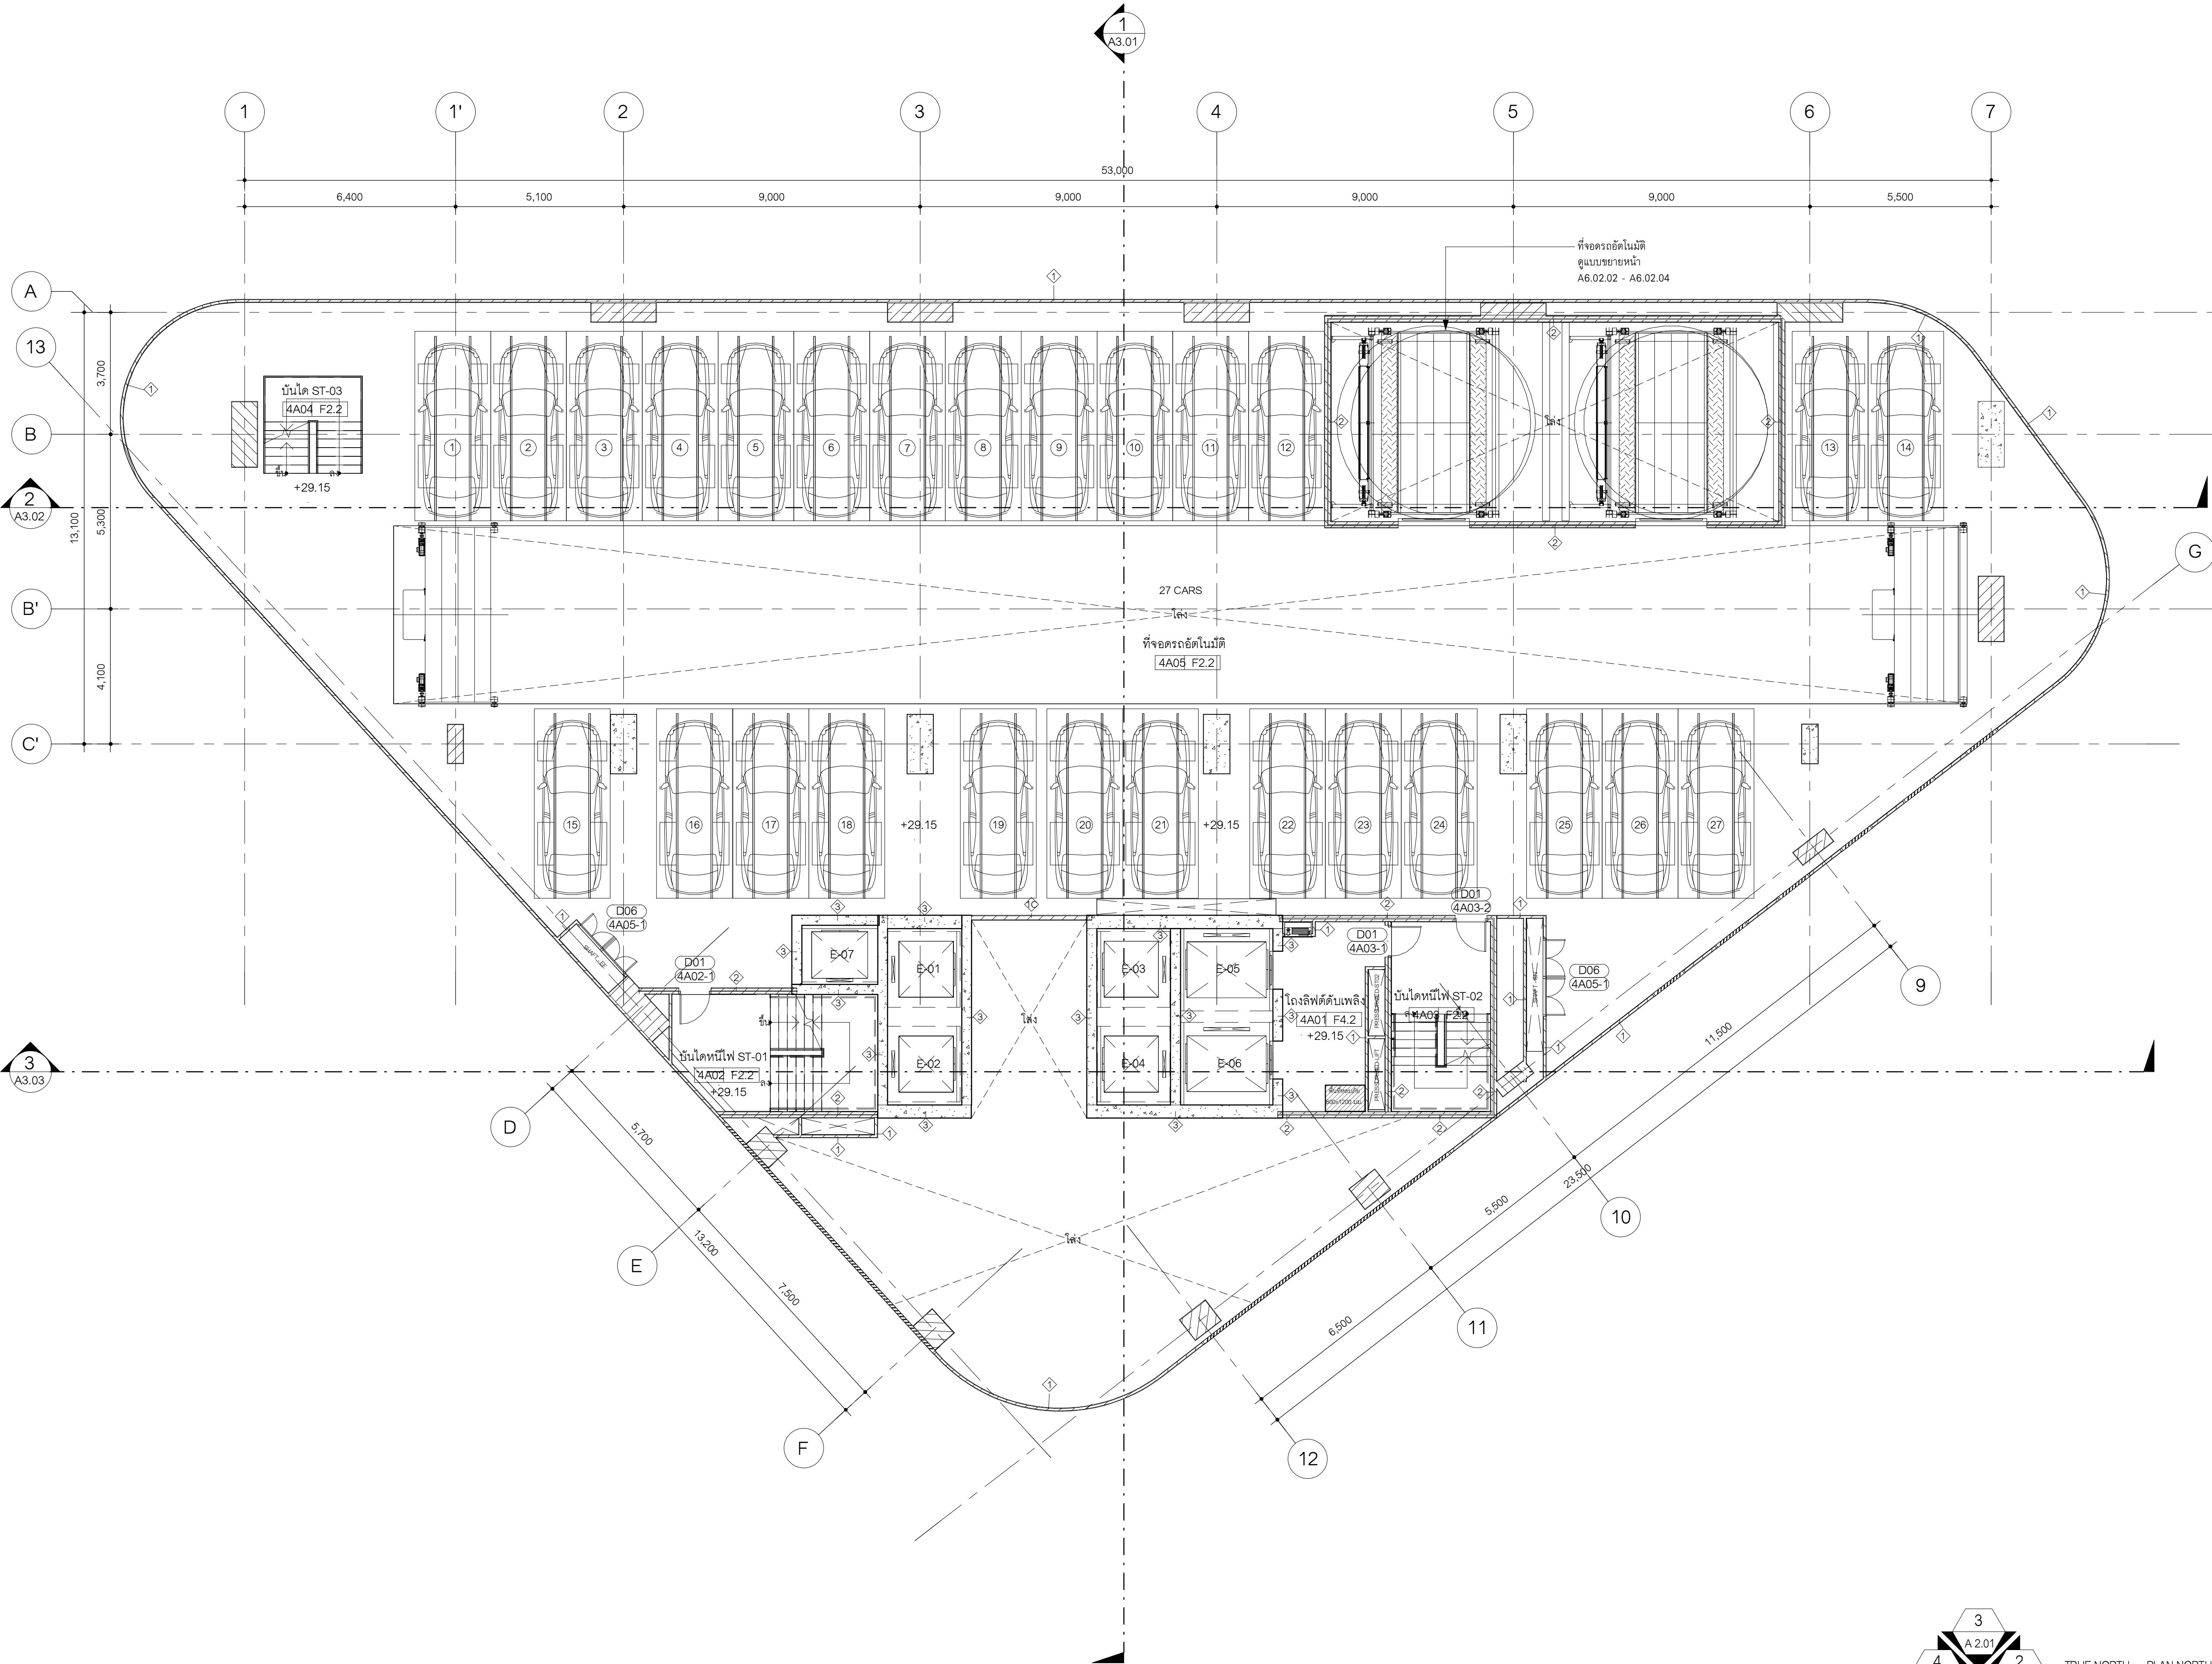

ผังพื้นที่ 4A
มาตราส่วน 1 : 100

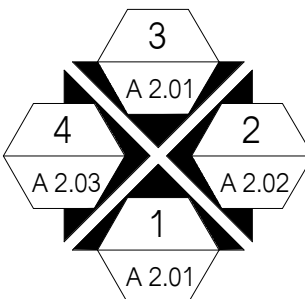

TRUE NORTH
PLAN NORTH

OWNER
LUXURY HOTEL DEVELOPMENT
SUKHUMVIT 38 CO., LTD.

DESIGNER
ARCHITECTS 49 LIMITED
81 SUKHUMVIT 26
BANGKOK 10110 THAILAND
T + 66 (0) 2260 4370
F + 66 (0) 2259 3872
E A49@A49.CO.TH
W A49.CO.TH

K.C.S. & ASSOCIATES CO. LTD.
22ND FLOOR, CHARN ISSARA TOWER II
2522/267 NEW PETCHABURI ROAD, BANGKAPI,
HUAY KWANG, BAKOK 10310 THAILAND
T +66 (0) 2308 2481 5
F +66 (0) 2308 2485

MEC PRO DESIGN CO. LTD.
567 BUILDING 4TH FLOOR, SUKUMVIT 38
SUAN LUANG, BANGKOK 10250 THAILAND
T +66 (0) 2170 8029
F +66 (0) 2170 8917
E MECPRO.DESIGN@GMAIL.COM

P.LANDSCAPE CO. LTD.
59/3 SUKHUMVIT 39, KLONLON NUA,
WATTANA, BANGKOK 10110 THAILAND
T (622) 261 3700 TO 9
F (622) 238 3388
E INFO@PLANDSCAPE.COM
W WWW.PLANDSCAPE.COM

ARCHITECTS
พริษฐ์ วงศ์โศภณรัตน์ วสท.509
เนรศักดิ์ อธิวิเศษ วสท.720
จารุวัฒน์ อธิวิเศษ วสท.769
พิชญพร อธิวิเศษ วสท.3432
สุภากร ศรีสมบุญ วสท.3347
ปวิศร์ จันทน์น้อย วสท.20910
ศรพร ศิริพาน วสท.23830
วรินทร์ พูลสวัสดิ์ วสท.27171

STRUCTURAL ENGINEER
กาญจนา จันทวงษ์ วสท.1023
กุลธิรา จันทวงษ์ สท.9572
ภาณุ สายรวมญาติ สท.15169
อภิสิทธิ์ สมอ้าง สท.69140

ELECTRICAL ENGINEER
ชานน นิ่มนง วท.1118
ชนัดดี พิศุสสง สท.1386
ชนวิวัฒน์ น้อยจ้อย วกท.63548

MECHANICAL ENGINEER
เบนต์ ไชยพงษ์ สท.3566
ณภัทร วิเชียรเทพาคุณ วก.51086
วิฑูรย์ บุญวิเศษ วก.52030

ENVIRONMENTAL ENGINEER
ทรงวุฒิ วิเศษศิลป์ สท.625
เบนต์ ไชยพงษ์ สท.112
วสุ ละลายบาลี วก.7507

SANITARY ENGINEER
ชื่อ นามสกุล เลขใบอนุญาต

LANDSCAPE ARCHITECT
นัทธกร รณศิริโนโจน สท.108

GENERAL NOTE
1. THIS DRAWING IS THE PROPERTY OF ARCHITECTS 49 LIMITED OR ONE OF ITS AFFILIATES. IT IS ISSUED SUBJECT TO RETURN UPON DEMAND AND IS NOT TO BE USED EXCEPT IN CONNECTION WITH THE PROJECT FOR WHICH IT IS INTENDED.
2. DO NOT SCALE THIS DRAWING. USE FIGURED DIMENSIONS ONLY.
ให้ใช้ค่าตัวเลขที่กำหนดไว้เท่านั้น ห้ามวัดจากแบบ

PROJECT NAME
THE OKURA PRESTIGE
SUKHUMVIT BANGKOK HOTEL
AND SPA


DRAWING TITLE
ผังพื้นที่ 5

ISSUE/REVISION
NO DESCRIPTION BY DATE
1 แบบแปลนอาคาร A49 17/04/2569


CHECK BY DRAWING NO.

ARCHITECT SIGNED
PM
PD
PA
JC

DRAWN BY Author SCALE: 1:100
PRINTED DATE 17/04/2569 REF. FILE

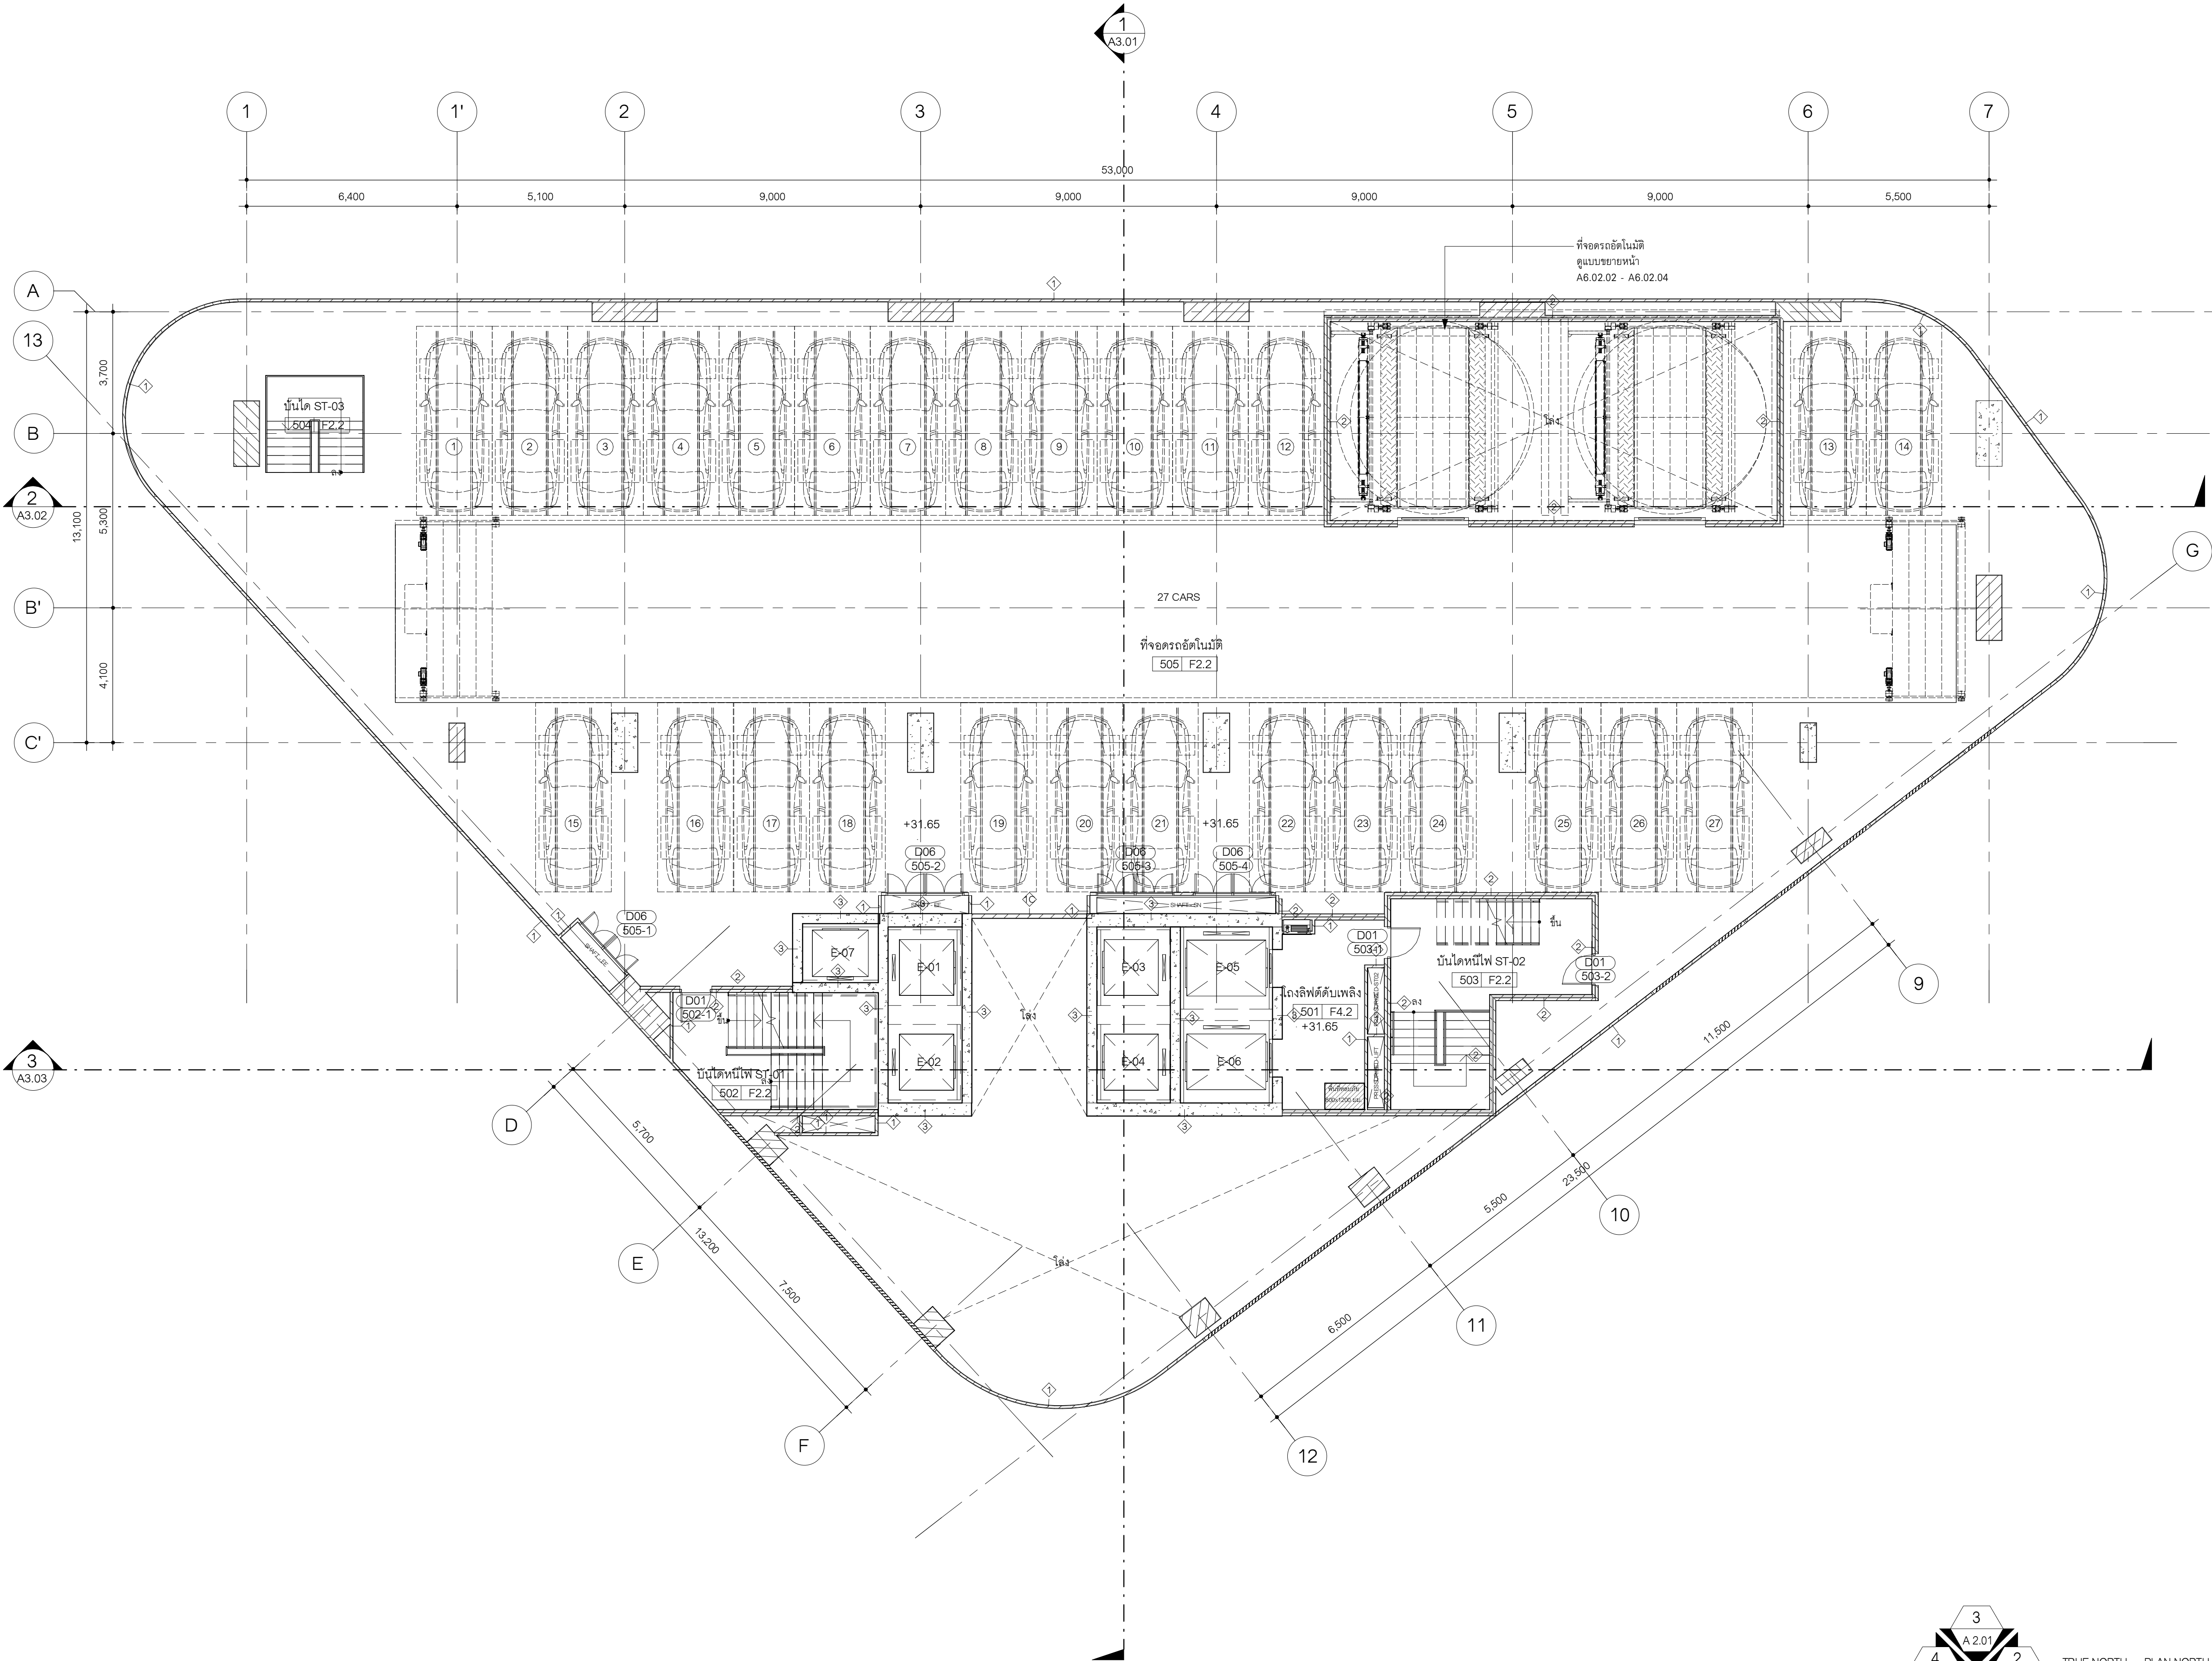

ผังพื้นที่ 5
มาตราส่วน 1 : 100

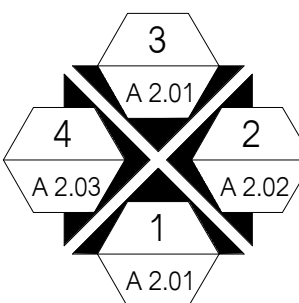

TRUE NORTH PLAN NORTH

OWNER
LUXURY HOTEL DEVELOPMENT
SUKHUMVIT 38 CO., LTD.

DESIGNER
ARCHITECTS 49 LIMITED
81 SUKHUMVIT 26
BANGKOK 10110 THAILAND
T + 66 (0) 2260 4370
F + 66 (0) 2259 3872
E A49@A49.CO.TH
W A49.CO.TH

K.C.S. & ASSOCIATES CO. LTD.
22ND FLOOR, CHARN ISSARA TOWER II
2522/267 NEW PETCHABURI ROAD, BANGKAPI,
HUAY KWANG, BANGKOK 10310 THAILAND
T +66 (0) 2308 2481 5
F +66 (0) 2308 2485

MEC PRO DESIGN CO. LTD.
567 BUILDING 4TH FLOOR, SUAN LUANG, BANGKOK 10250 THAILAND
T +66 (0) 270 8029
F (02) 238 3388
E INFO@PLANDSCAPE.COM
W WWW.PLANDSCAPE.COM

P.LANDSCAPE CO. LTD.
59/3 SUKHUMVIT 39, KLONGTON NUA,
WATTANA, BANGKOK 10110 THAILAND
T (622) 261 3700 TO 9
F (622) 238 3388
E INFO@PLANDSCAPE.COM
W WWW.PLANDSCAPE.COM

ARCHITECTS
ที่ปรึกษา วรวิทย์ วรวิทย์ วรวิทย์ 509
นางสาววิทย์ อธิวิทย์ วรวิทย์ 720
นางสาววิทย์ อธิวิทย์ วรวิทย์ 769
ที่ปรึกษา อธิวิทย์ วรวิทย์ 3432
สถาปนิก อธิวิทย์ วรวิทย์ 3347
สถาปนิก อธิวิทย์ วรวิทย์ 20910
สถาปนิก อธิวิทย์ วรวิทย์ 23830
สถาปนิก อธิวิทย์ วรวิทย์ 27171

STRUCTURAL ENGINEER
นายวิชาญ จันทวงษ์ วรวิทย์ 1023
นายวิชาญ จันทวงษ์ วรวิทย์ 9572
นายวิชาญ จันทวงษ์ วรวิทย์ 15169
นายวิชาญ จันทวงษ์ วรวิทย์ 69140

ELECTRICAL ENGINEER
นายวิชาญ จันทวงษ์ วรวิทย์ 1118
นายวิชาญ จันทวงษ์ วรวิทย์ 15186
นายวิชาญ จันทวงษ์ วรวิทย์ 63548

MECHANICAL ENGINEER
นายวิชาญ จันทวงษ์ วรวิทย์ 3566
นายวิชาญ จันทวงษ์ วรวิทย์ 51088
นายวิชาญ จันทวงษ์ วรวิทย์ 52030

ENVIRONMENTAL ENGINEER
นางวิชาญ จันทวงษ์ วรวิทย์ 625
นายวิชาญ จันทวงษ์ วรวิทย์ 112
นายวิชาญ จันทวงษ์ วรวิทย์ 7507

SANITARY ENGINEER
นายวิชาญ จันทวงษ์ วรวิทย์ 108

LANDSCAPE ARCHITECT
นายวิชาญ จันทวงษ์ วรวิทย์ 108

GENERAL NOTE
1. THIS DRAWING IS THE PROPERTY OF ARCHITECTS 49 LIMITED OR ONE OF ITS AFFILIATES. IT IS ISSUED SUBJECT TO RETURN UPON DEMAND AND IS NOT TO BE USED EXCEPT IN CONNECTION WITH THE PROJECT FOR WHICH IT IS INTENDED.
2. DO NOT SCALE THIS DRAWING. USE FIGURED DIMENSIONS ONLY.
3. DO NOT SCALE THIS DRAWING. USE FIGURED DIMENSIONS ONLY.

PROJECT NAME
THE OKURA PRESTIGE
SUKHUMVIT BANGKOK HOTEL
AND SPA


DRAWING TITLE
ผังพื้นที่ 6 (BALLROOM)

ISSUE/REVISION
NO DESCRIPTION BY DATE
1 แก้ไขแบบแปลน A49 17/04/2569


CHECK BY DRAWING NO.

ARCHITECT SIGNED
PM
PD
PA
JC

DRAWN BY Author SCALE: 1:100
PRINTED DATE 17/04/2569 REF. FILE

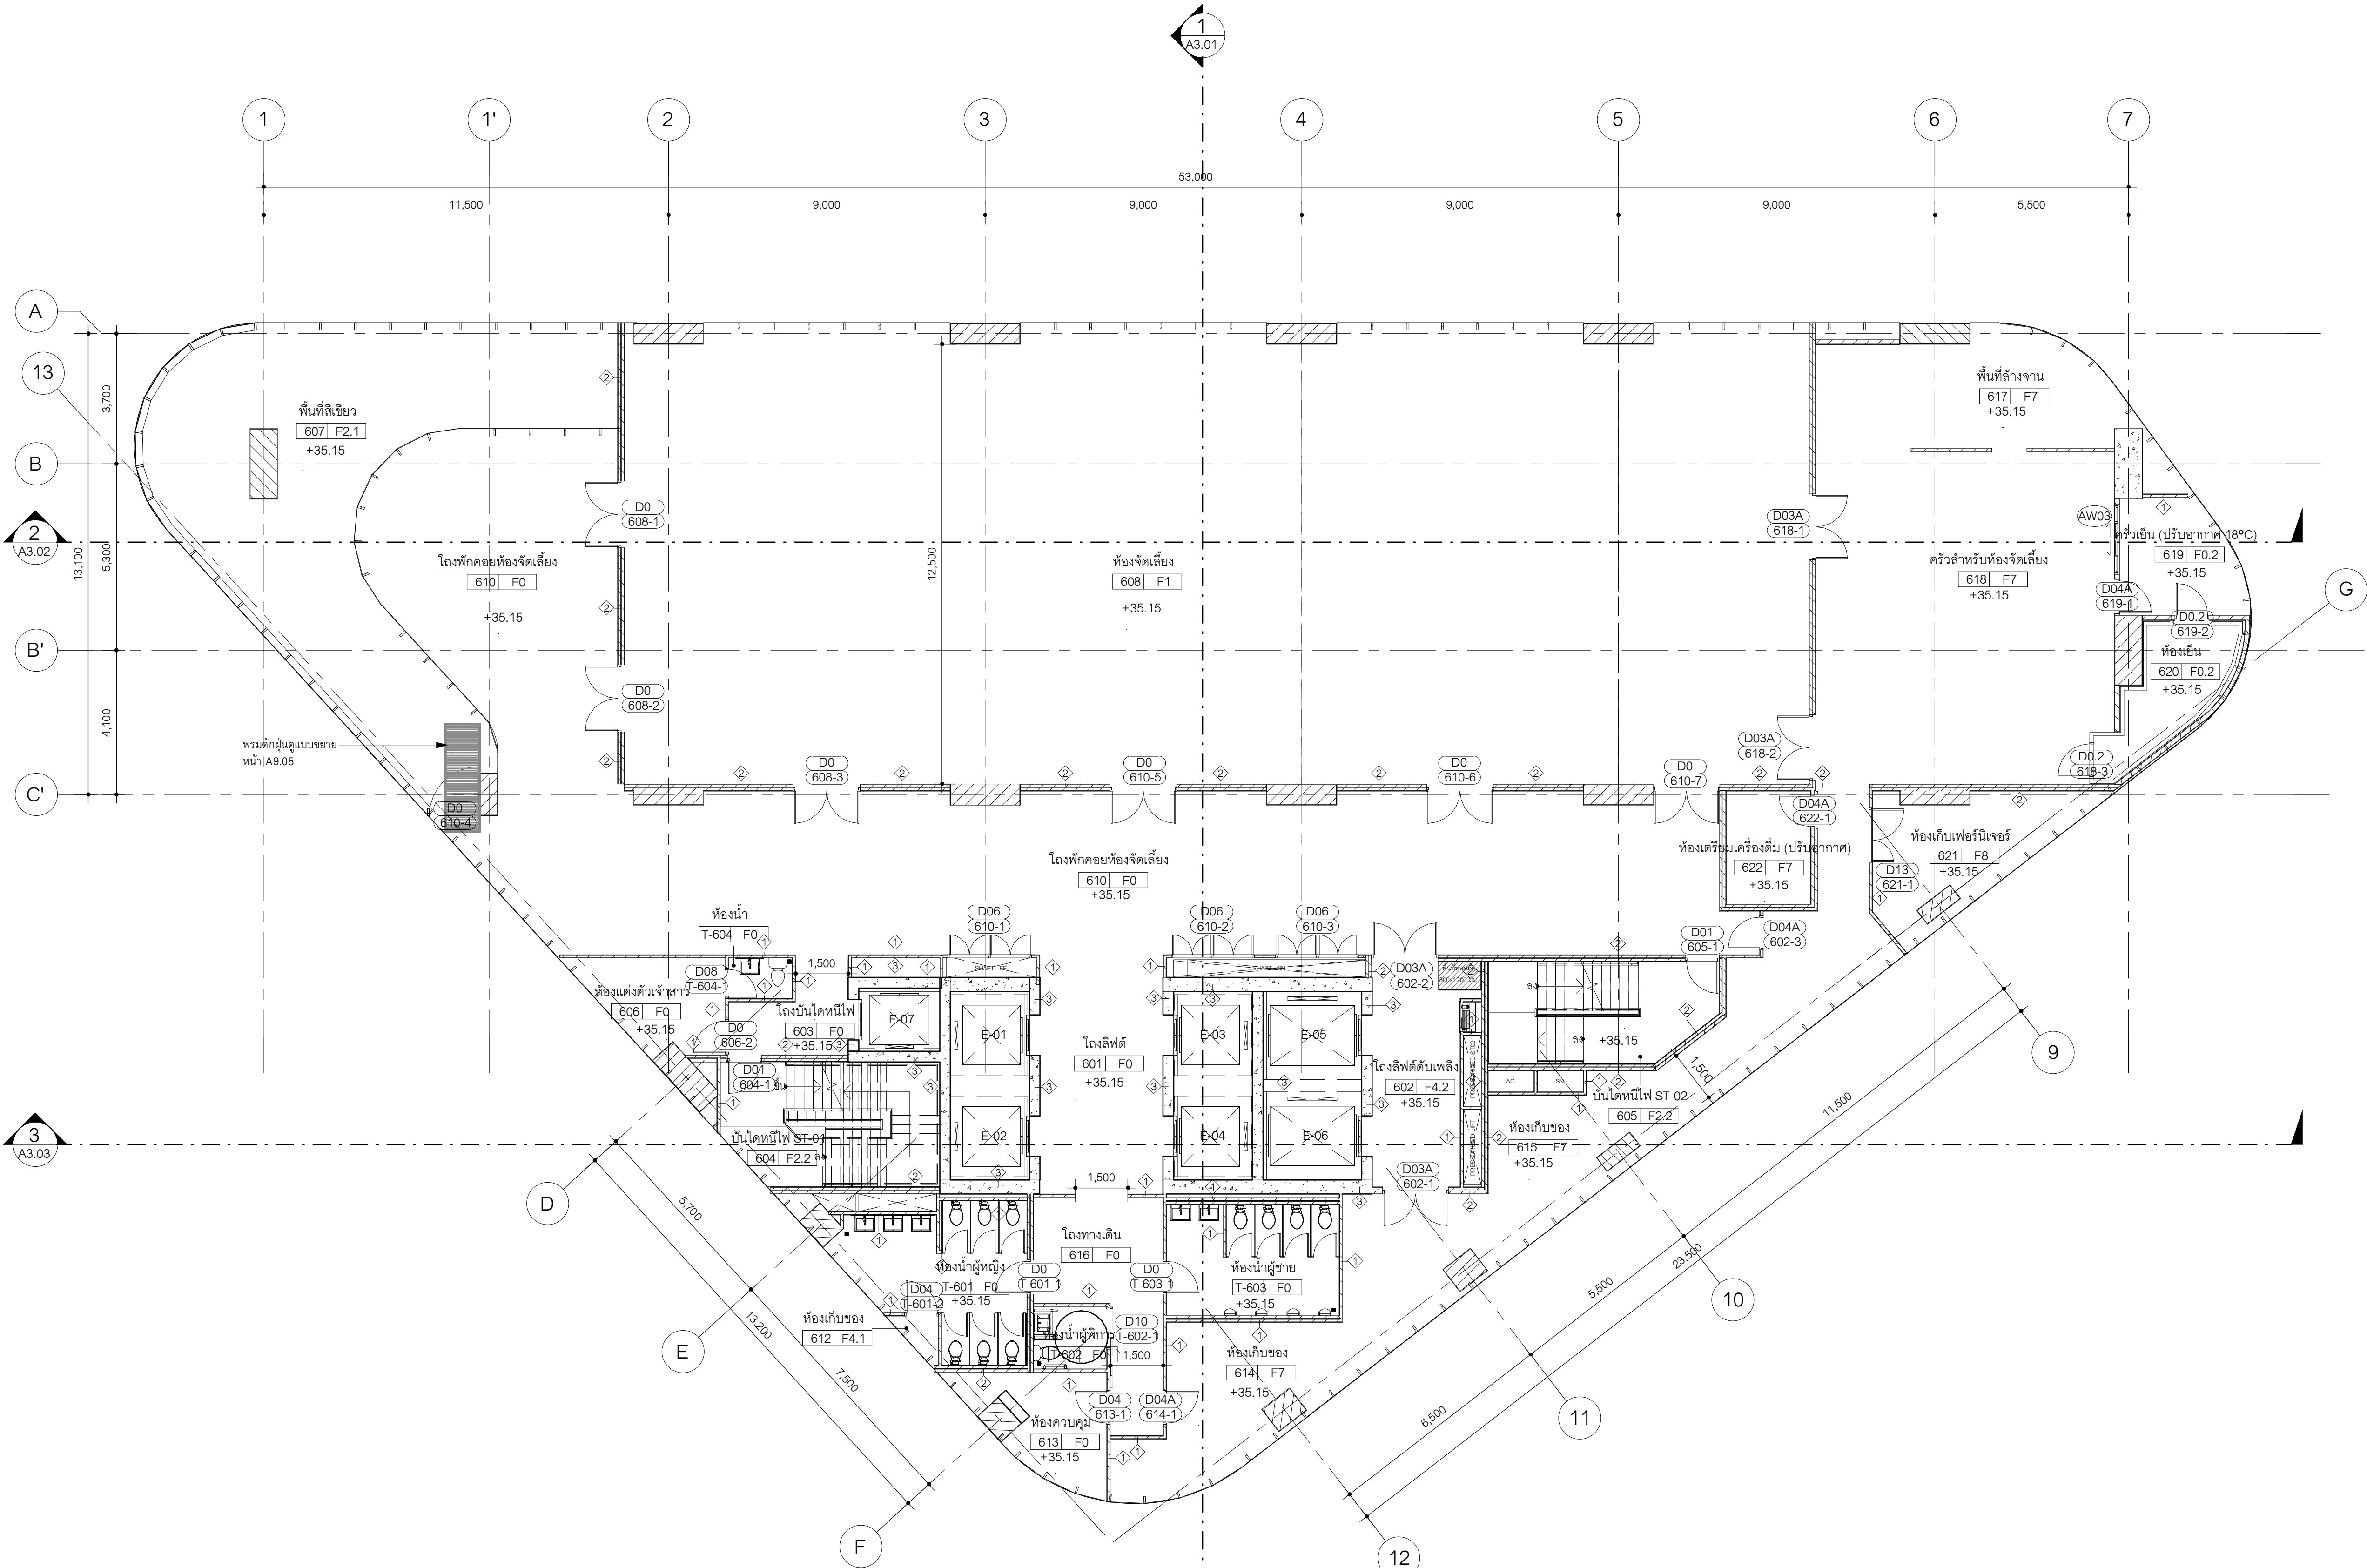

ผังพื้นที่ 6 (BALLROOM)
มาตราส่วน 1:100

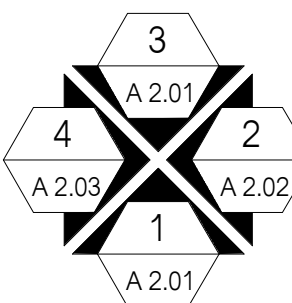

TRUE NORTH PLAN NORTH

OWNER
LUXURY HOTEL DEVELOPMENT
SUKHUMVIT 38 CO., LTD.

DESIGNER
ARCHITECTS 49 LIMITED
81 SUKHUMVIT 26
BANGKOK 10110 THAILAND
T + 66 (0) 2260 4370
F + 66 (0) 2259 3872
E A49@A49.CO.TH
W A49.CO.TH

K.C.S. & ASSOCIATES CO. LTD.
22ND FLOOR, CHARN ISSARA TOWER II
2592/267 NEW PETCHABURI ROAD, BANGKAPI,
HUAY KWANG, BANGKOK 10310 THAILAND
T +66 (0) 2308 2481 5
F +66 (0) 2308 2485

MEC PRO DESIGN CO. LTD.
567 BUILDING 4TH FLOOR SUKUMVIT 38
SUAN LUANG, BANGKOK 10250 THAILAND
T +66 (0) 2170 8029
F +66 (0) 37 034 8917
E MECPRO.DESIGN@GMAIL.COM

P.LANDSCAPE CO. LTD.
59/3 SUKHUMVIT 39, KLINGTON NUA,
WATTANA, BANGKOK 10110 THAILAND
T (622) 251 3700 TO 9
F (622) 238 3388
E INFO@PLANDSCAPE.COM
W WWW.PLANDSCAPE.COM

ARCHITECTS
พิธีชัย วงศ์วิเศษวรรณ วสท.509
ณัฏฐพร อธิวิเศษ วสท.720
จารุวัฒน์ อธิวิเศษ วสท.769
พิณพร อธิวิเศษ วสท.3432
สุภากร ศรีสมบูรณ์ วสท.3347
ปวิศร์ หิวนนไวย วสท.20910
ศรพร ศิริพาน วสท.23830
วันธรณ์ พูลสวัสดิ์ วสท.27171

STRUCTURAL ENGINEER
ภาณุ จันทวงศ วส.1023
ภูสิริ จันทวงศ สบ.9572
ภาณุ สายรวมญาติ สบ.15169
อภิสิทธิ์ สมอียง กบ.69140

ELECTRICAL ENGINEER
ชาน นิ่มตรง วท.1118
พนศักดิ์ พงษ์พานิช สท.1386
ธนวัฒน์ น้อยจ้อย กทท.63548

MECHANICAL ENGINEER
ณเดช ไชยพงษ์ สท.3566
ณภัทร วิเชียรพทยาคม กท.51088
วิฑกร์ บุญโคตร กท.52030

ENVIRONMENTAL ENGINEER
ทรงวุฒิ วิเศษศิลป์ สท.625
ณเดช ไชยพงษ์ กท.112
วสุ สละยาบป กท.7507

SANITARY ENGINEER
ช่อ นามสกุล เสกโชษณูชาติ

LANDSCAPE ARCHITECT
นัทธกร รณศิริโนโจน สท.108

GENERAL NOTE
1. THIS DRAWING IS THE PROPERTY OF ARCHITECTS 49 LIMITED OR ONE OF ITS AFFILIATES. IT IS ISSUED SUBJECT TO RETURN UPON DEMAND AND IS NOT TO BE USED EXCEPT IN CONNECTION WITH THE PROJECT FOR WHICH IT IS INTENDED.
2. DO NOT SCALE THIS DRAWING. USE FIGURED DIMENSIONS ONLY.
ให้ใช้ค่าเลขที่กำกับไว้เท่านั้น ห้ามวัดจากแบบ

PROJECT NAME
THE OKURA PRESTIGE
SUKHUMVIT BANGKOK HOTEL
AND SPA


DRAWING TITLE
ผังพื้นที่ 6A

ISSUE/REVISION
NO DESCRIPTION BY DATE
1 แบบแปลนอาคาร A49 17/04/2569


CHECK BY
ARCHITECT SIGNED
PD
PA
JC
DRAWN BY Author SCALE: 1:100
PRINTED DATE 17/04/2569 REF. FILE

DRAWING NO.

A1.16

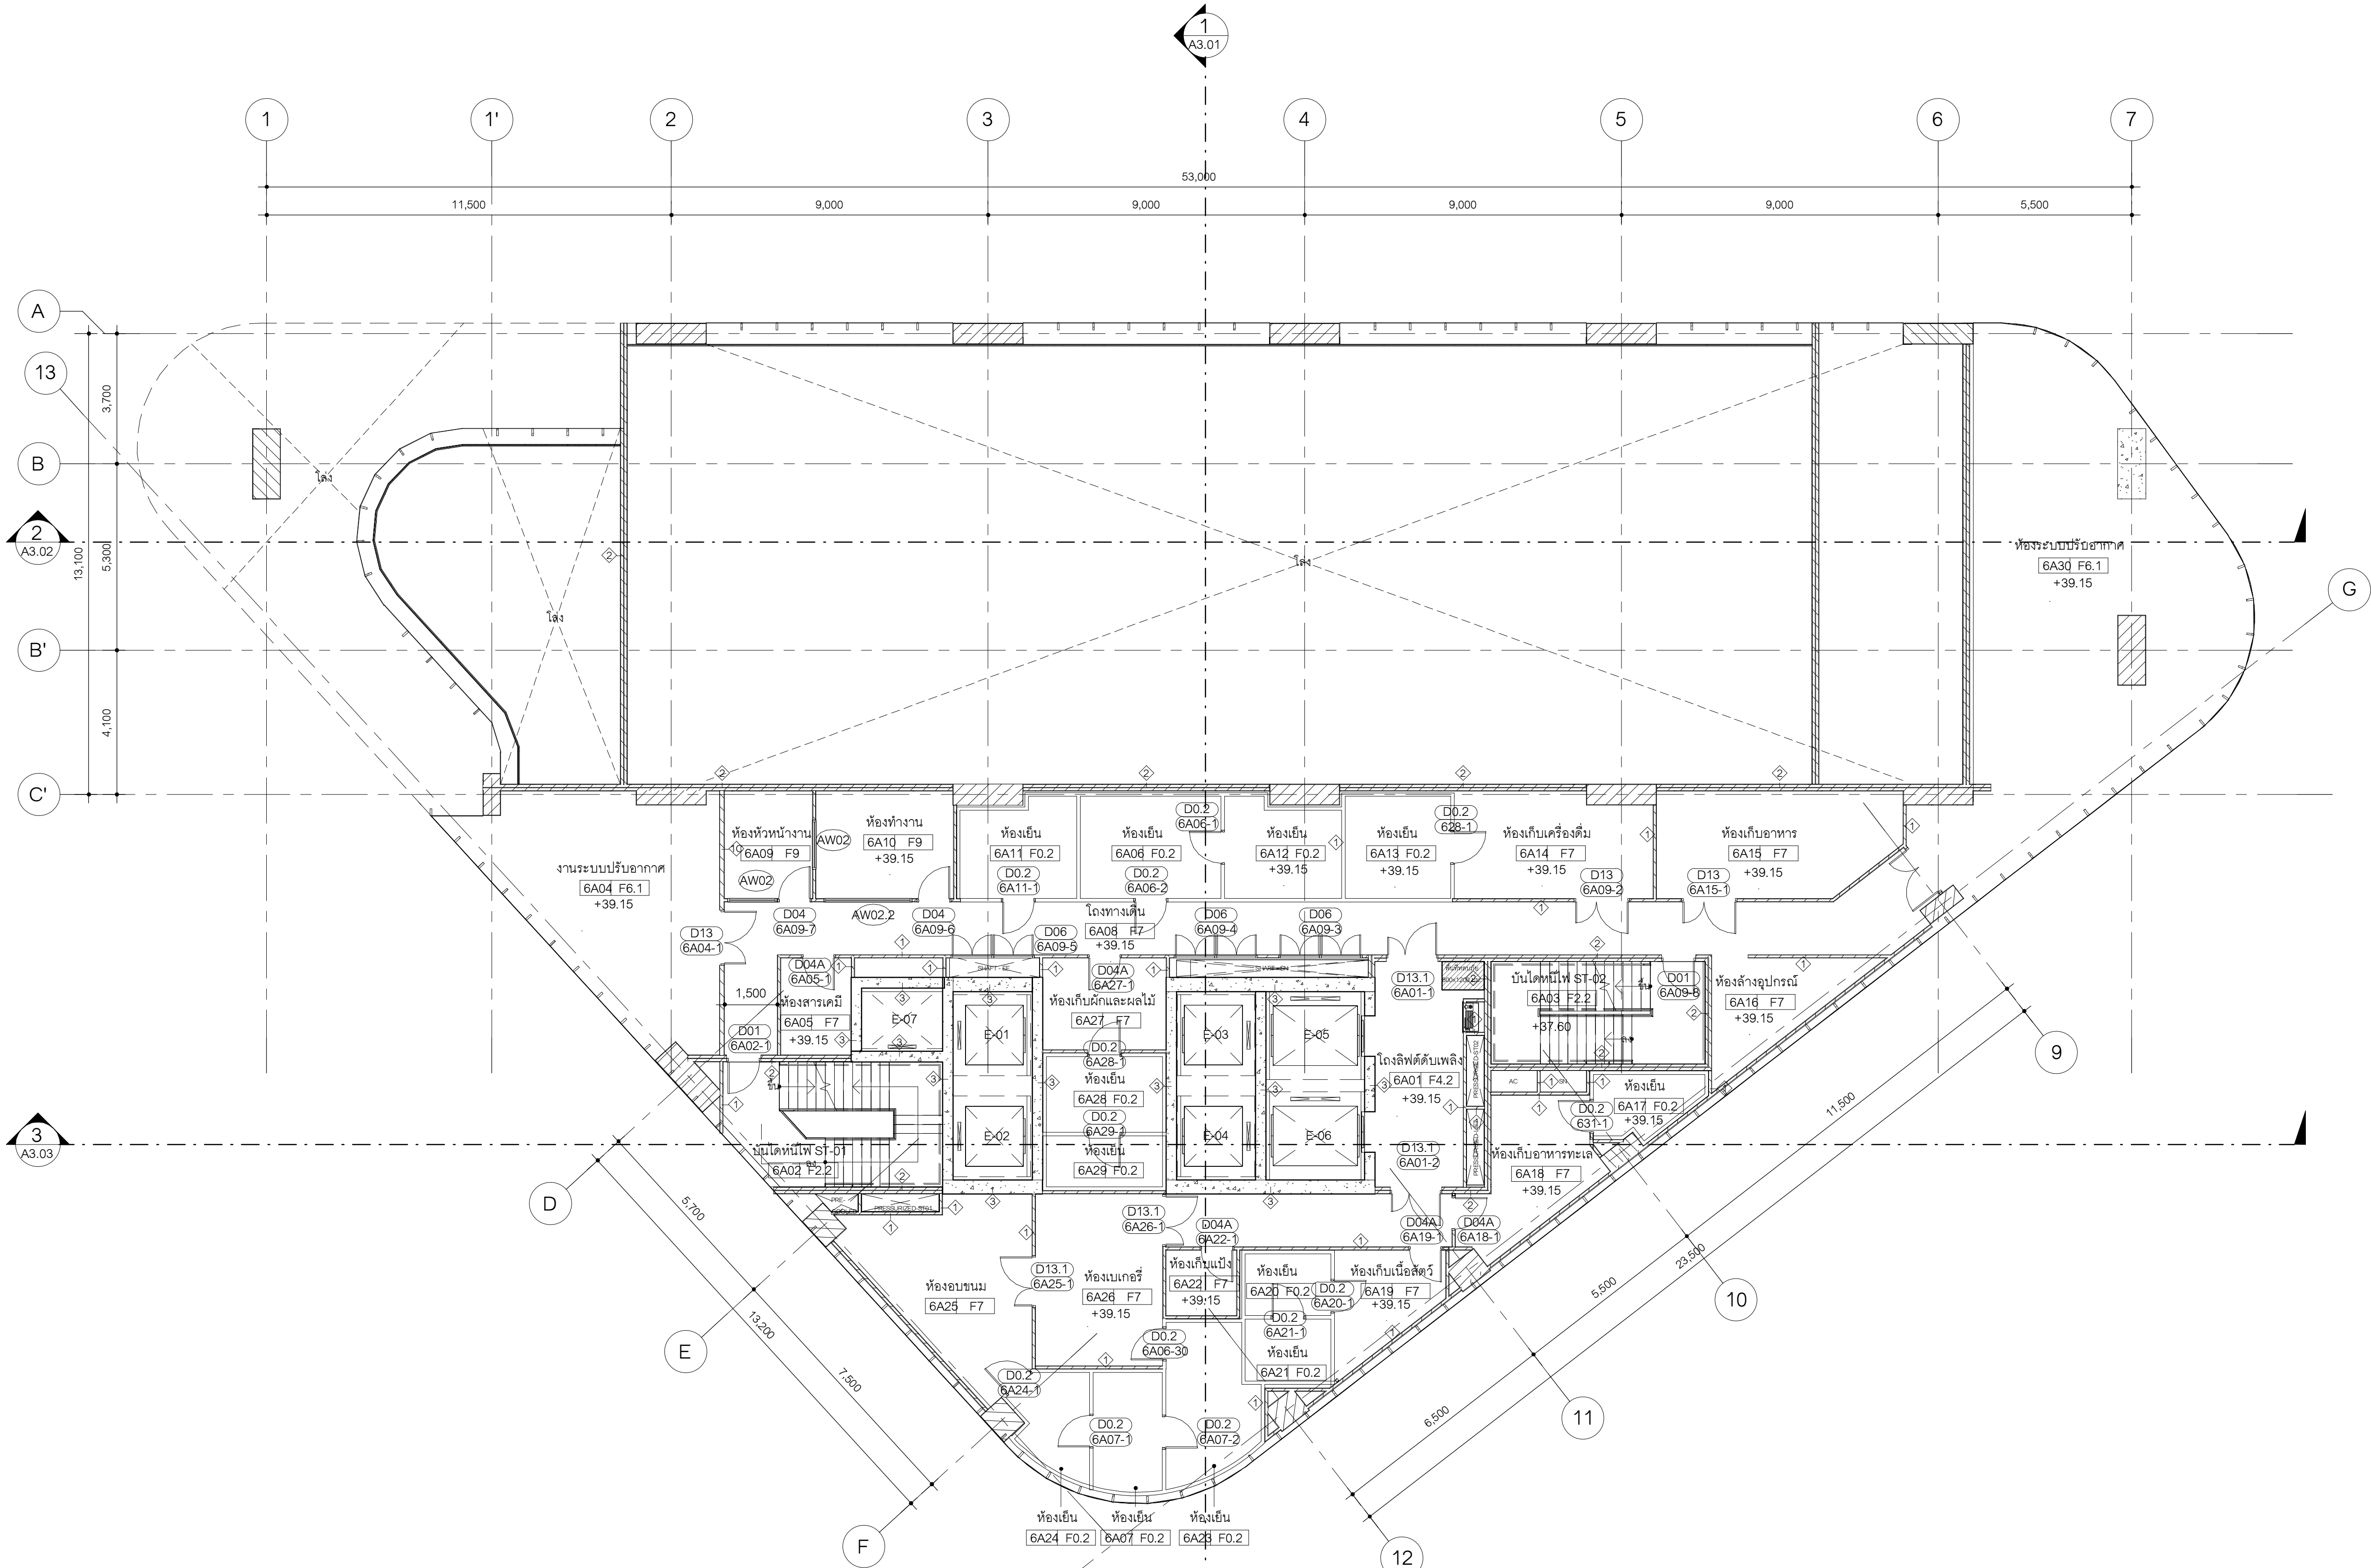

ผังพื้นที่ 6A
มาตราส่วน 1:100

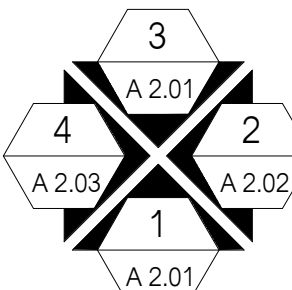

TRUE NORTH
PLAN NORTH

OWNER
LUXURY HOTEL DEVELOPMENT
SUKHUMVIT 38 CO., LTD.

DESIGNER
ARCHITECTS 49 LIMITED
81 SUKHUMVIT 26
BANGKOK 10110 THAILAND
T + 66 (0) 2260 4370
F + 66 (0) 2259 3872
E A49@A49.CO.TH
W A49.CO.TH

K.C.S. & ASSOCIATES CO. LTD.
22ND FLOOR, CHARN ISSARA TOWER II
2522/267 NEW PETCHABURI ROAD, BANGKAPI,
HUAY KWANG, BAKOK 10310 THAILAND
T + 66 (0) 2308 2481 5
F + 66 (0) 2308 2485

MEC PRO DESIGN CO. LTD.
567 BUILDING 4TH FLOOR, SUKUMVIT 38
SUAN LUANG, BANGKOK 10250 THAILAND
T + 66 (0) 2170 8029
F + 66 (0) 37 034 8917
E MECPRO.DESIGN@GMAIL.COM

P.LANDSCAPE CO. LTD.
59/3 SUKHUMVIT 39, KLONGTON NUA,
WATTANA, BANGKOK 10110 THAILAND
T (622) 261 3700 TO 9
F (622) 258 3388
E INFO@PLANDSCAPE.COM
W WWW.PLANDSCAPE.COM

ARCHITECTS
พริษฐ์ วงศ์วิเศษวรรณ วสท.509
เนตรศศิธร อธิวิเศษ วสท.720
จารุวิมล อธิวิเศษ วสท.769
พริษฐ์ อธิวิเศษ วสท.3432
สุภากร ศรีสมบุญ วสท.3347
ปรีดี ตันนันทน์ วสท.20910
ศรพร ศิริพันธ์ วสท.23830
วริศรา นิลสวัสดิ์ วสท.27171

STRUCTURAL ENGINEER
กาญจนา จันทวงษ์ วบ.1023
ภูริศ จันทวงษ์ สบ.9572
ภาณุ สายรวมญาติ สบ.15169
อภิสิทธิ์ สมอ้ง กบ.69140

ELECTRICAL ENGINEER
ชาน นิลเดช วท.1118
ชนัดดา พิศุสสง วท.1586
ชนัดดา นิลเดช วท.63548

MECHANICAL ENGINEER
เบน ไซมอน สท.3566
ณัฏฐา วิเชียรพทยาคม กท.51086
วิภากร บุญนิยม กท.52030

ENVIRONMENTAL ENGINEER
ทรงวุฒิ วิเศษศิลป์ สท.625
เบน ไซมอน สท.112
วสุ สดายุบป สท.7507

SANITARY ENGINEER
ชื่อ นามสกุล เลขใบอนุญาต

LANDSCAPE ARCHITECT
นัทธ วรรณสินใจ สท.108

GENERAL NOTE
1. THIS DRAWING IS THE PROPERTY OF ARCHITECTS 49 LIMITED OR ONE OF ITS AFFILIATES. IT IS ISSUED SUBJECT TO RETURN UPON DEMAND AND IS NOT TO BE USED EXCEPT IN CONNECTION WITH THE PROJECT FOR WHICH IT IS INTENDED.
2. DO NOT SCALE THIS DRAWING. USE FIGURED DIMENSIONS ONLY.
ให้ใช้ค่าเลขที่กำกับไว้เท่านั้น ห้ามวัดจากแบบ

PROJECT NAME
THE OKURA PRESTIGE
SUKHUMVIT BANGKOK HOTEL
AND SPA


DRAWING TITLE
ผังพื้นที่ 7

NO	DESCRIPTION	BY	DATE
1	แบบแปลนอาคาร	A49	17/04/2569



CHECK BY
ARCHITECT SIGNED

DRAWING NO.
A1.17

DRAWN BY Author
PRINTED DATE 17/04/2569
SCALE: 1:100
REF. FILE

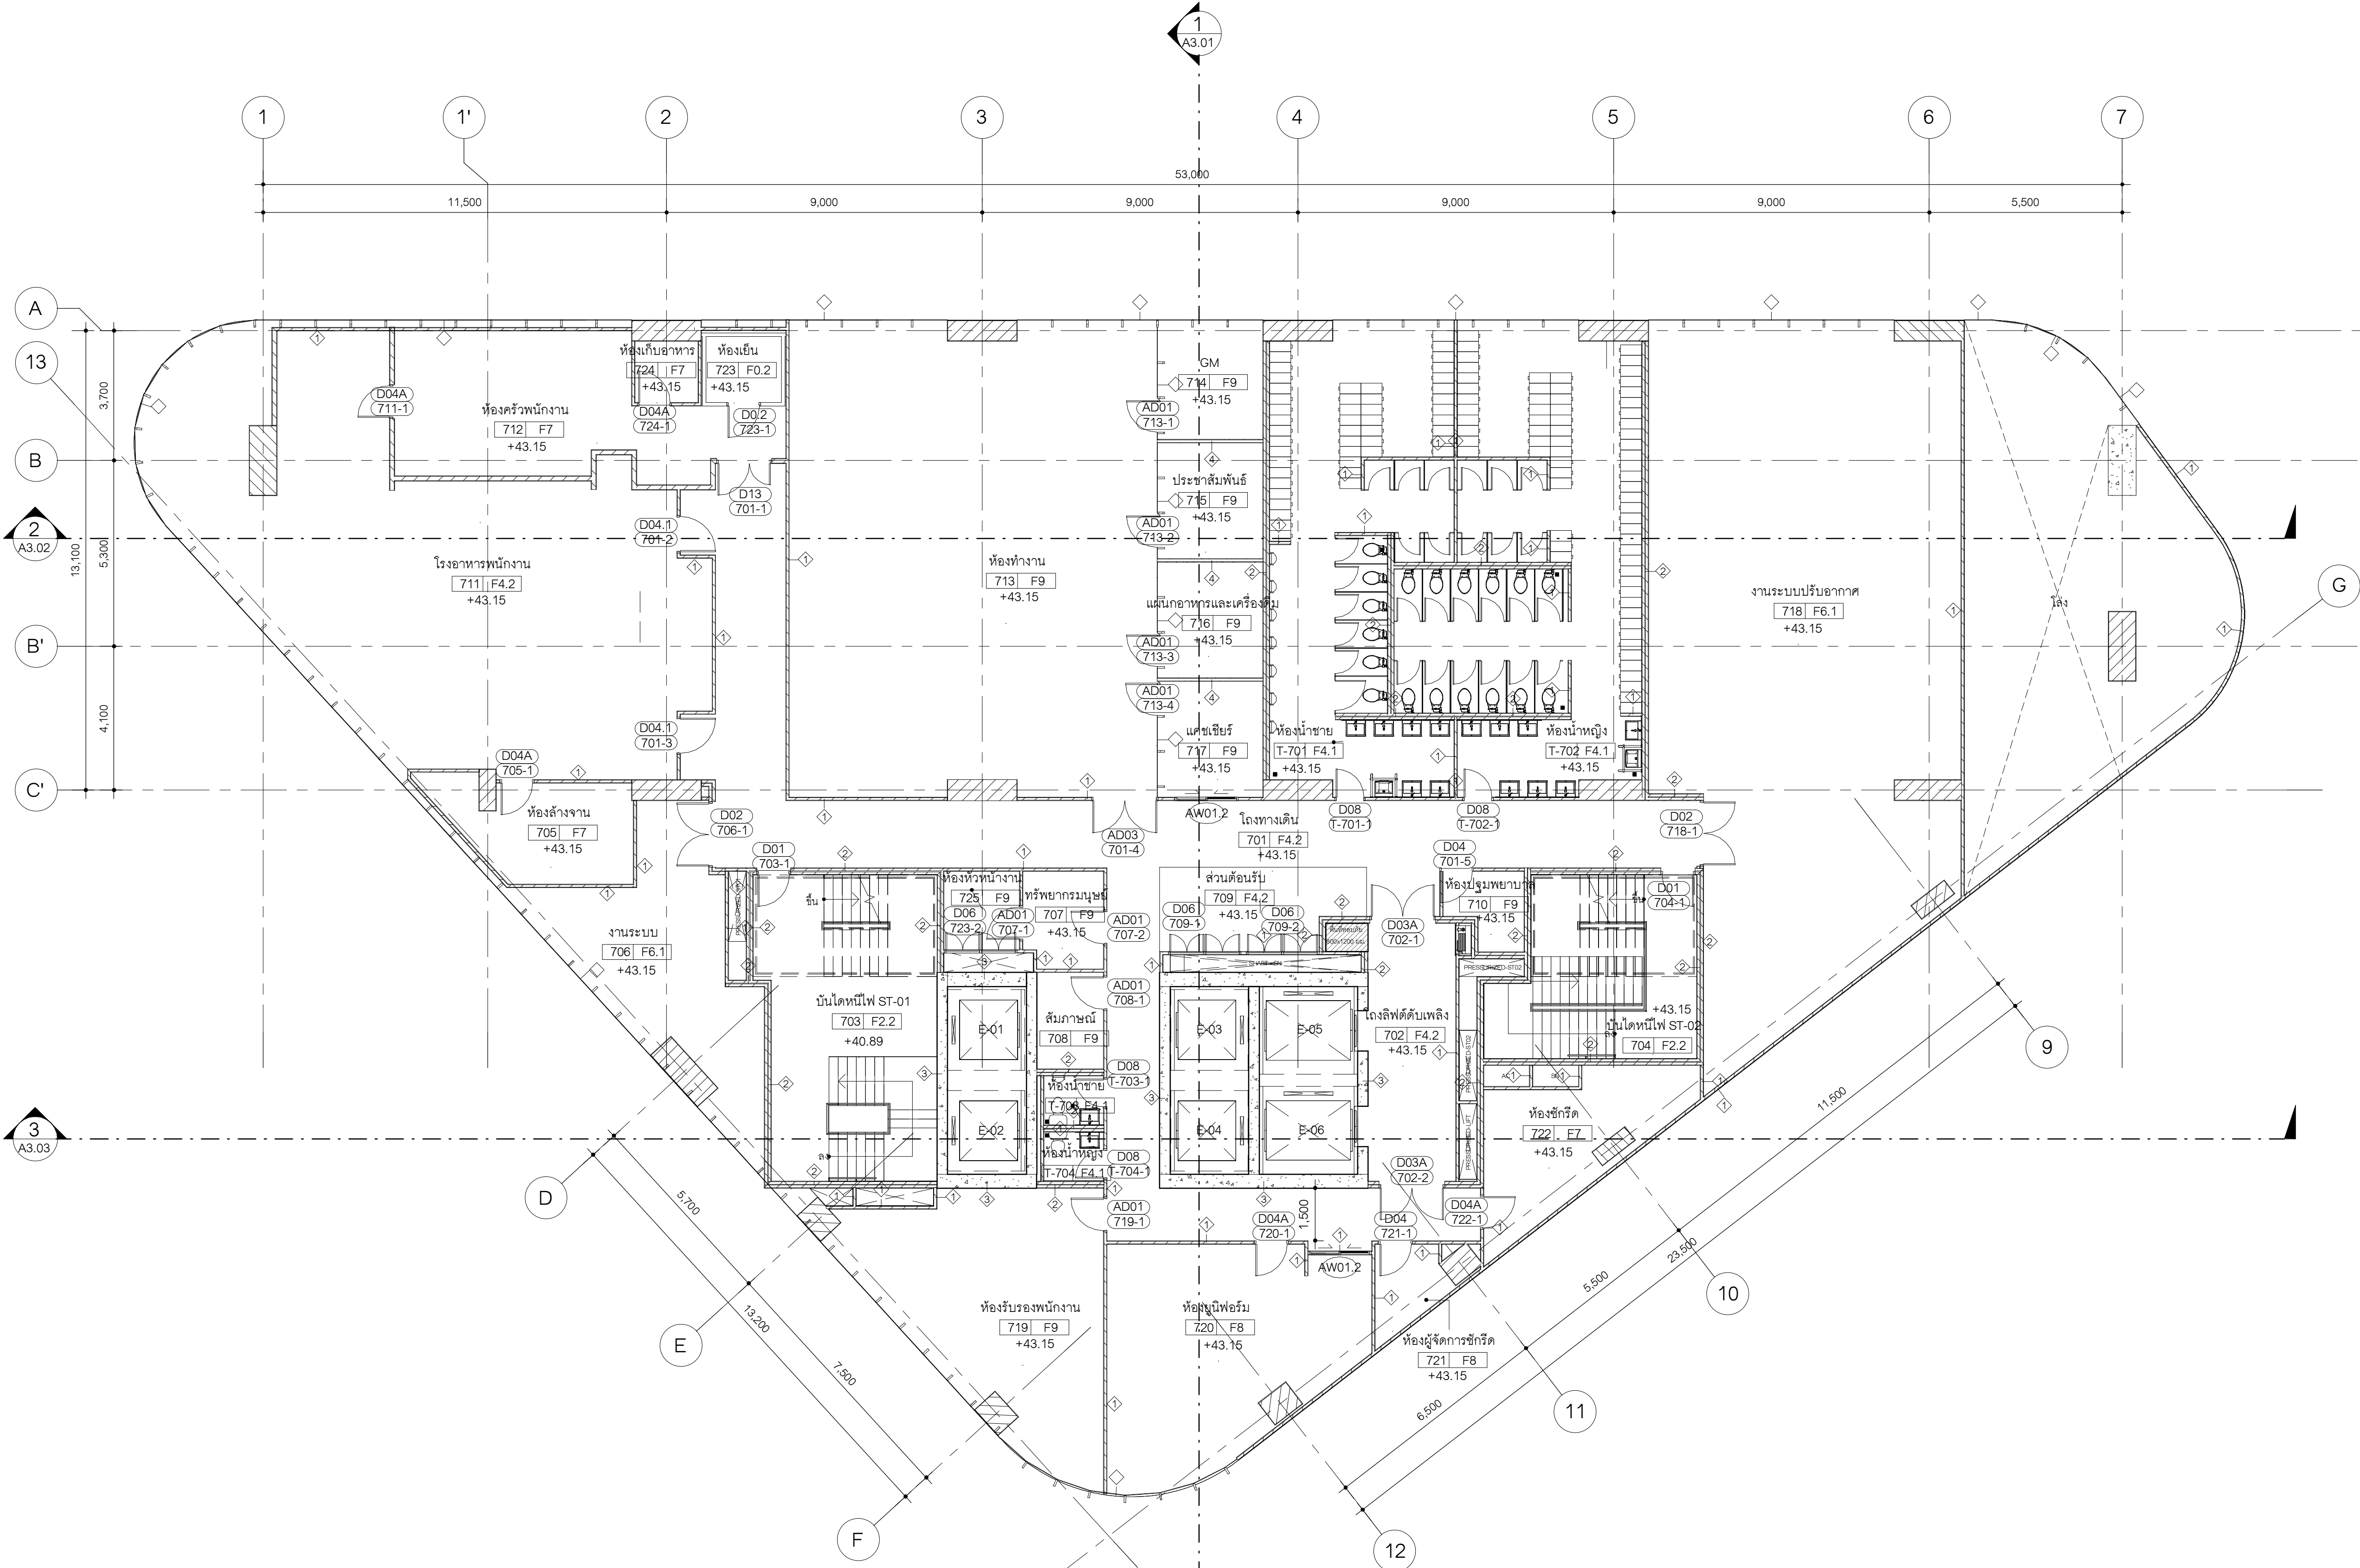

ผังพื้นที่ 7
มาตราส่วน 1 : 100

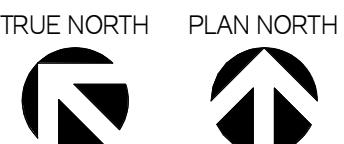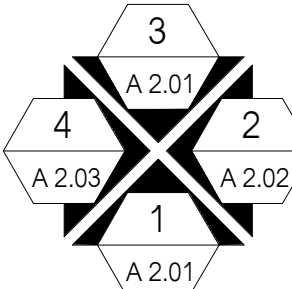

OWNER
LUXURY HOTEL DEVELOPMENT
SUKHUMVIT 38 CO., LTD.

DESIGNER
ARCHITECTS 49 LIMITED
81 SUKHUMVIT 26
BANGKOK 10110 THAILAND
T + 66 (0) 2260 4370
F + 66 (0) 2259 3872
E A49@A49.CO.TH
W A49.CO.TH

K.C.S. & ASSOCIATES CO. LTD.
22ND FLOOR, CHARN ISSARA TOWER II
2522/267 NEW PETCHABURI ROAD, BANGKAPI,
HUAY KWANG, BANGKOK 10310 THAILAND
T +66 (0) 2308 2481 5
F +66 (0) 2308 2485

MEC PRO DESIGN CO. LTD.
567 BUILDING 4TH FLOOR SUKUMVIT 38
SUAN LUANG, BANGKOK 10250 THAILAND
T +66 (0) 2170 8029
+66 (0) 97 034 8917
E MECPRO.DESIGN@GMAIL.COM

P LANDSCAPE CO. LTD.
59/3 SUKHUMVIT 39, KLONTON NUA,
WATTANA, BANGKOK 10110 THAILAND
T (622) 261 3700 TO 9
F (622) 238 3388
E INFO@PLANDSCAPE.COM
W WWW.PLANDSCAPE.COM

ARCHITECTS
ที่ปรึกษา วรวิทย์วรรณ วรณ.509
เนรมิตวิทย์ อธิวิตร วรณ.720
จารุวิมล อธิวิตร วรณ.769
พิชญพร อธิวิตร วรณ.3432
สุภากร ศรีสมบุญ วรณ.3347
ปาริชาติ หิมนันนัย วรณ.20910
ศรพร ศิริพาน วรณ.23830
วริษรณ พูลสวัสดิ์ วรณ.27171

STRUCTURAL ENGINEER
การบัญชี จันทราวุธ วร.1023
ภูริสร์ จันทราวุธ สบ.9572
ภาสกร สายรวมญาติ สบ.15169
อภิสิทธิ์ สมอียง สบ.69140

ELECTRICAL ENGINEER
ชานน นิมิตกร วรณ.1118
ธนศักดิ์ พิชัยสุข สบ.1586
ธนวัฒน์ น้อยจ้อย ภาท.63548

MECHANICAL ENGINEER
เบนซ์ ไชยพงษ์ สบ.3566
ณภัทร วิเชียรเมทขาน ภา.51088
วิภากร บุญนิยม ภา.52030

ENVIRONMENTAL ENGINEER
ทรงวุฒิ วิเศษศิลป์ สบ.625
เบนซ์ ไชยพงษ์ สบ.112
วสุ ลดาชัย ภา.7507

SANITARY ENGINEER
ชื่อ นามสกุล เลขใบอนุญาต

LANDSCAPE ARCHITECT
นัทธกร รณชัยโน้มน สบ.108

GENERAL NOTE
1. THIS DRAWING IS THE PROPERTY OF ARCHITECTS 49 LIMITED OR ONE OF ITS AFFILIATES. IT IS ISSUED SUBJECT TO RETURN UPON DEMAND AND IS NOT TO BE USED EXCEPT IN CONNECTION WITH THE PROJECT FOR WHICH IT IS INTENDED.
2. DO NOT SCALE THIS DRAWING. USE FIGURED DIMENSIONS ONLY.
ให้ใช้ค่าตัวเลขที่กำหนดไว้เท่านั้น ห้ามวัดจากแบบ

PROJECT NAME
THE OKURA PRESTIGE
SUKHUMVIT BANGKOK HOTEL
AND SPA


DRAWING TITLE
ผังพื้นที่ 8 (GUESTROOM)

ISSUE/REVISION
NO DESCRIPTION BY DATE
1 แบบแปลนสถาปัตย์ A49 17/04/2569


CHECK BY
ARCHITECT SIGNED
PD
PA
JC
DRAWN BY Author SCALE: 1:100
PRINTED DATE 17/04/2569 REF. FILE

DRAWING NO.

A1.18

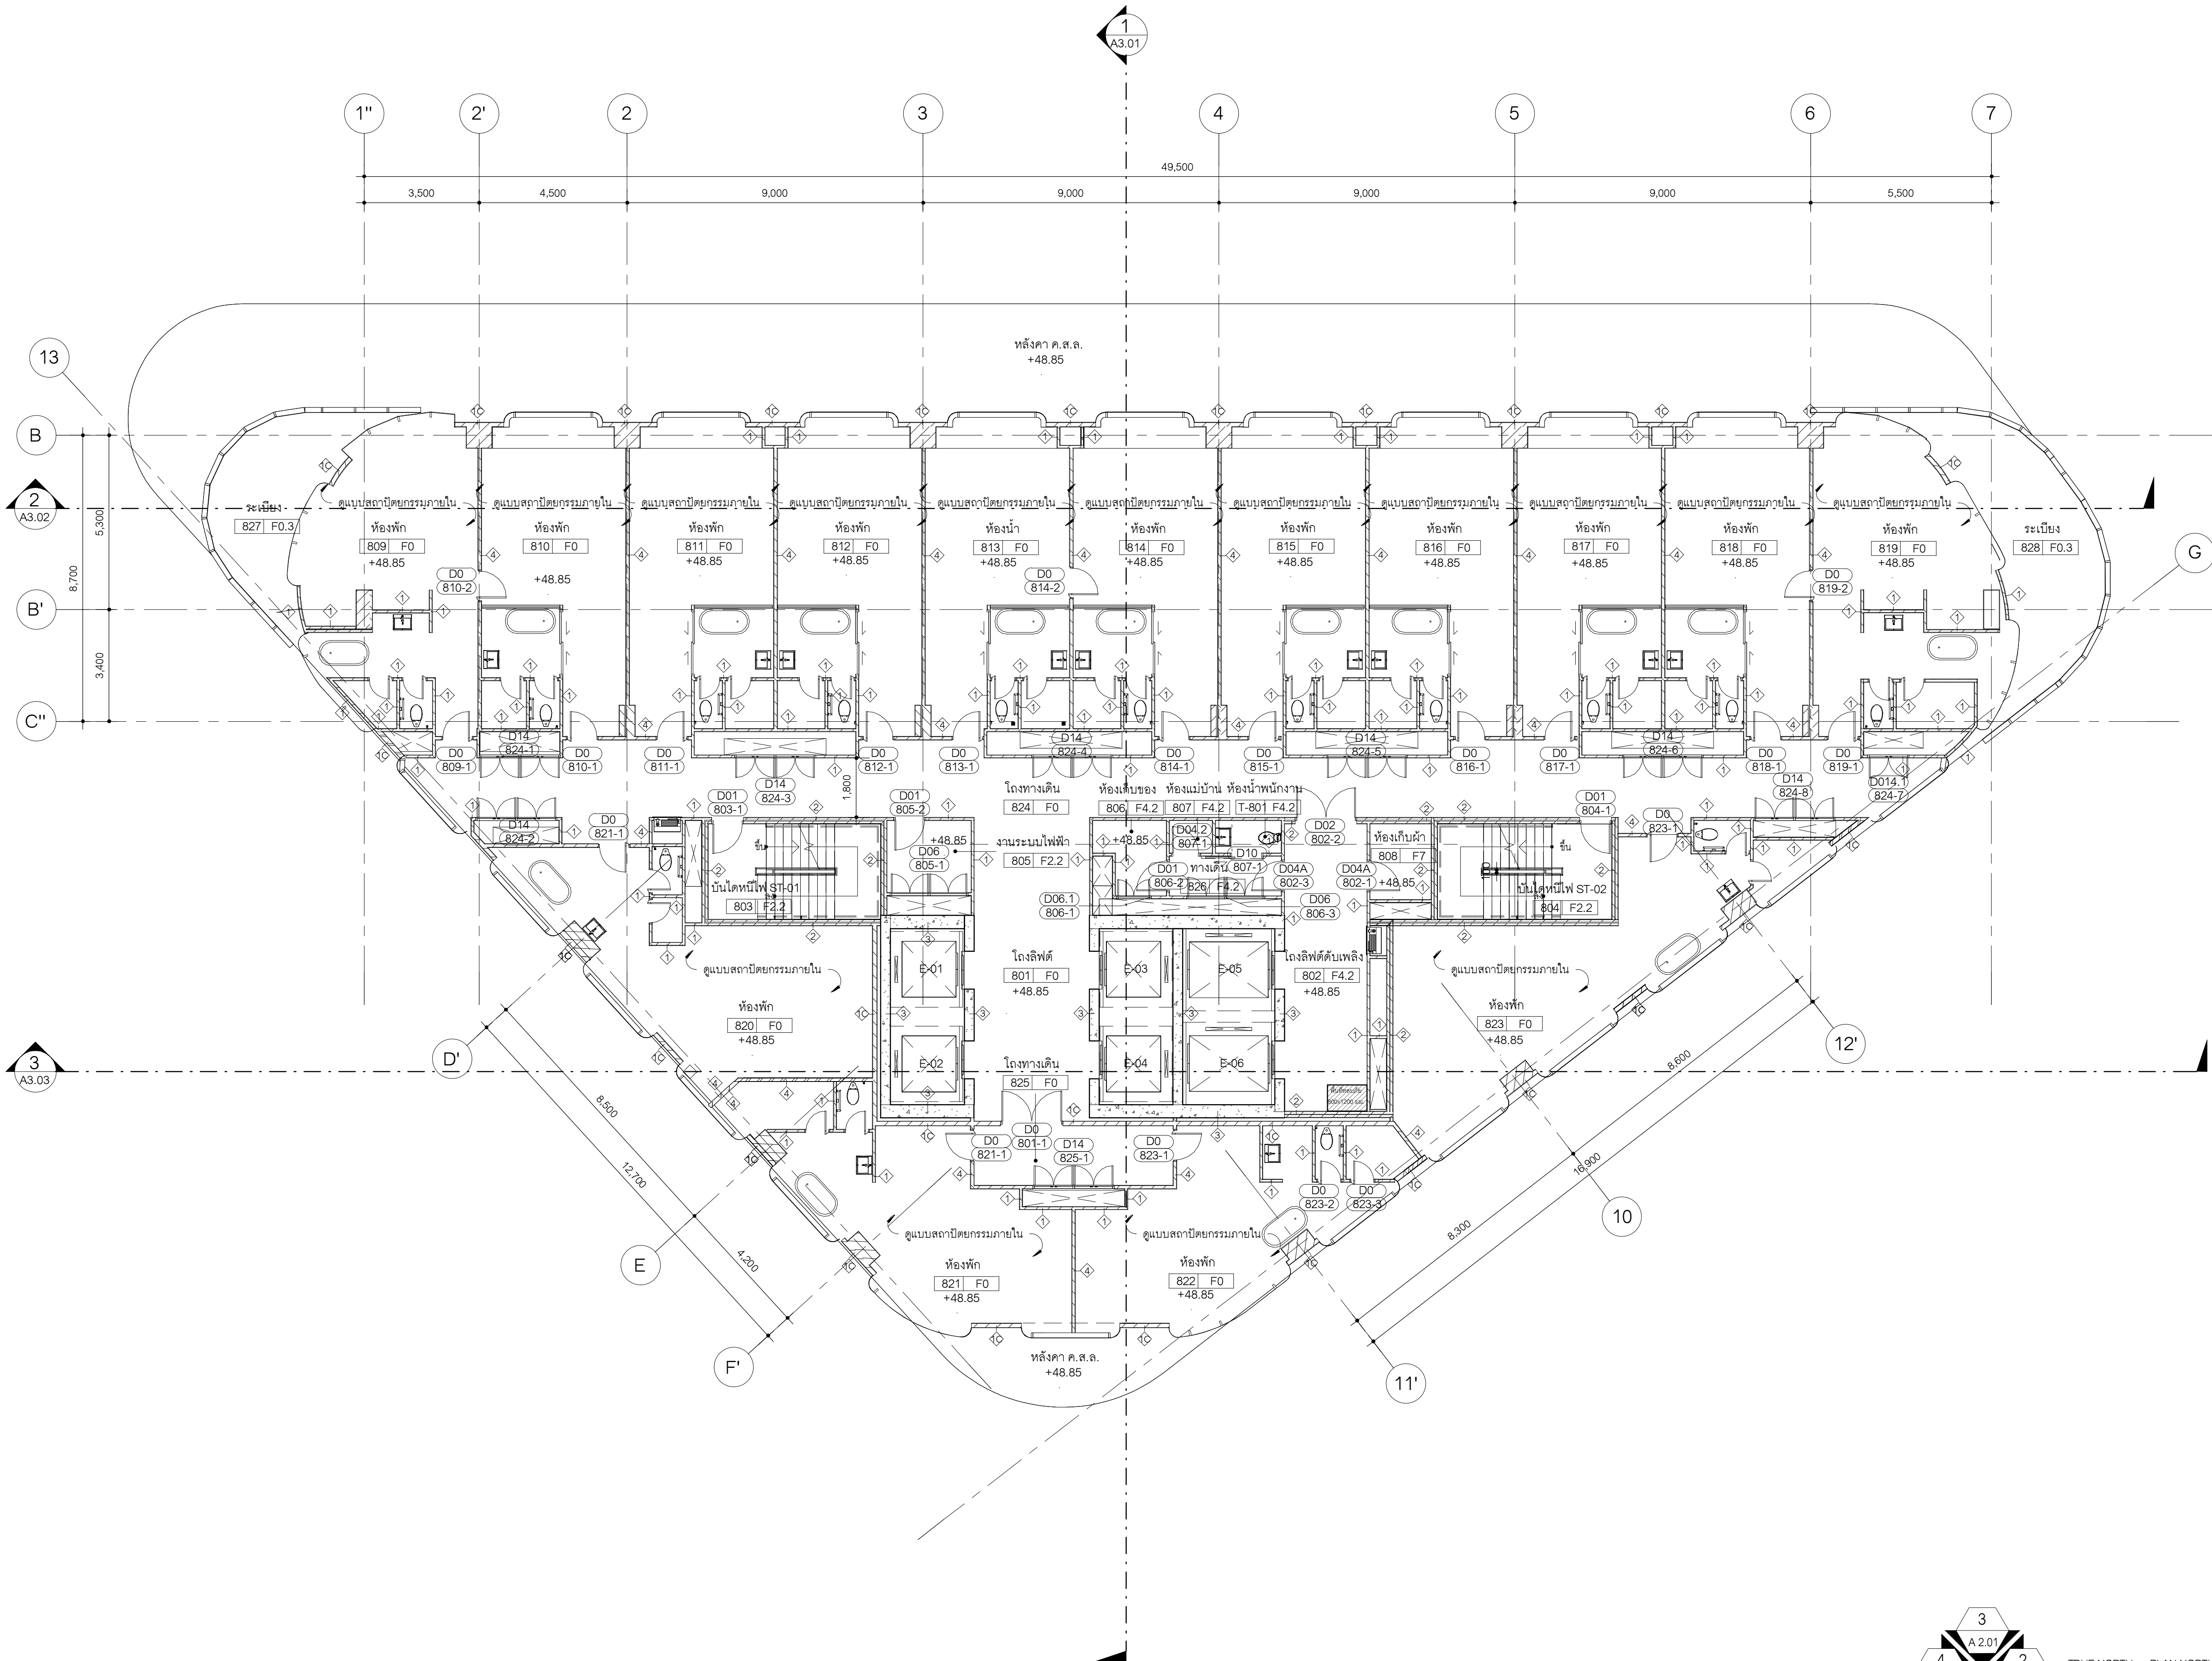


ผังพื้นที่ 8 (GUESTROOM)
มาตราส่วน 1:100

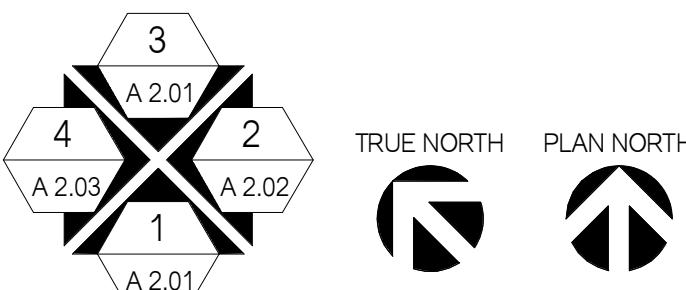

CHECK BY		DRAWING NO.
ARCHITECT	SIGNED	A1.19
PM		
PD		
PA		
JC		
DRAWN BY _____		SCALE: As Indicated
Author		
PRINTED DATE 17/04/2569		REF. FILE

LEVEL	+FFL
ระดับพื้นที่ 9	+52.25
ระดับพื้นที่ 10	+55.65
ระดับพื้นที่ 11	+59.05
ระดับพื้นที่ 12	+62.45
ระดับพื้นที่ 12A	+65.85

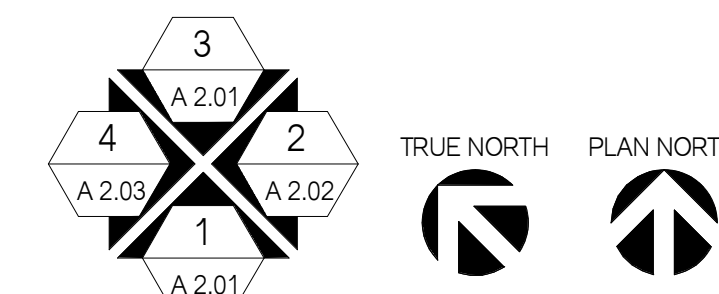

ผังพื้นที่ 9-13 (GUESTROOM)
มาตราส่วน 1:100

OWNER
LUXURY HOTEL DEVELOPMENT
SUKHUMVIT 38 CO., LTD.

DESIGNER
ARCHITECTS 49 LIMITED
81 SUKHUMVIT 26
BANGKOK 10110 THAILAND
T + 66 (0) 2260 4370
F + 66 (0) 2259 3872
E A49@A49.CO.TH
W A49.CO.TH

K.C.S. & ASSOCIATES CO. LTD.
22ND FLOOR, CHARN ISSARA TOWER II
2592/267 NEW PETCHABURI ROAD, BANGKAPI,
HUAY KWANG, BANGKOK 10310 THAILAND
T +66 (0) 2308 2481 5
F +66 (0) 2308 2485

MEC PRO DESIGN CO. LTD.
567 BUILDING 4TH FLOOR SUKUMVIT 38
SUAN LUANG, BANGKOK 10250 THAILAND
T +66 (0) 2170 8029
+66 (0) 97 034 8917
E MECPRO.DESIGN@GMAIL.COM

P.LANDSCAPE CO. LTD.
59/3 SUKHUMVIT 39, KLONGTON NUA,
WATTANA, BANGKOK 10110 THAILAND
T (622) 261 3700 TO 9
F (622) 238 9388
E INFO@PLANDSCAPE.COM
W WWW.PLANDSCAPE.COM

ARCHITECTS
พิธีกร วรวิทย์วรรณ วรณ.509
นางศศิธร อธิวิเศษ วรณ.720
นางวิมลพร อธิวิเศษ วรณ.769
นางวิมลพร อธิวิเศษ วรณ.3432
นางสุภากร ศรีสมบุญ วรณ.3347
นางปวีณา หิรัญน้อย วรณ.20910
นางศศิธร หิรัญน้อย วรณ.23830
นางวันพร หิรัญน้อย วรณ.27171

STRUCTURAL ENGINEER
นายบุญ จันทวงษ์ วรณ.1023
นายสุวิทย์ จันทวงษ์ วรณ.9572
นางสาวสุวิทย์ จันทวงษ์ วรณ.15169
นายสุวิทย์ จันทวงษ์ วรณ.69140

ELECTRICAL ENGINEER
นายธนกร นิ่มนวล วรณ.1118
นายสุวิทย์ นิ่มนวล วรณ.1386
นายสุวิทย์ นิ่มนวล วรณ.63548

MECHANICAL ENGINEER
นายธนกร นิ่มนวล วรณ.3566
นายสุวิทย์ นิ่มนวล วรณ.51088
นายสุวิทย์ นิ่มนวล วรณ.52030

ENVIRONMENTAL ENGINEER
นางสาววิมลพร อธิวิเศษ วรณ.625
นายสุวิทย์ นิ่มนวล วรณ.112
นายสุวิทย์ นิ่มนวล วรณ.7507

SANITARY ENGINEER
นายธนกร นิ่มนวล วรณ.1118
นายสุวิทย์ นิ่มนวล วรณ.1386
นายสุวิทย์ นิ่มนวล วรณ.63548

LANDSCAPE ARCHITECT
นายธนกร นิ่มนวล วรณ.1118
นายสุวิทย์ นิ่มนวล วรณ.1386
นายสุวิทย์ นิ่มนวล วรณ.63548

GENERAL NOTE
1. THIS DRAWING IS THE PROPERTY OF ARCHITECTS 49 LIMITED OR ONE OF ITS AFFILIATES. IT IS ISSUED SUBJECT TO RETURN UPON DEMAND AND IS NOT TO BE USED EXCEPT IN CONNECTION WITH THE PROJECT FOR WHICH IT IS INTENDED.
2. DO NOT SCALE THIS DRAWING. USE FIGURED DIMENSIONS ONLY.
3. DO NOT SCALE THIS DRAWING. USE FIGURED DIMENSIONS ONLY.

PROJECT NAME
THE OKURA PRESTIGE
SUKHUMVIT BANGKOK HOTEL
AND SPA


DRAWING TITLE
ผังพื้นที่ 14 (GUESTROOM)

ISSUE/REVISION
NO DESCRIPTION BY DATE
1 แก้ไขแบบแปลน A49 17/04/2569


CHECK BY
ARCHITECT SIGNED
PD
PA
JC
DRAWN BY Author
PRINTED DATE 17/04/2569
SCALE: 1:100
REF. FILE

DRAWING NO.

A1.20

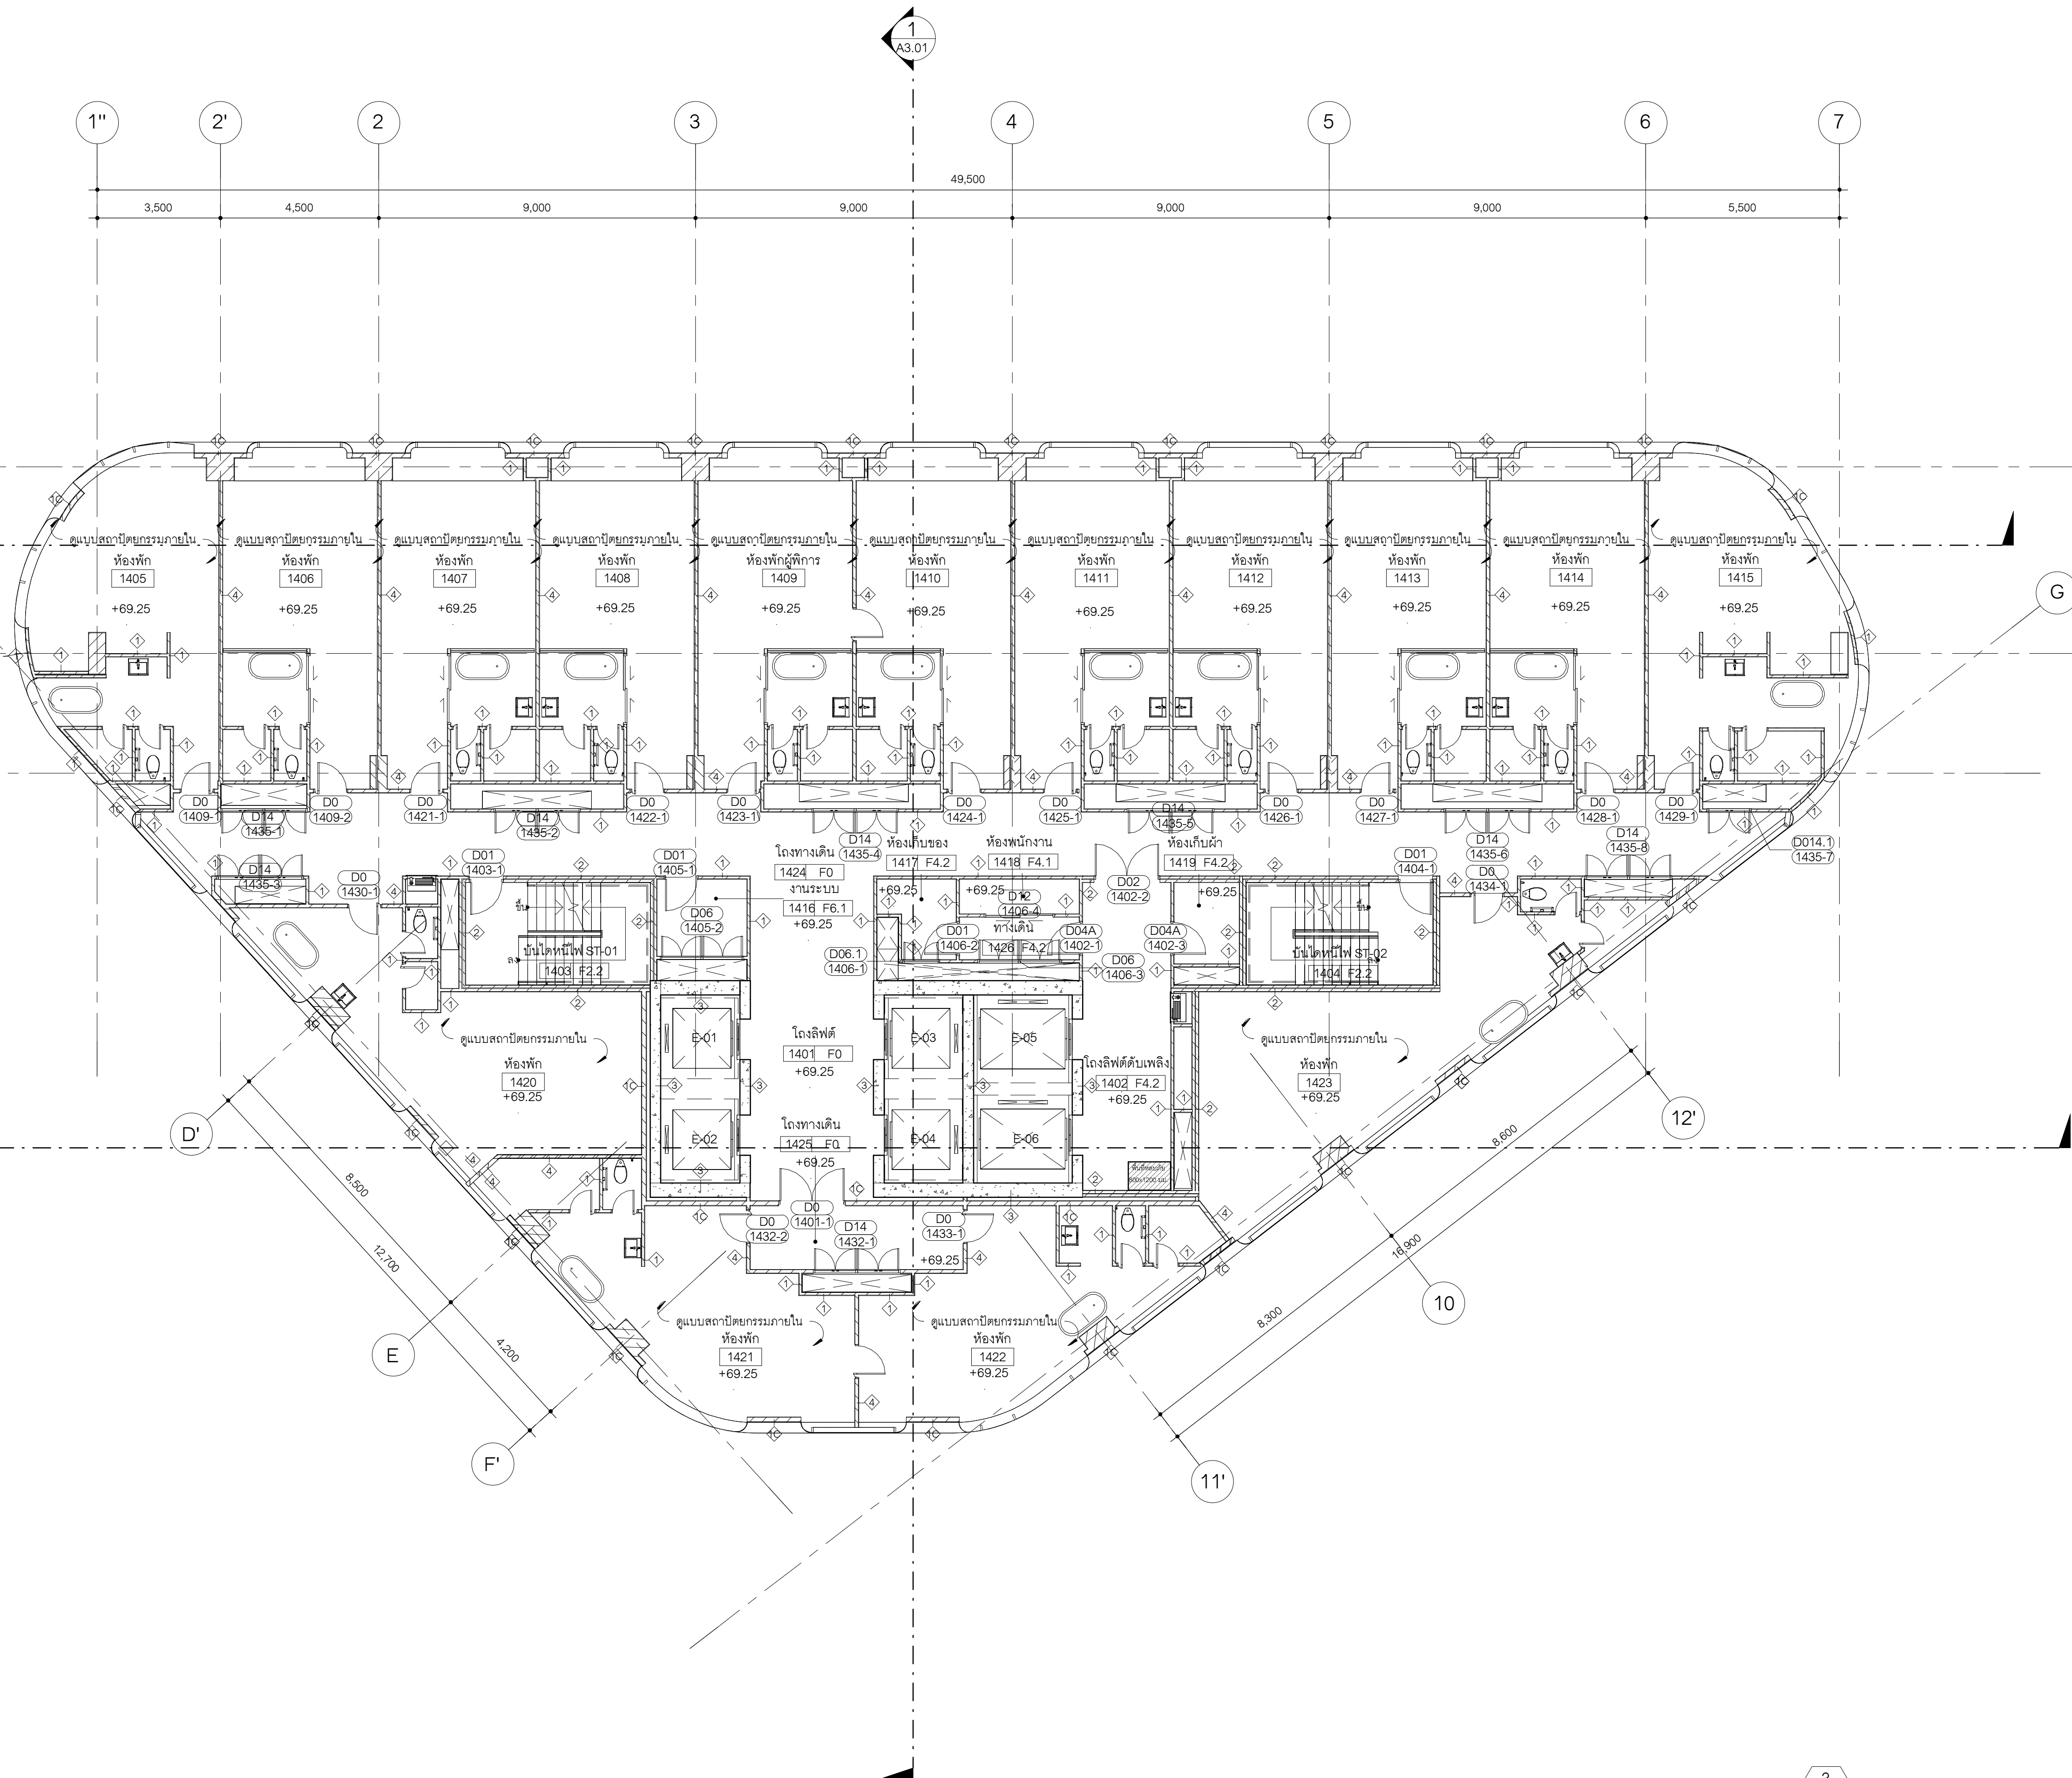

ผังพื้นที่ 14 (GUESTROOM)
มาตราส่วน 1:100

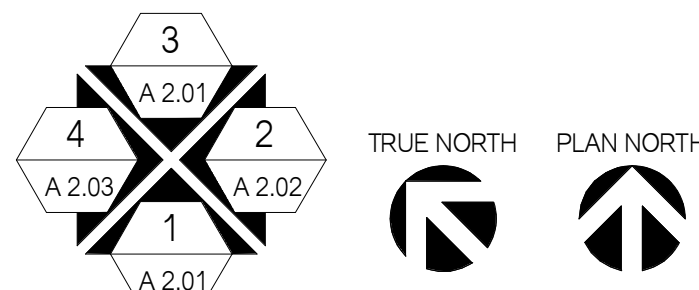

CHECK BY		DRAWING NO.	
ARCHITECT	SIGNED	A1.22	
PM			
PD			
PA			
JC			
DRAWN BY Author		SCALE: As Indicated	
PRINTED DATE 17/04/2569		REF. FILE	

11/18/2026 3:16:32 PM