

OWNER
LUXURY HOTEL DEVELOPMENT
SUKHUMVIT 38 CO., LTD.

DESIGNER
ARCHITECTS 49 LIMITED
81 SUKHUMVIT 26
BANGKOK 10110 THAILAND
T + 66 (0) 2260 4370
F + 66 (0) 2259 3872
E A49@A49.CO.TH
W A49.CO.TH

K.C.S. & ASSOCIATES CO. LTD.
22ND FLOOR, CHARN ISSARA TOWER II
2592/267 NEW PETCHABURI ROAD, BANGKAPI,
HUAY KWANG, BAKOK 10310 THAILAND
T +66 (0) 2308 2481 5
F +66 (0) 2308 2485

MEC PRO DESIGN CO. LTD.
567 BUILDING 4TH FLOOR, SUKUMVIT 38
SUAN LUANG, BANGKOK 10250 THAILAND
T +66 (0) 2170 8029
+66 (0) 97 034 8917
E MECPRO.DESIGN@GMAIL.COM

P LANDSCAPE CO. LTD.
59/3 SUKHUMVIT 39, KLONGTON NUA,
WATTANA, BANGKOK 10110 THAILAND
T (622) 261 3700 TO 9
F (622) 258 5888
E INFO@PLANDSCAPE.COM
W WWW.PLANDSCAPE.COM

ARCHITECTS
พิธีกร วรวิทย์วรรณ วสท.509
เนตรวิทย์ อธิวิตร วสท.720
จารุวิมล อธิวิตร วสท.769
ทิพย์พร อธิวิตร วสท.3432
สุภากร ศรีสมบุญ วสท.3347
ปรีดีศร์ หิมนันโย วสท.20910
ศรพร ศิริพาน วสท.23830
วันธรรณ พูลสวัสดิ์ วสท.27171

STRUCTURAL ENGINEER
การุญ จันทรางศุ วบ.1023
กุลศิริ จันทรางศุ สบ.9572
ภาณุ สายรวมญาติ สบ.15169
อภิสิทธิ์ สมอ้าง สบ.69140

ELECTRICAL ENGINEER
ชาน นิมิตกร วท.1118
ทนศักดิ์ พิศุฒิกุล สท.1386
ธนวัฒน์ น้อยจ้อย วกท.63548

MECHANICAL ENGINEER
เบนด ไซทอง สท.3566
ณภัทร วิเชียรพทยาคม วก.51088
วิฑรศักดิ์ บุญโคตร วก.52030

ENVIRONMENTAL ENGINEER
ทรงวุฒิ วิเศษศิลป์ สส.625
เบนด ไซทอง สท.112
วสุ สลายนบาล สท.7507

SANITARY ENGINEER
ชื่อ นามสกุล เลขใบอนุญาต

LANDSCAPE ARCHITECT
นัทธกร รามศรีโน้ตจั่น สท.108

GENERAL NOTE
1. THIS DRAWING IS THE PROPERTY OF ARCHITECTS 49 LIMITED OR ONE OF ITS AFFILIATES. IT IS ISSUED SUBJECT TO RETURN UPON DEMAND AND IS NOT TO BE USED EXCEPT IN CONNECTION WITH THE PROJECT FOR WHICH IT IS INTENDED.
2. DO NOT SCALE THIS DRAWING. USE FIGURED DIMENSIONS ONLY.
ให้ใช้ค่าตัวเลขที่กำหนดไว้เท่านั้น ห้ามวัดจากแบบ

PROJECT NAME
THE OKURA PRESTIGE
SUKHUMVIT BANGKOK HOTEL
AND SPA


DRAWING TITLE
ผังพื้นที่ 23 (GUESTROOM)

ISSUE/REVISION
NO DESCRIPTION BY DATE
1 แบบแปลนอาคาร A49 17/04/2569


CHECK BY
ARCHITECT SIGNED
PD
PA
JC
DRAWN BY Author SCALE: 1:100
PRINTED DATE 17/04/2569 REF. FILE

DRAWING NO.

A1.23

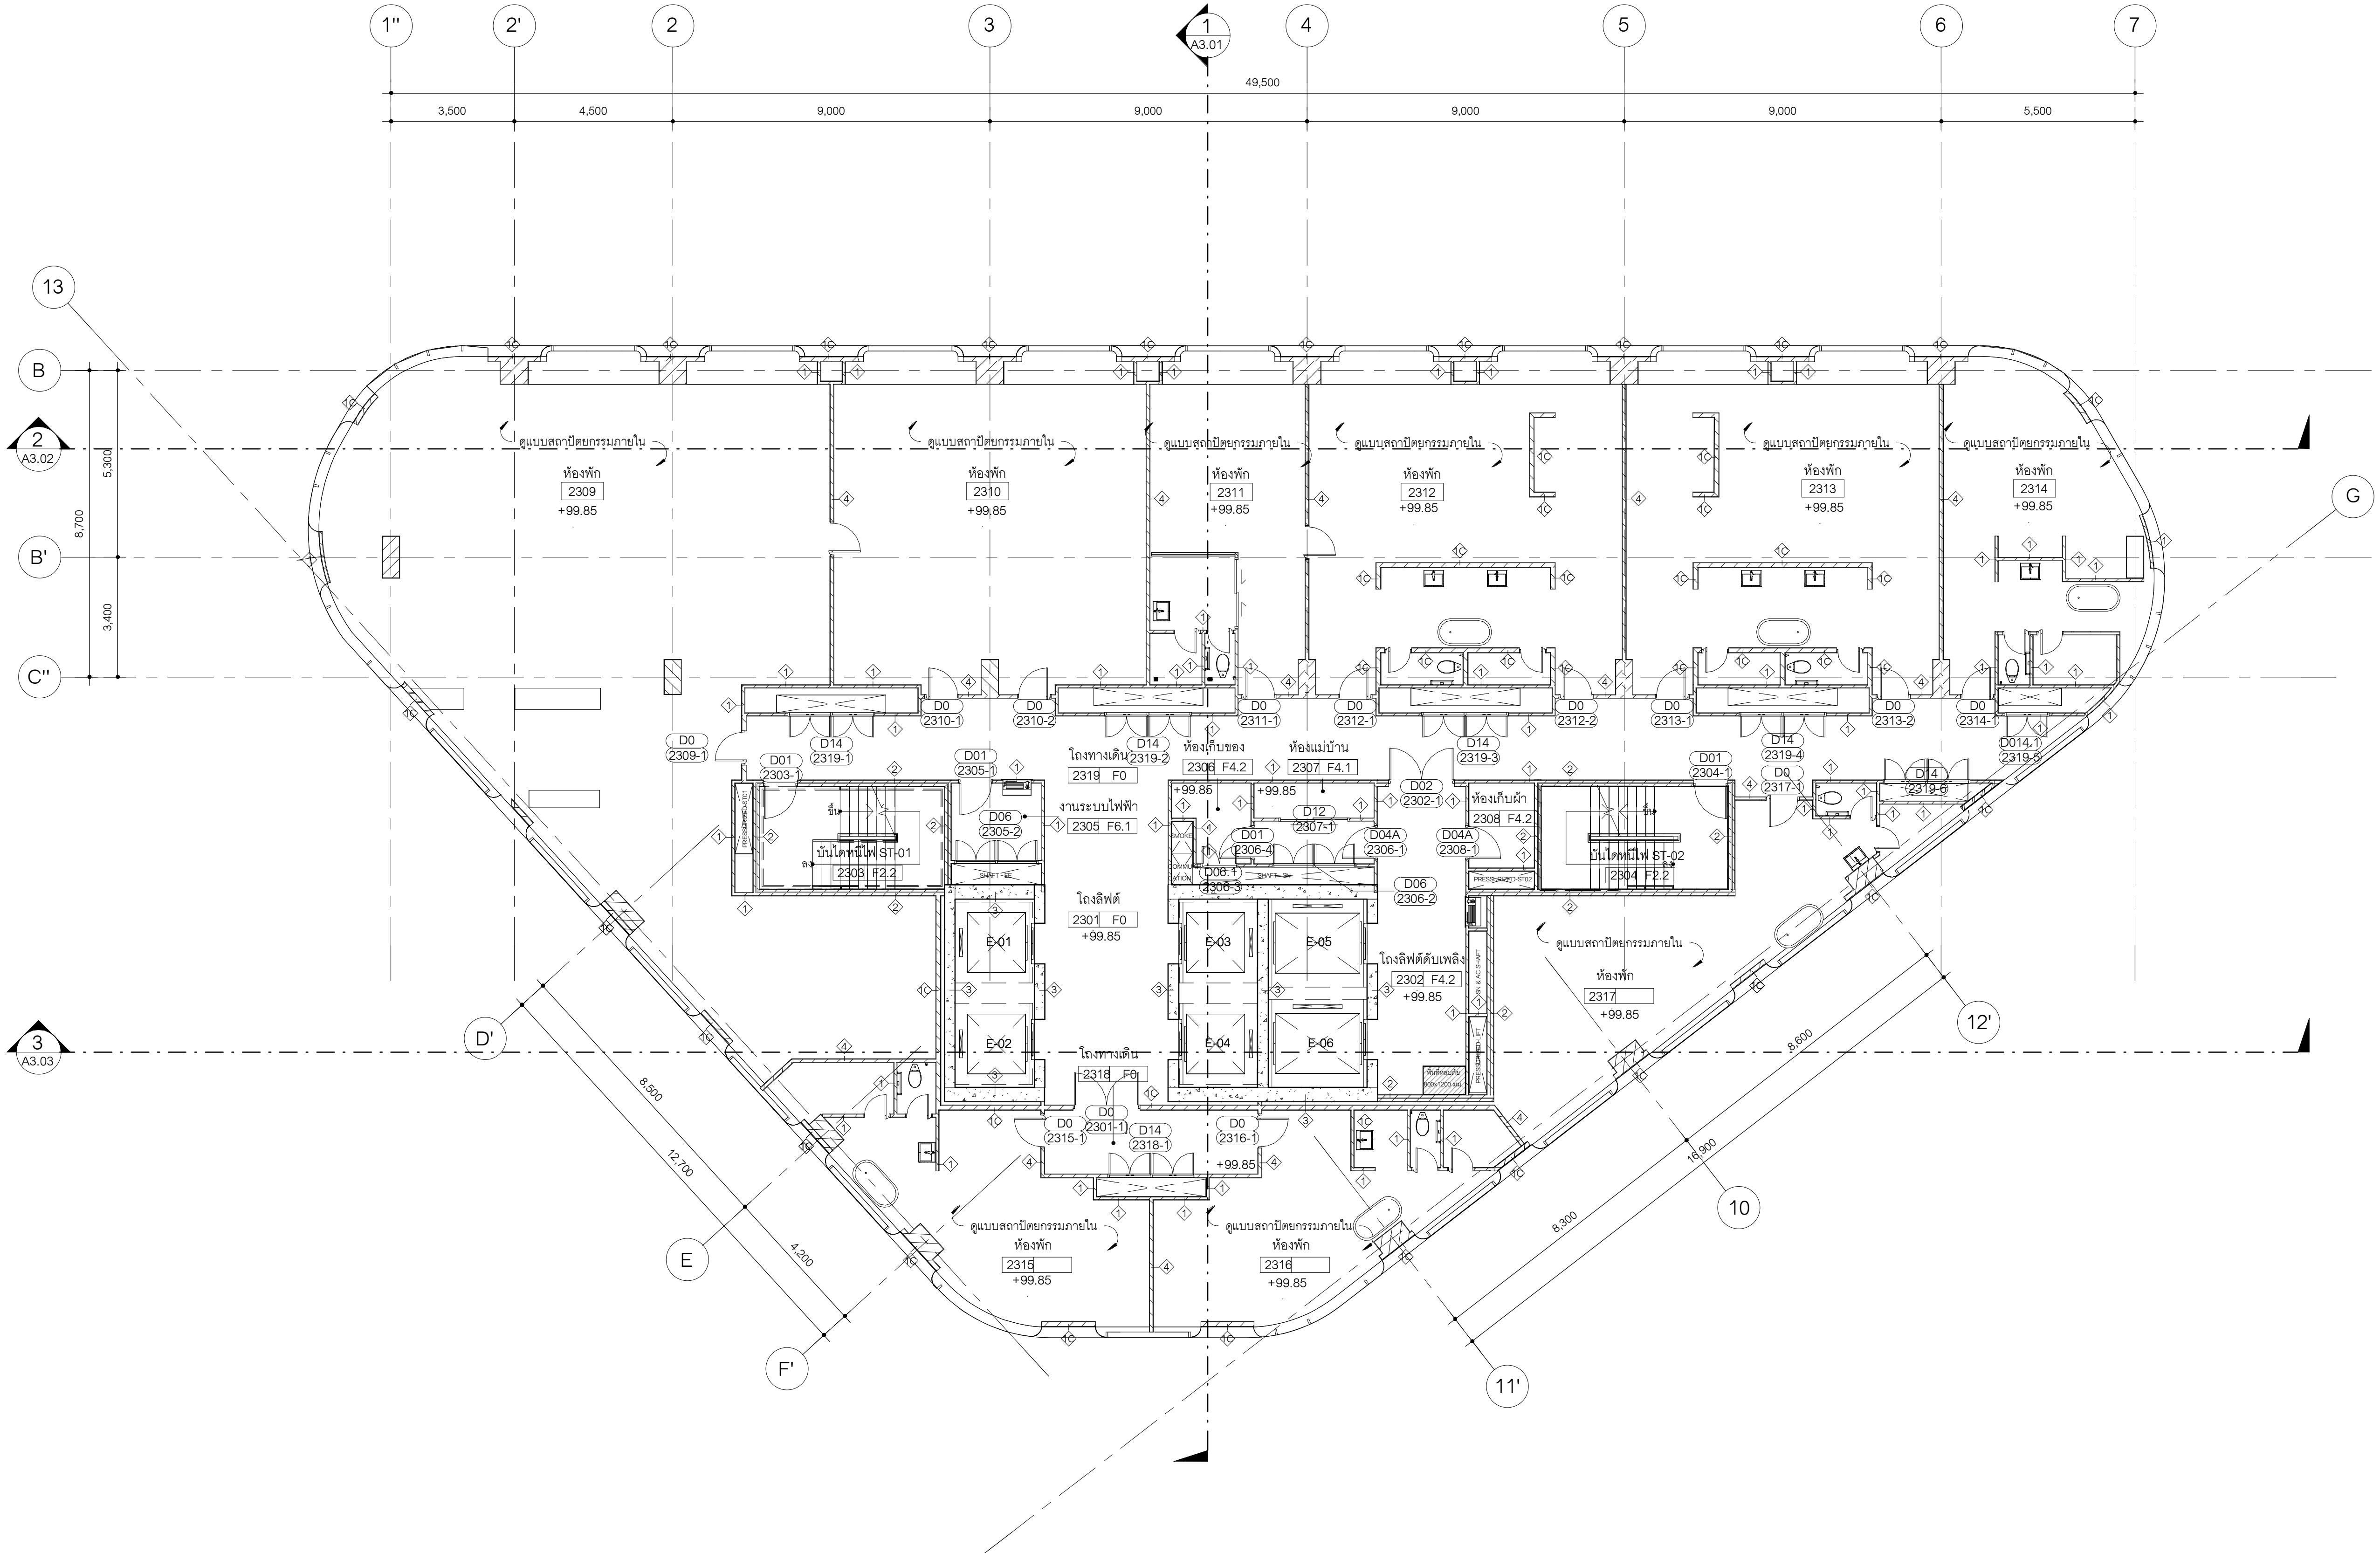

CHECK BY		DRAWING NO.
ARCHITECT	SIGNED	A1.24
PM		
PD		
PA		
JC		
DRAWN BY Author		SCALE: 1:100
PRINTED DATE 17/04/2559		REF. FILE

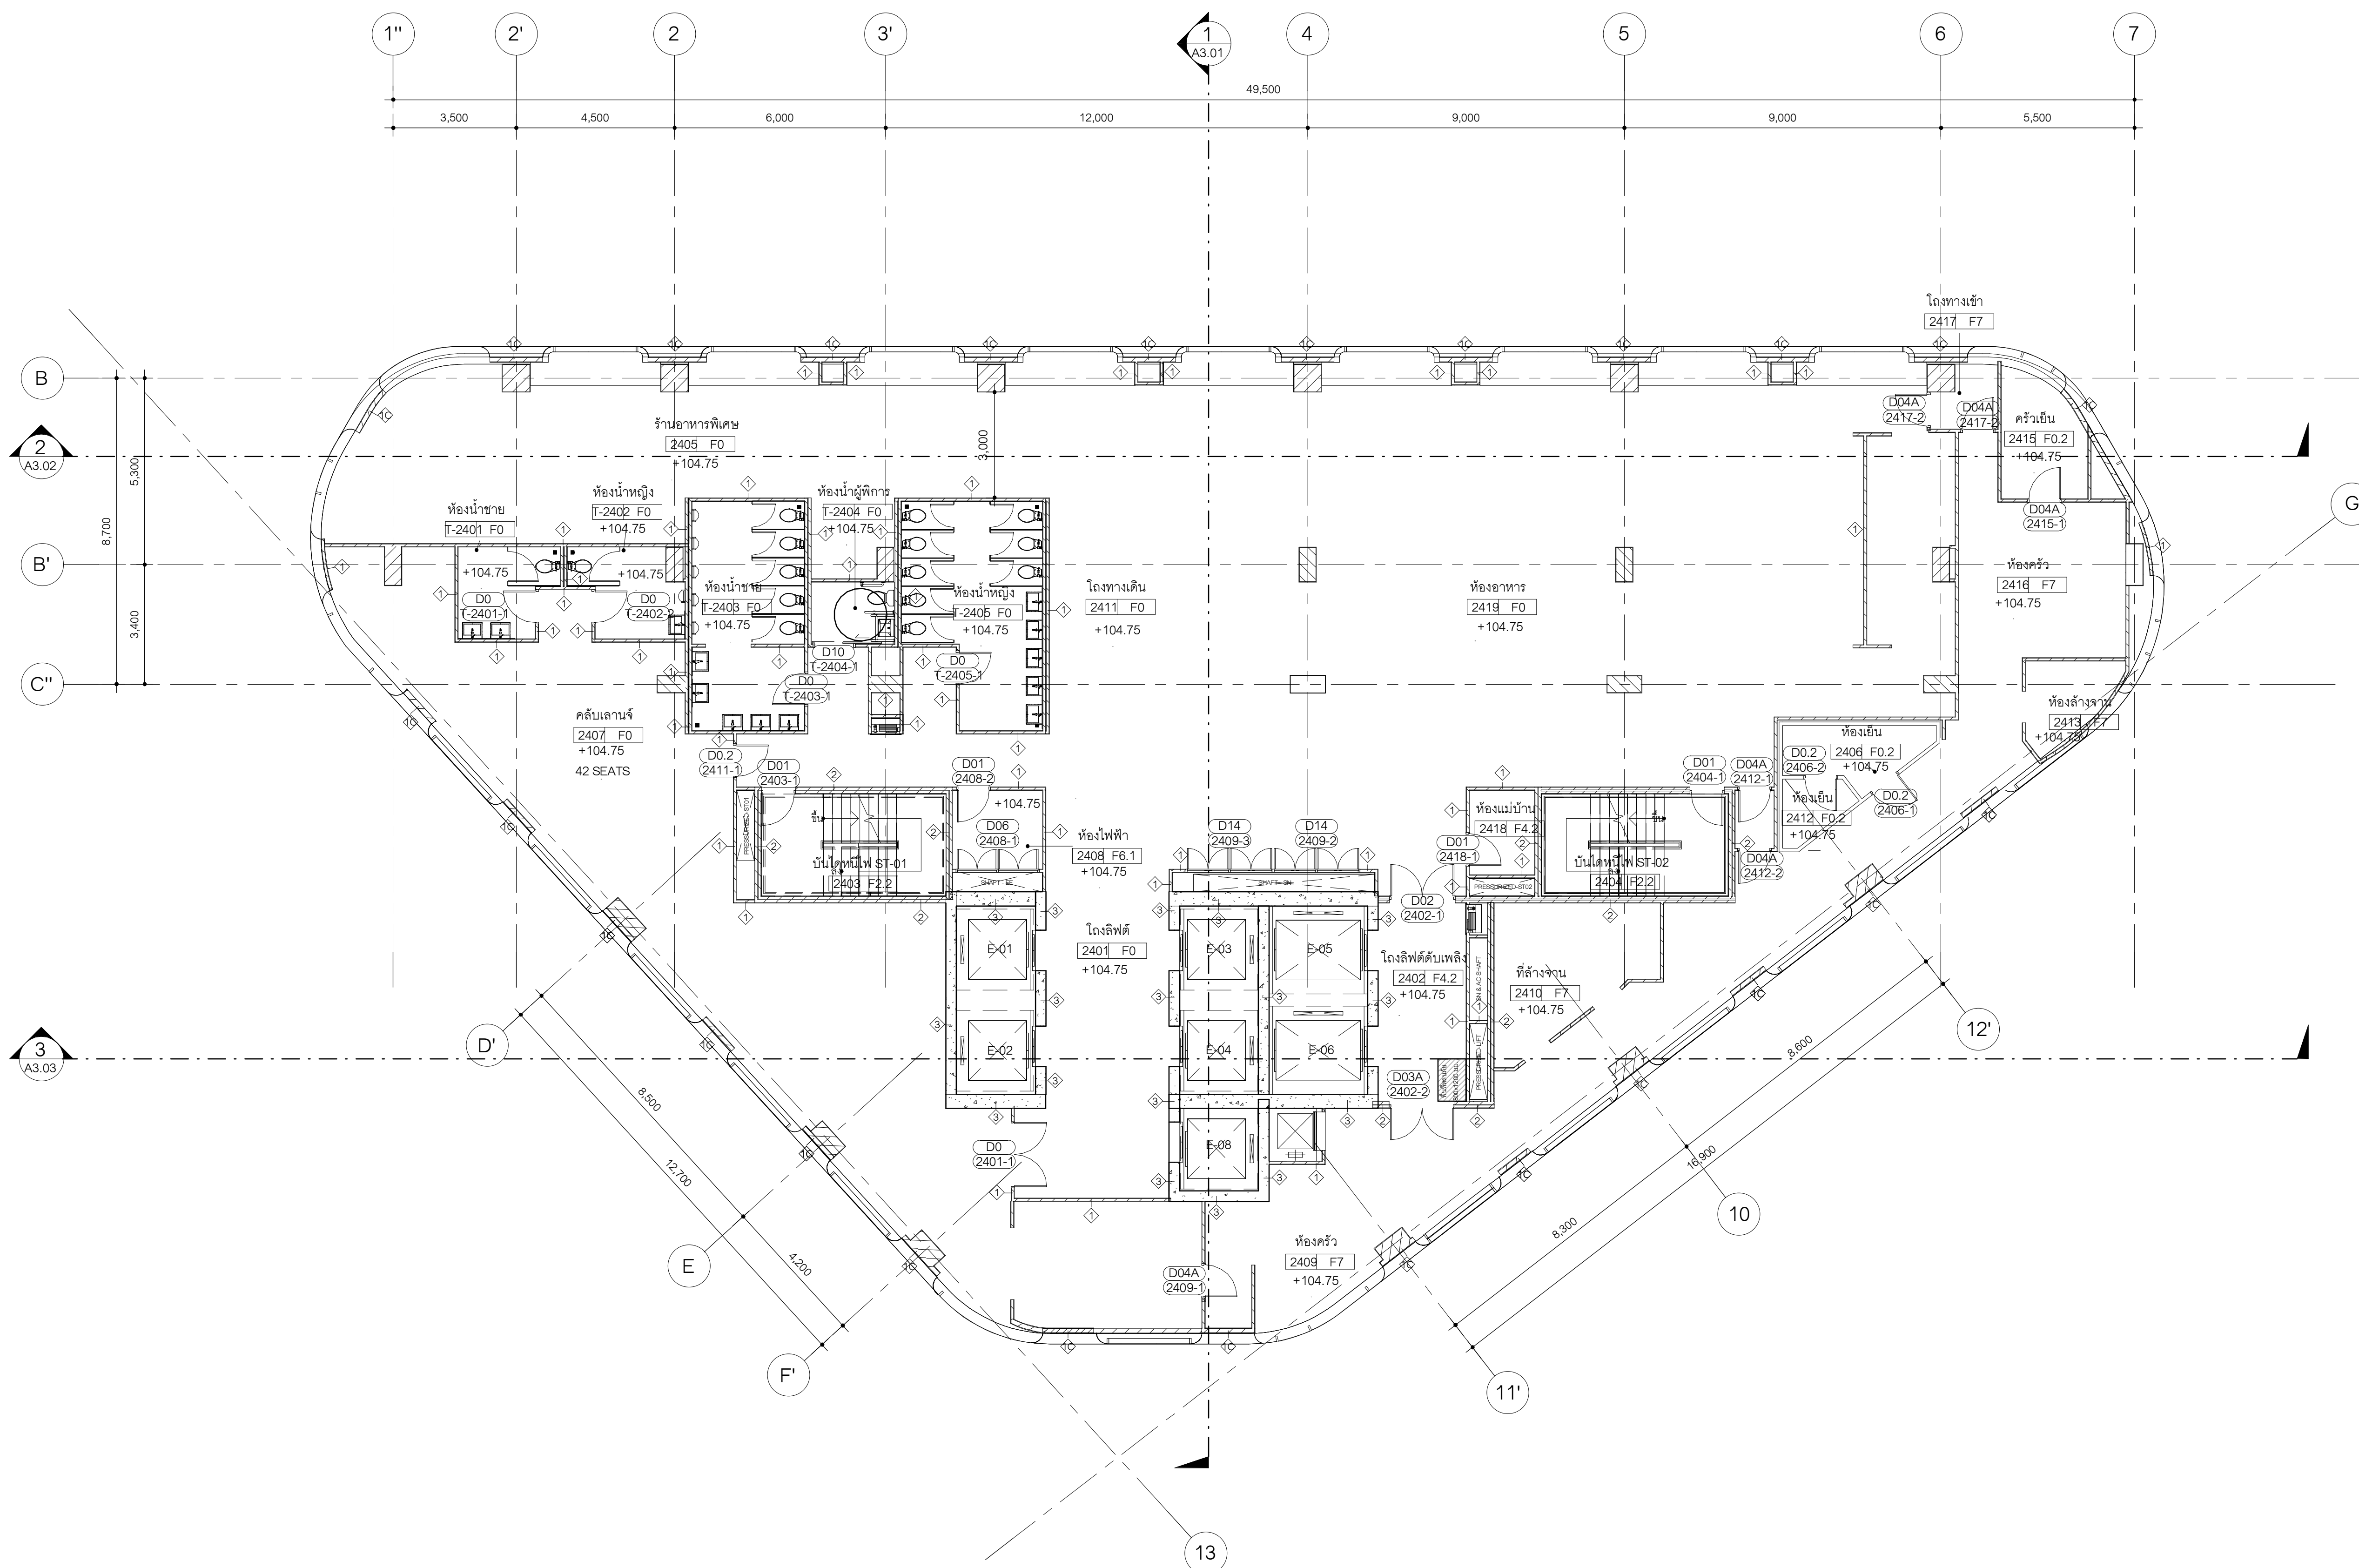

OWNER
LUXURY HOTEL DEVELOPMENT
SUKHUMVIT 38 CO., LTD.

DESIGNER
ARCHITECTS 49 LIMITED
81 SUKHUMVIT 26
BANGKOK 10110 THAILAND
T + 66 (0) 2260 4370
F + 66 (0) 2259 3872
E A49@A49.CO.TH
W A49.CO.TH

K.C.S. & ASSOCIATES CO. LTD.
22ND FLOOR, CHARN ISSARA TOWER II
2592/267 NEW PETCHABURI ROAD, BANGKAPI,
HUAY KWANG, BAKOK 10310 THAILAND
T +66 (0) 2308 2481 5
F +66 (0) 2308 2485

MEC PRO DESIGN CO. LTD.
567 BUILDING 4TH FLOOR SUAN LUANG
SUAN LUANG, BANGKOK 10250 THAILAND
T +66 (0) 2170 8029
+66 (0) 97 034 8917
E MECPRO.DESIGN@GMAIL.COM

P LANDSCAPE CO. LTD.
59/3 SUKHUMVIT 39, KLONGTON NUA,
WATTANA, BANGKOK 10110 THAILAND
T (622) 261 3700 TO 9
F (622) 238 3388
E INFO@PLANDSCAPE.COM
W WWW.PLANDSCAPE.COM

ARCHITECTS			SIGNED
พิธีชัย วงศ์โกลนวรรณ	วส. 509		
เนตรศศิวิทย์ อธิวิเศษ	วส. 720		
จารุวิมลพร อธิวิเศษ	วส. 769		
พิชญพร อธิวิเศษ	วส. 3432		
สุภากร ศรีสมบุญ	วส. 3347		
ปาริชาติ หิมนันโวย	วส. 20910		
ศสพร ศิริพานิช	วส. 23830		
วันวิมลพร พูลสวัสดิ์	วส. 27171		

STRUCTURAL ENGINEER			SIGNED
ภาณุชัย จันทวงศ	ว. 1023		
ภูริสร์ จันทวงศ	ว. 9572		
ภาณุ สายรวมญาติ	ว. 15169		
อภิสิทธิ์ สมอียง	ว. 69140		

ELECTRICAL ENGINEER			SIGNED
ชานน นิ่มตรง	ว. 1118		
พนิตศักดิ์ พันธ์สูง	ว. 1586		
ธนวัฒน์ น้อยจ้อย	ว. 63548		

MECHANICAL ENGINEER			SIGNED
ธนศ ไชยพงษ์	ว. 3566		
ณภัทร วิเชียรพทยาคม	ว. 51086		
วิภากร บุญนิยม	ว. 52030		

ENVIRONMENTAL ENGINEER			SIGNED
ทรงวุฒิ วิเศษศิลป์	ว. 625		
เนตร ไชยพงษ์	ว. 112		
วสุ ละเอียดศิลป์	ว. 7507		

SANITARY ENGINEER			SIGNED
ธีร นามสกุล	ว. 1586		

LANDSCAPE ARCHITECT			SIGNED
นันทิกร รณศิริโน้ต	ว. 108		

GENERAL NOTE
1. THIS DRAWING IS THE PROPERTY OF ARCHITECTS 49 LIMITED OR ONE OF ITS AFFILIATES. IT IS ISSUED SUBJECT TO RETURN UPON DEMAND AND IS NOT TO BE USED EXCEPT IN CONNECTION WITH THE PROJECT FOR WHICH IT IS INTENDED.
2. DO NOT SCALE THIS DRAWING. USE FIGURED DIMENSIONS ONLY.
ไม่ใช้ตัวเลขนี้นี้ในการวัดขนาด

PROJECT NAME
THE OKURA PRESTIGE
SUKHUMVIT BANGKOK HOTEL
AND SPA


DRAWING TITLE
ผังพื้นที่ 27 (SWIMMING POOL)

ISSUE/REVISION			
NO	DESCRIPTION	BY	DATE
1	แบบแปลนอาคาร	A49	17/04/2569


CHECK BY
ARCHITECT SIGNED

DRAWING NO.
A1.27


DRAWN BY Author
PRINTED DATE 17/04/2569
SCALE: 1:100
REF. FILE

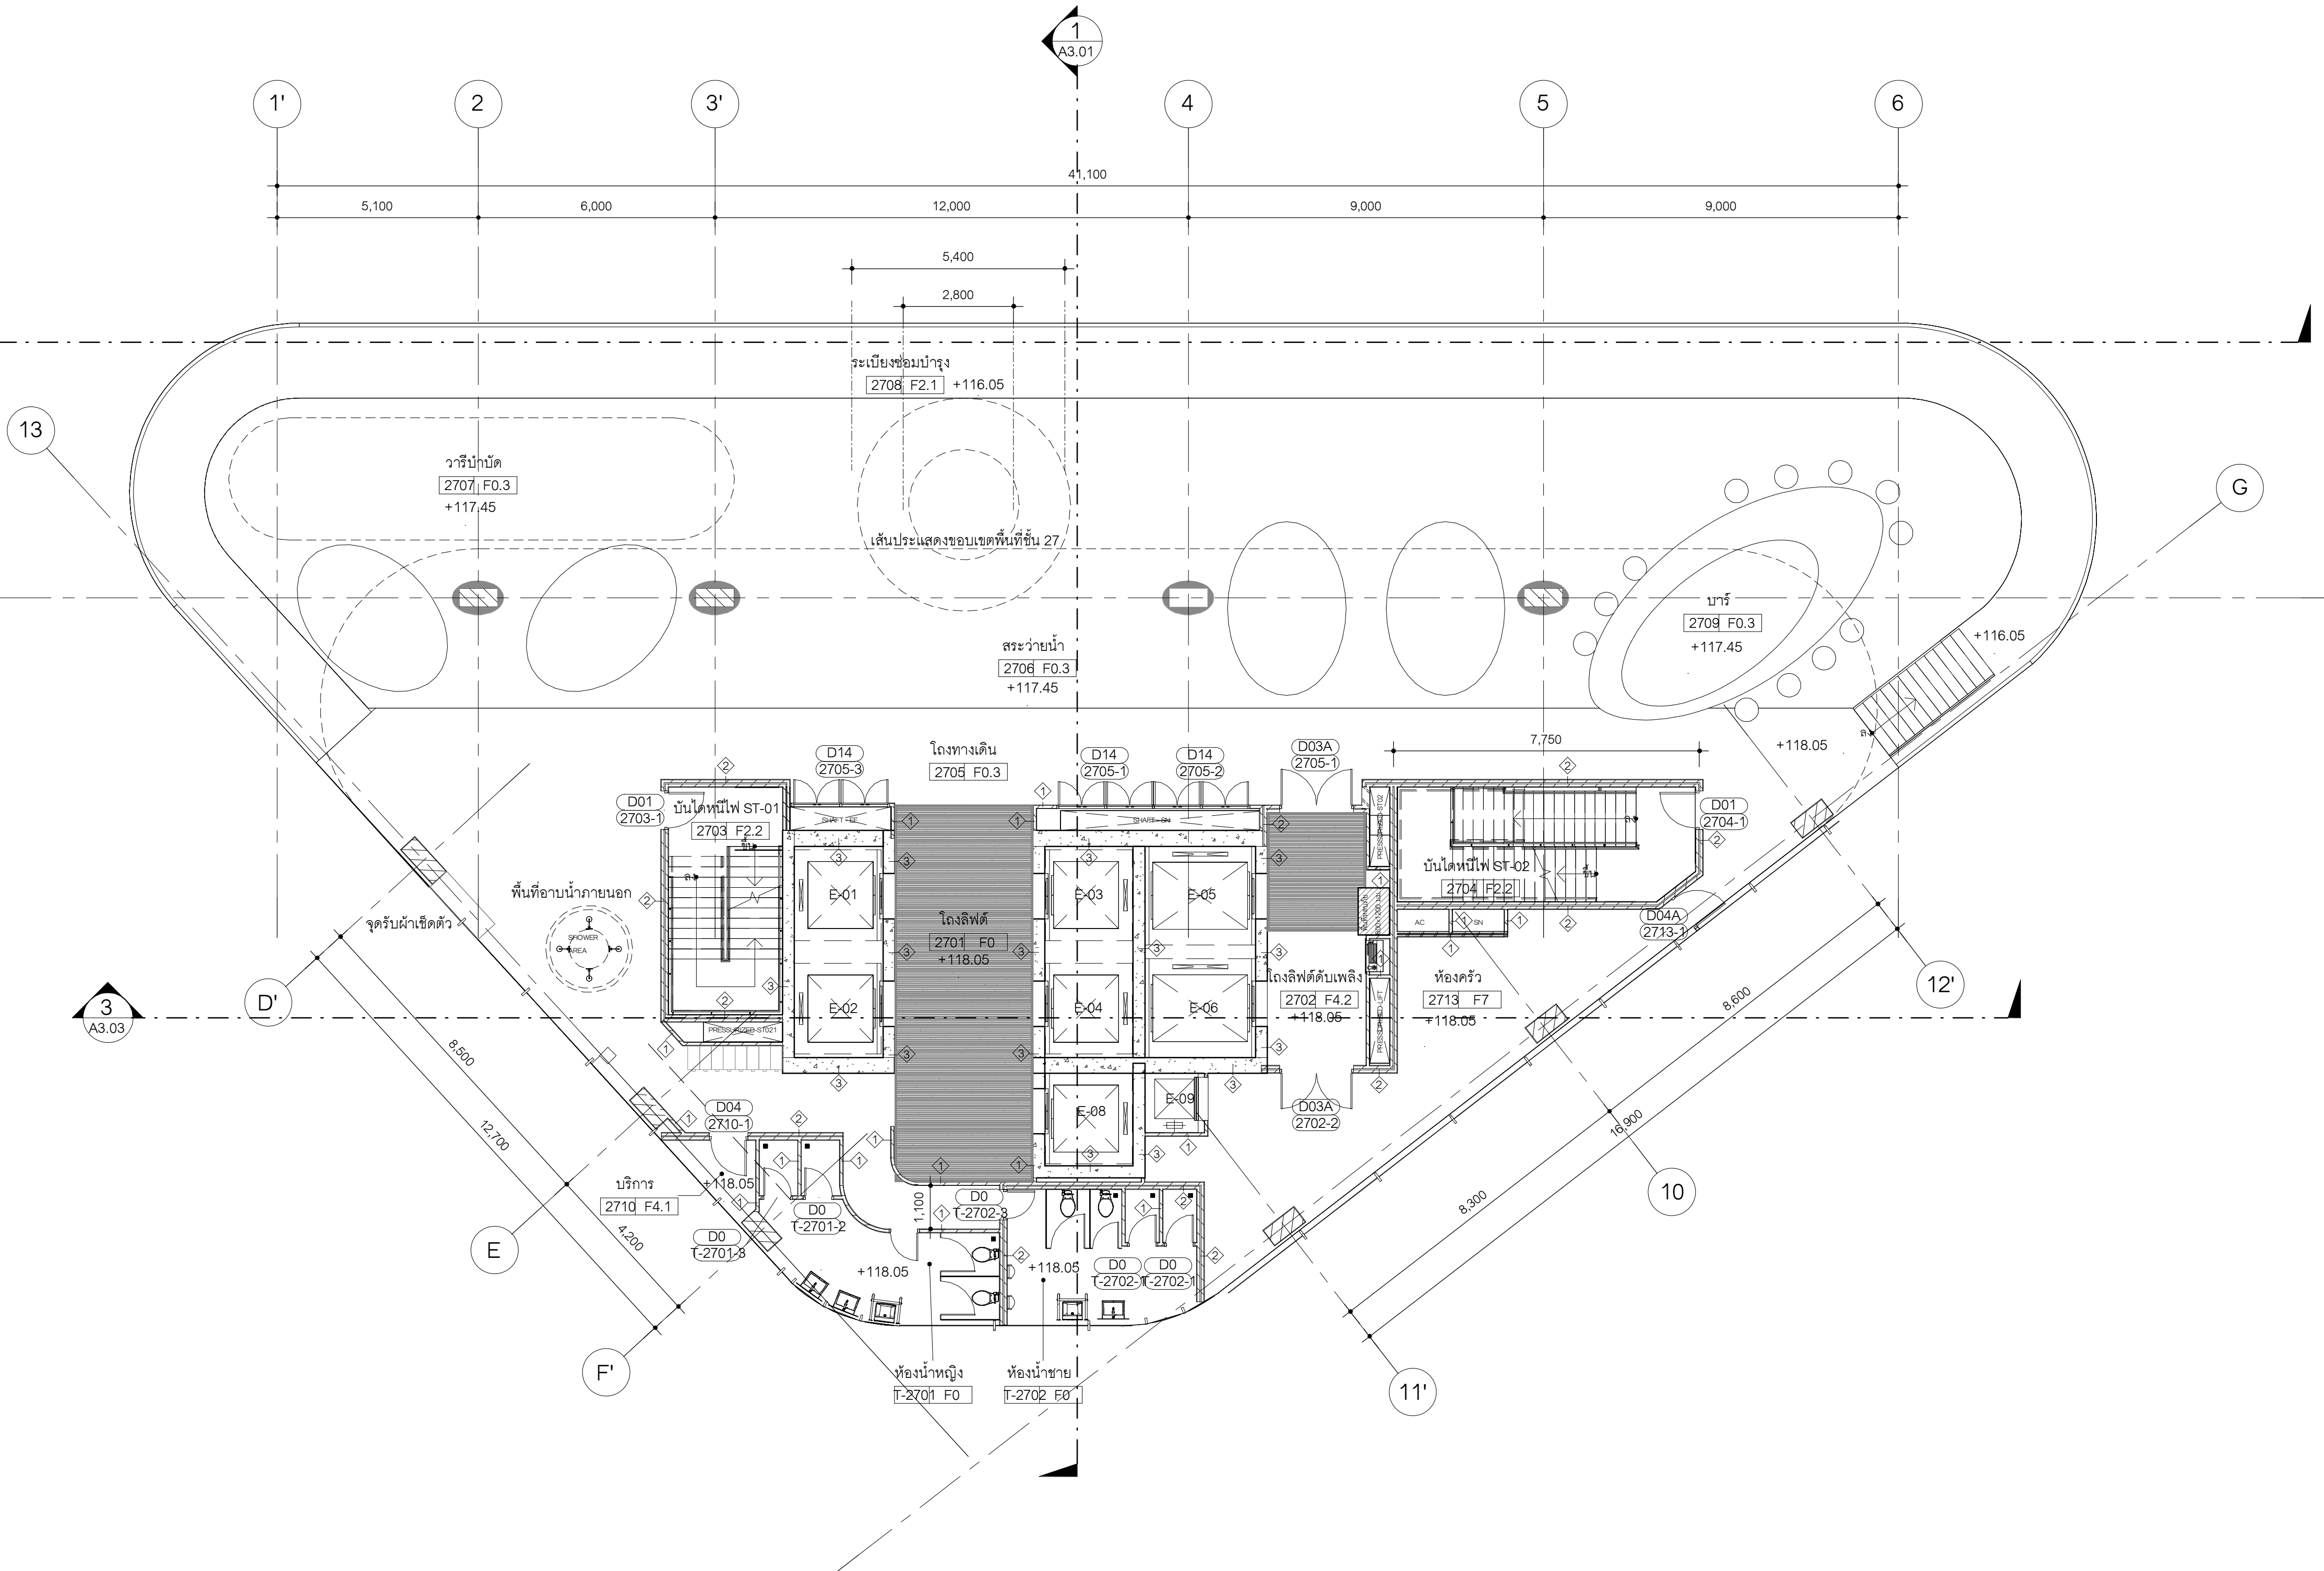


ผังพื้นที่ 27 (SWIMMING POOL)
มาตราส่วน 1 : 100

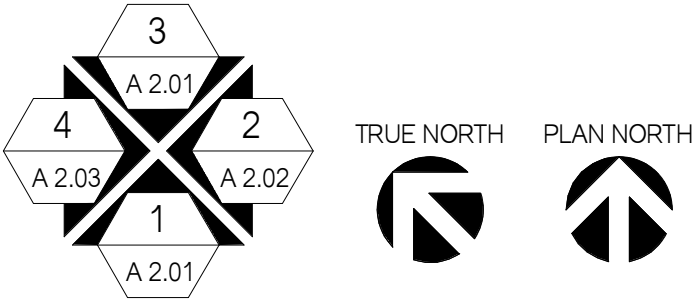

4/18/2026 3:17:00 PM

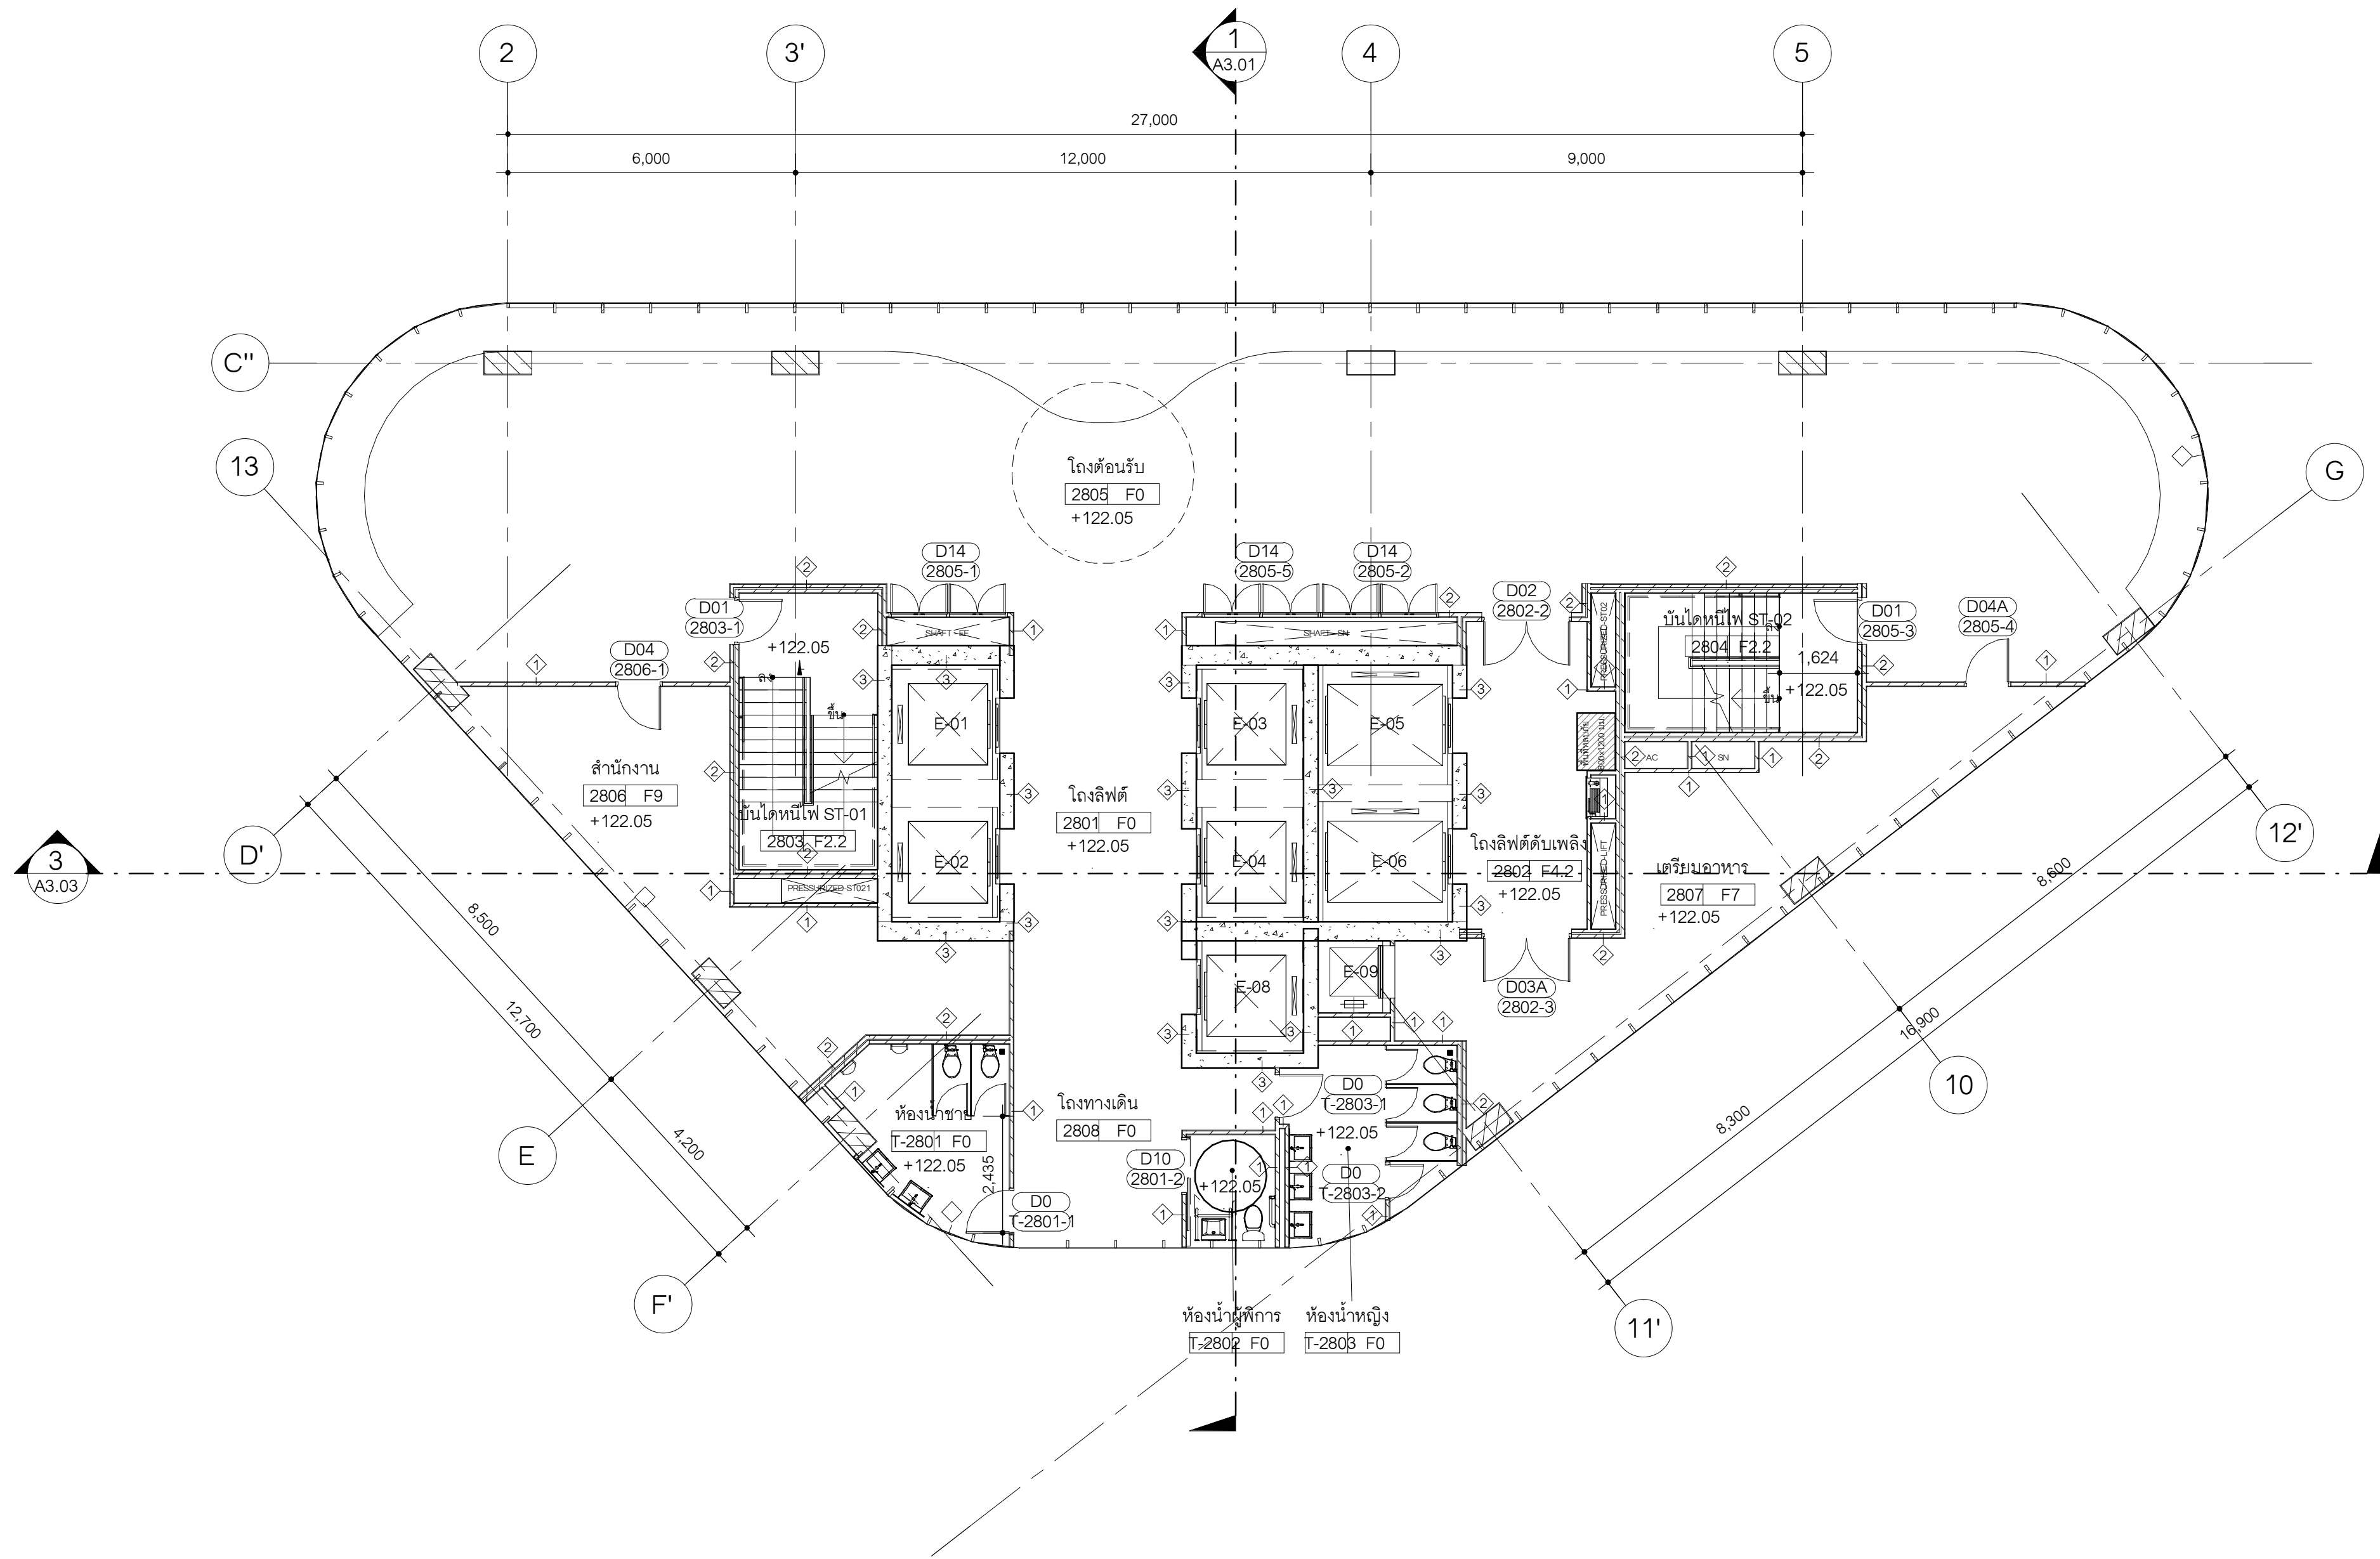

ผังพื้นที่ 28 (LOBBY)
มาตราส่วน 1 : 100

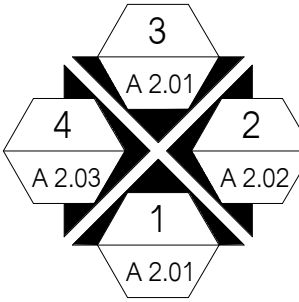

TRUE NORTH
PLAN NORTH

OWNER
LUXURY HOTEL DEVELOPMENT
SUKHUMVIT 38 CO., LTD.

DESIGNER
ARCHITECTS 49 LIMITED
81 SUKHUMVIT 26
BANGKOK 10110 THAILAND
T + 66 (0) 2260 4370
F + 66 (0) 2259 3872
E A49@A49.CO.TH
W A49.CO.TH

A | 49

K.C.S. & ASSOCIATES CO. LTD.
22ND FLOOR, CHARN ISSARA TOWER II
2592/267 NEW PETCHABURI ROAD, BANGKAPI,
HUAY KWANG, BAKOK 10310 THAILAND
T +66 (0) 2308 2481 5
F +66 (0) 2308 2485

KCS
K.C.S. & ASSOCIATES CO. LTD.

MEC PRO DESIGN CO. LTD.
567 BUILDING 4TH RAMA IX SOI 51
SUAN LUANG, BANGKOK 10250 THAILAND
T +66 (0) 2170 8029
+66 (0) 97 034 8917
E MECPRO.DESIGN@GMAIL.COM

MEC PRO
DESIGN

P LANDSCAPE CO. LTD.
59/3 SUKHUMVIT 39, KLONGTON NUA,
WATTANA, BANGKOK 10110 THAILAND
T (622) 261 3700 TO 9
F (622) 239 3388
E INFO@PLANDSCAPE.COM
W WWW.PLANDSCAPE.COM

pla | | |

ARCHITECTS				SIGNED
พิธีชัย	วงศ์โศภณวรรณ	วสท.509		
เนรศักดิ์ชัย	อ.วิจิตร	วสท.720		
จารุวัฒน์	อ.วิเศษชัยศักดิ์	วสท.769		
พิณมพร	อ.พนธ์ศักดิ์	สท.3432		
สุชาภา	ศรีสมบุญ	สท.3347		
ปาริชาติ	จินนีน้อย	วสท.20910		
คสพร	ศิริพจน์	วสท.23830		
วันชนน	พลสวัสดิ์	วสท.27171		

STRUCTURAL ENGINEER				SIGNED
ภาณุ	จันทราวุธ	วสท.1023		
กุลศิริ	จันทราวุธ	สท.9572		
ภาณุ	สายวรมงคล	สท.15169		
อภิสัย	สมชาย	วสท.69140		

ELECTRICAL ENGINEER				SIGNED
ชาน	นิมิต	วสท.1118		
พนธ์ศักดิ์	พิชิต	สท.1586		
ธนวิวัฒน์	น้อยจ้อย	วสท.63548		

MECHANICAL ENGINEER				SIGNED
เบน	ไชยพงษ์	สท.3566		
ณภัทร	วิเชียรเทพาคุณ	วสท.51088		
วิฑร	บุญนิยม	วสท.52030		

ENVIRONMENTAL ENGINEER				SIGNED
ทรงวุฒิ	วิเศษชัย	สท.625		
เบน	ไชยพงษ์	วสท.112		
วิฑร	ละลาขณ	วสท.7507		

SANITARY ENGINEER				SIGNED
ช่อ	นามสกุล	เลขใบอนุญาต		

LANDSCAPE ARCHITECT				SIGNED
นัท	รณชัยโพธิ์	สท.108		

GENERAL NOTE
1. THIS DRAWING IS THE PROPERTY OF ARCHITECTS 49 LIMITED OR ONE OF ITS AFFILIATES. IT IS ISSUED SUBJECT TO RETURN UPON DEMAND AND IS NOT TO BE USED EXCEPT IN CONNECTION WITH THE PROJECT FOR WHICH IT IS INTENDED.
2. DO NOT SCALE THIS DRAWING. USE FIGURED DIMENSIONS ONLY.
ให้ใช้ค่าตัวเลขที่กำหนดไว้เท่านั้น ห้ามวัดจากแบบ


PROJECT NAME
THE OKURA PRESTIGE
SUKHUMVIT BANGKOK HOTEL
AND SPA

DRAWING TITLE
ผังพื้นที่ 28 (LOBBY)


ISSUE/REVISION			
NO	DESCRIPTION	BY	DATE
1	แบบแปลนสถาปัตย์	A49	17/04/2569

CHECK BY		DRAWING NO.	
ARCHITECT	SIGNED	A1.28	
PM			
PD			
PA			
JC			
DRAWN BY	Author	SCALE:	1 : 100
PRINTED DATE	17/04/2569	REF. FILE	

4/18/2026 3:17:04 PM

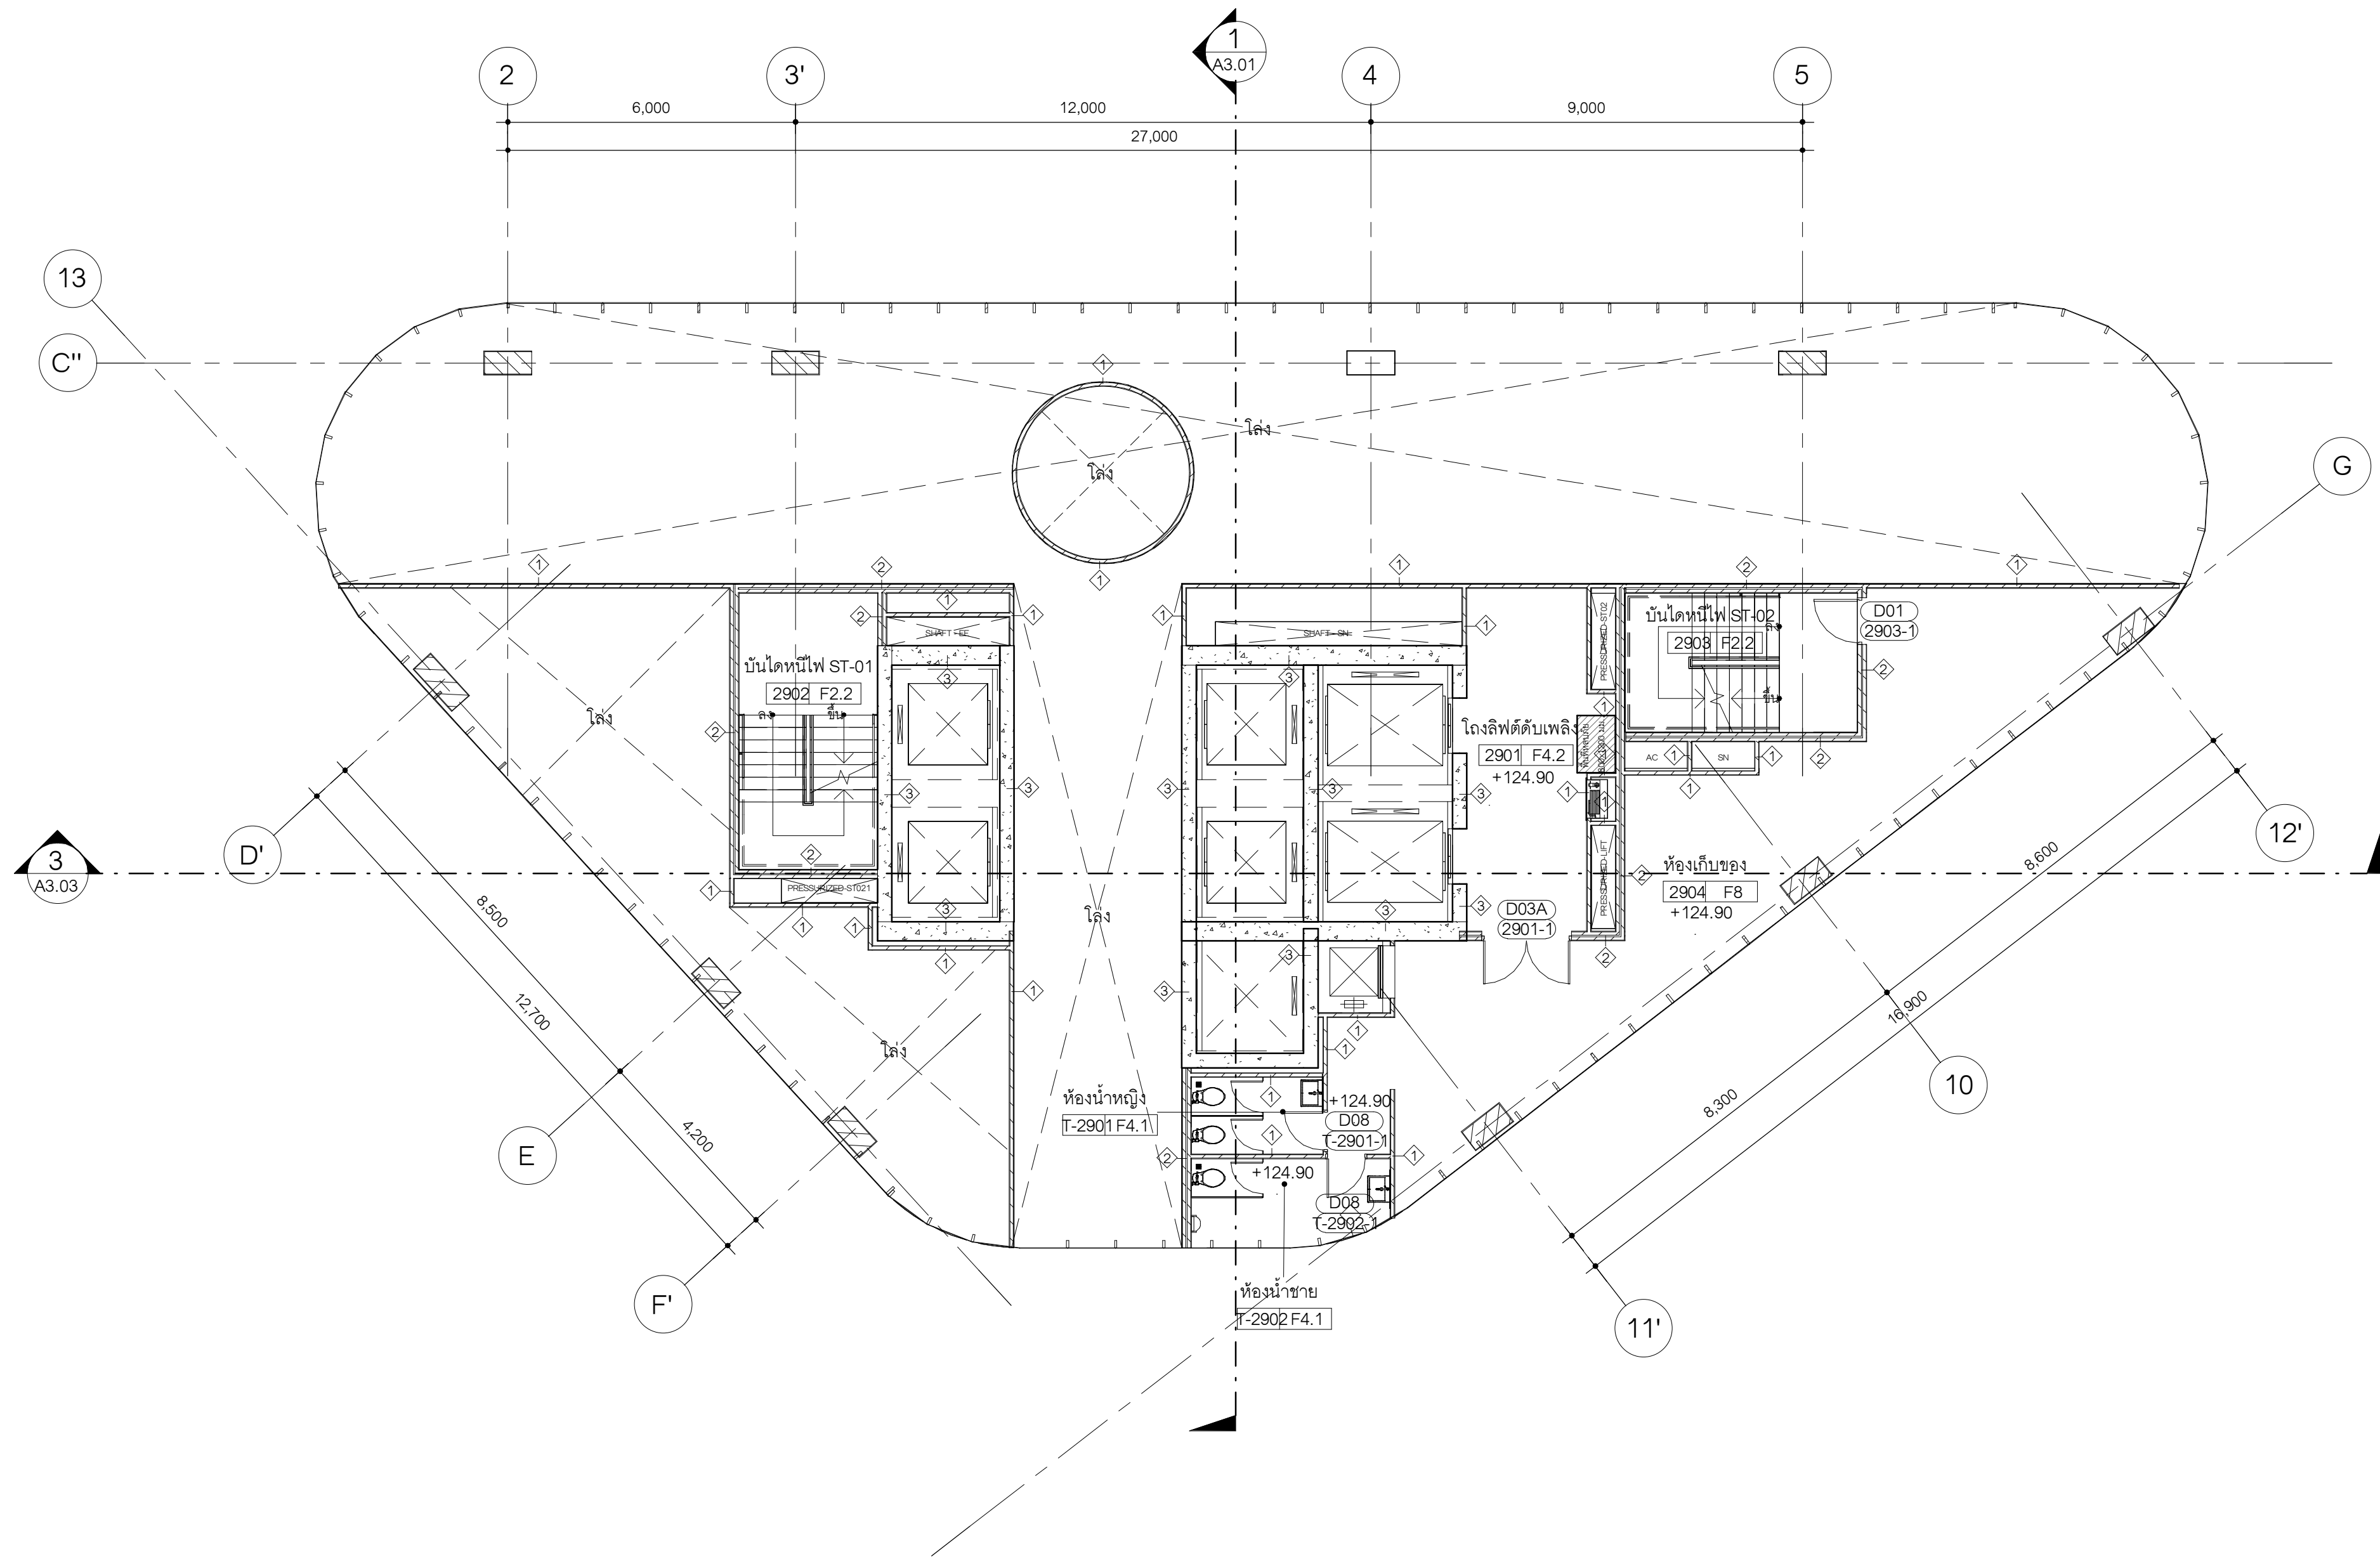

ผังพื้นที่ 29
มาตราส่วน 1 : 100

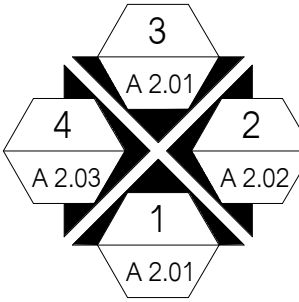

OWNER
LUXURY HOTEL DEVELOPMENT
SUKHUMVIT 38 CO., LTD.

DESIGNER
ARCHITECTS 49 LIMITED
81 SUKHUMVIT 26
BANGKOK 10110 THAILAND
T + 66 (0) 2260 4370
F + 66 (0) 2259 3872
E A49@A49.CO.TH
W A49.CO.TH

A | 49

K.C.S. & ASSOCIATES CO. LTD.
22ND FLOOR, CHARN ISSARA TOWER II
2592/267 NEW PETCHABURI ROAD, BANGKAPI,
HUAY KWANG, BAKOK 10310 THAILAND
T +66 (0) 2308 2481 5
F +66 (0) 2308 2485

KCS
K.C.S. & ASSOCIATES CO. LTD.

MEC PRO DESIGN CO. LTD.
567 BUILDING 4TH RAMA IX SOI 51
SUAN LUANG, BANGKOK 10250 THAILAND
T +66 (0) 2170 8029
+66 (0) 97 034 8917
E MECPRO.DESIGN@GMAIL.COM

MEC PRO
DESIGN

P LANDSCAPE CO. LTD.
59/3 SUKHUMVIT 39, KLONGTON NUA,
WATTANA, BANGKOK 10110 THAILAND
T (622) 261 3700 TO 9
F (622) 238 3388
E INFO@PLANDSCAPE.COM
W WWW.PLANDSCAPE.COM

pla | | |

ARCHITECTS				SIGNED
พิธีชัย	วงศ์ไวศยวรรณ	วสท.509		
เนรศักดิ์	อ.วิจิตร	วสท.720		
จารุวัฒน์	อ.วิเศษศักดิ์	วสท.769		
พิณมร	อ.พนธ์ศักดิ์	สท.3432		
สุชาภา	ศรีสมบูรณ์	สท.3347		
ปาริชาติ	จินนีน้อย	วสท.20910		
คสพร	ศิริพจน์	วสท.23830		
วันธรณ์	พลสวัสดิ์	วสท.27171		

STRUCTURAL ENGINEER				SIGNED
ภาณุ	จันทราวุธ	ว.1023		
กุลศิริ	จันทราวุธ	ส.9572		
ภาณุ	สายวณภูมิ	ส.15169		
อภิสิทธิ์	สมชาย	ว.69140		

ELECTRICAL ENGINEER				SIGNED
ชาน	นิมิต	วท.1118		
พนศักดิ์	พิรุณ	สท.1586		
ธนวัฒน์	น้อยจ้อย	วท.63548		

MECHANICAL ENGINEER				SIGNED
เบน	โชพงษ์	ส.3566		
ณภัทร	วิเชษฐพทยาน	ว.51086		
วิฑร	บุญนิยม	ว.52030		

ENVIRONMENTAL ENGINEER				SIGNED
ทรงวุฒิ	วิเศษศิลป์	ส.625		
เบน	โชพงษ์	ว.112		
วสุ	ละลาขบป	ว.7507		

SANITARY ENGINEER				SIGNED
ช่อ	นามสกุล	เลขใบอนุญาต		

LANDSCAPE ARCHITECT				SIGNED
นัท	รณศิริโพธิ์	สท.108		

GENERAL NOTE
1. THIS DRAWING IS THE PROPERTY OF ARCHITECTS 49 LIMITED OR ONE OF ITS AFFILIATES. IT IS ISSUED SUBJECT TO RETURN UPON DEMAND AND IS NOT TO BE USED EXCEPT IN CONNECTION WITH THE PROJECT FOR WHICH IT IS INTENDED.
2. DO NOT SCALE THIS DRAWING. USE FIGURED DIMENSIONS ONLY.
ไม่ใช้ตัวเลงที่กหนดไว้เท่านั้น ห้ามวัดจากแบบ


PROJECT NAME
THE OKURA PRESTIGE
SUKHUMVIT BANGKOK HOTEL
AND SPA

DRAWING TITLE
ผังพื้นที่ 29


ISSUE/REVISION			
NO	DESCRIPTION	BY	DATE
1	แบบแปลนสถาปัตย์	A49	17/04/2569

CHECK BY		DRAWING NO.	
ARCHITECT	SIGNED	A1.29	
PM			
PD			
PA			
JC			
DRAWN BY		SCALE: 1 : 100	
PRINTED DATE		REF. FILE	
17/04/2569			

4/18/2026 3:17:08 PM

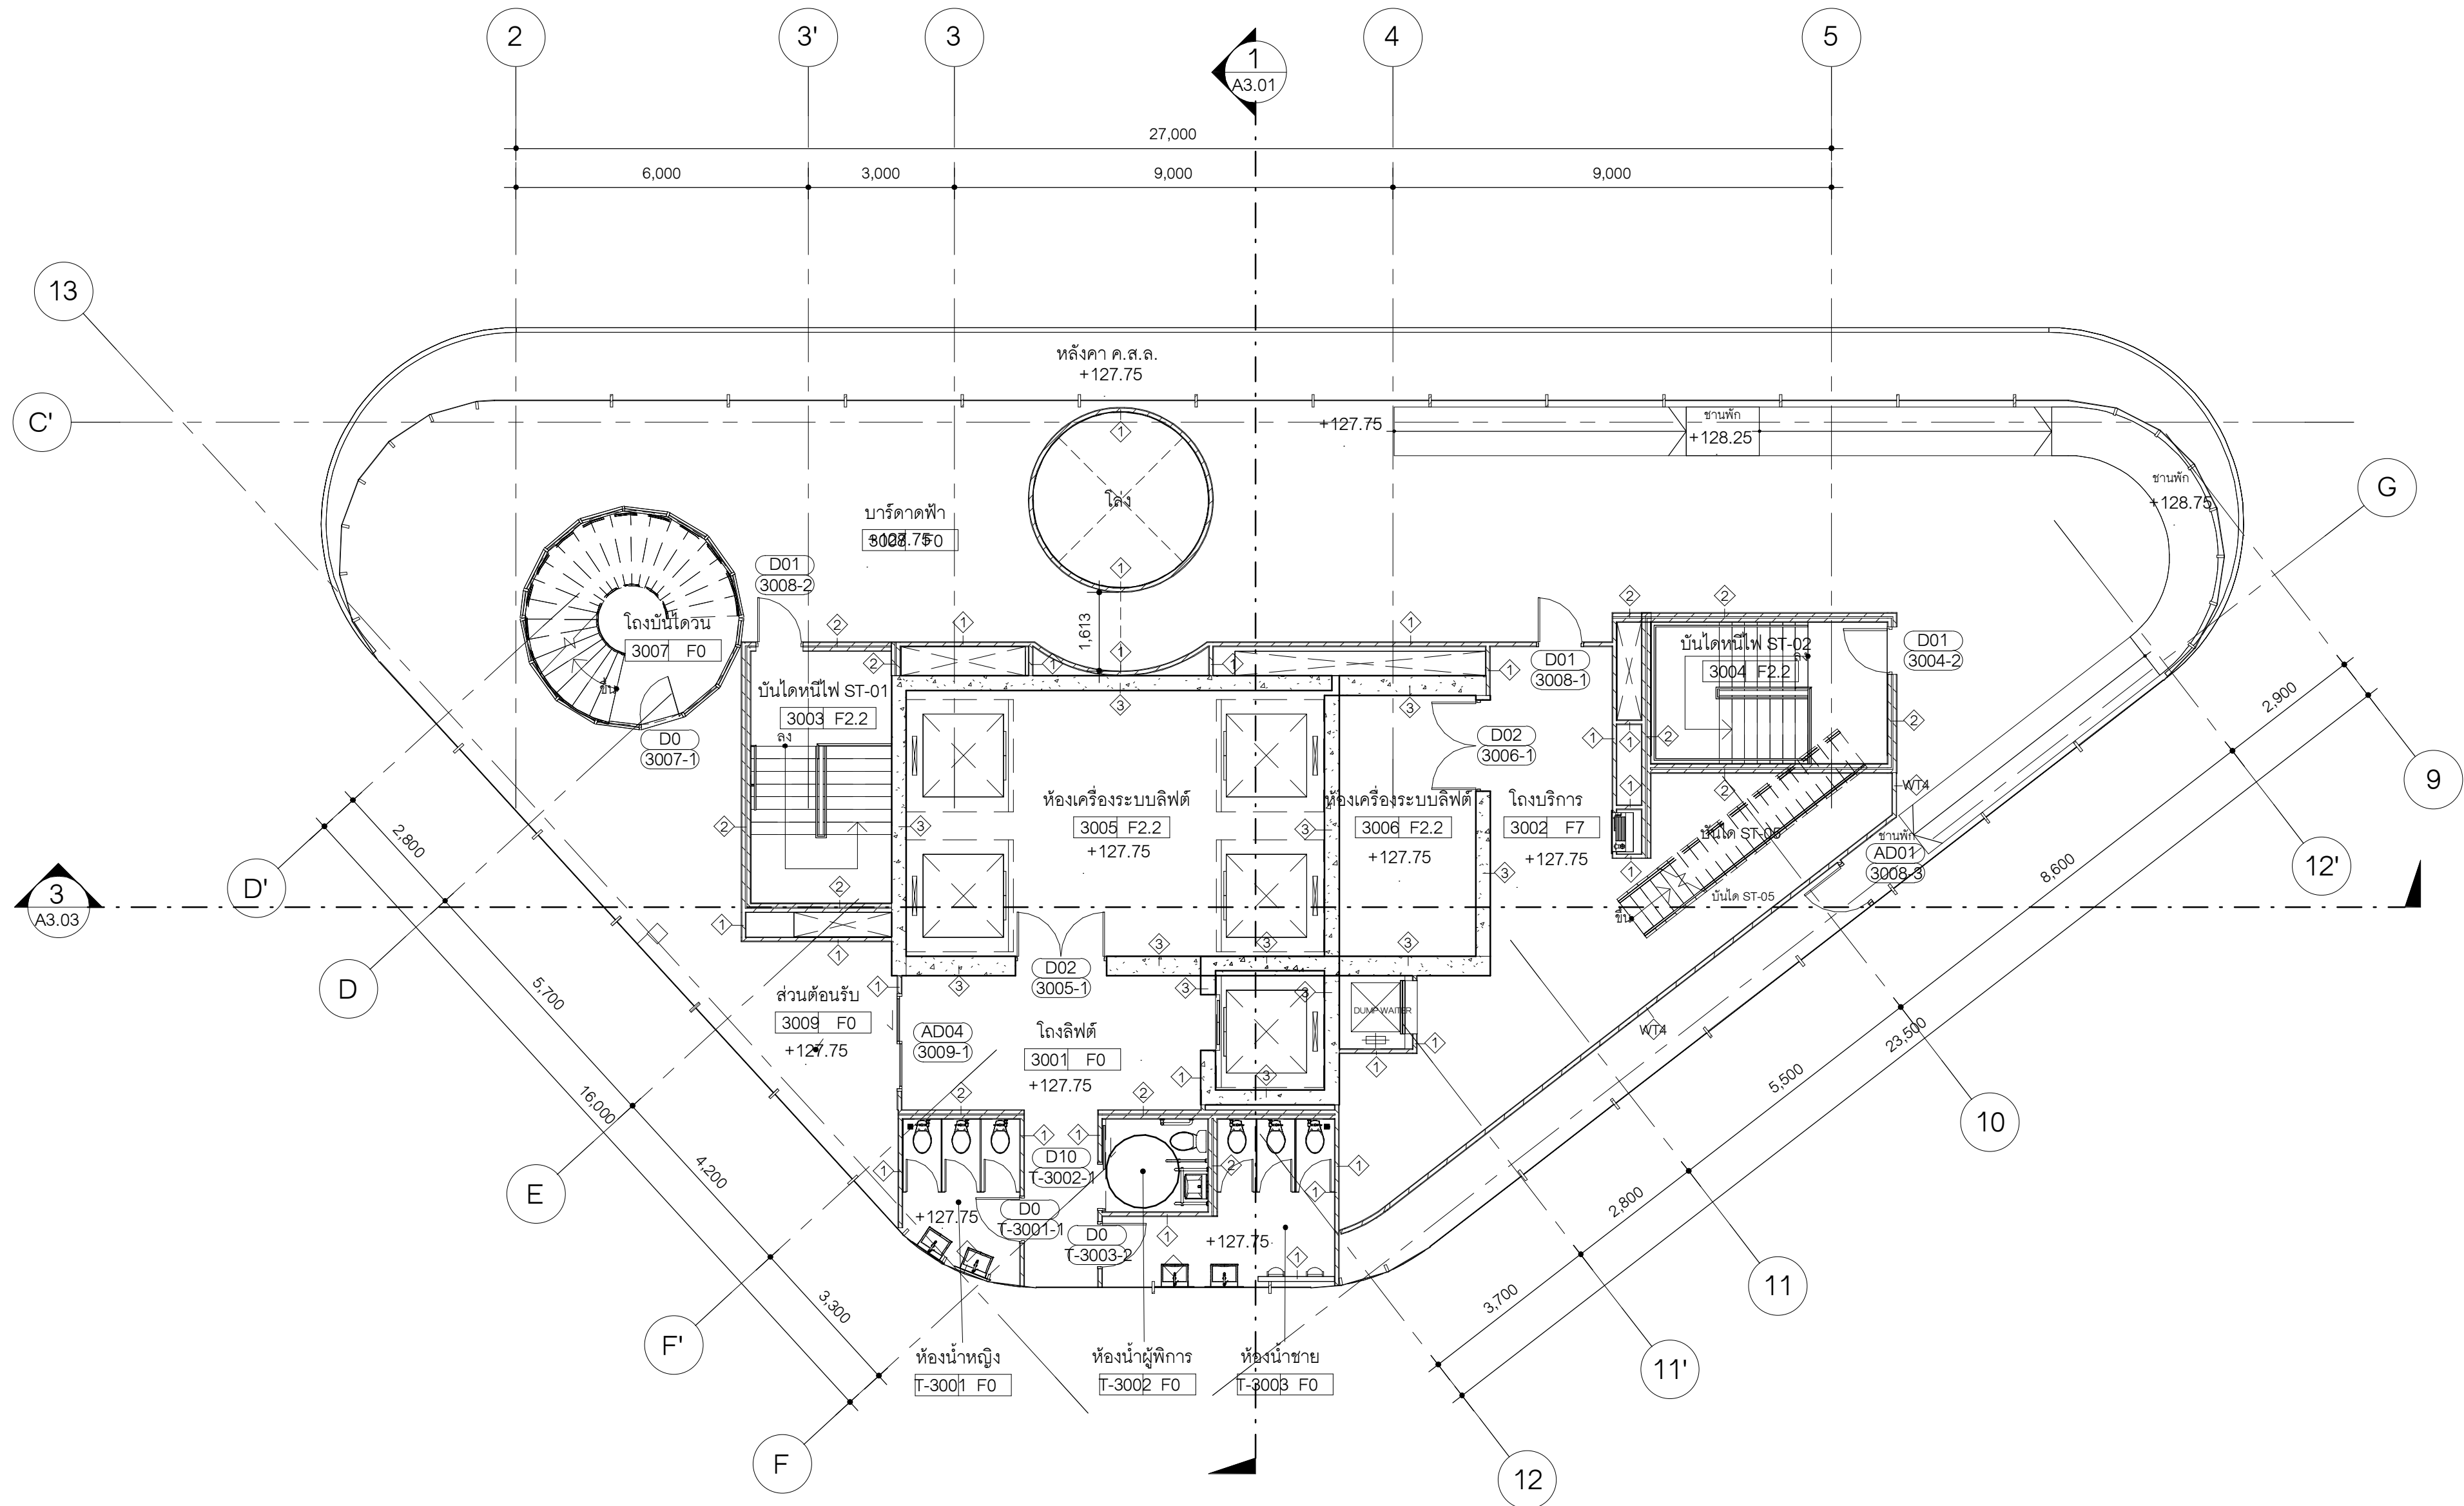

ผังพื้นที่ขนาดพื้นที่
มาตราส่วน 1 : 100

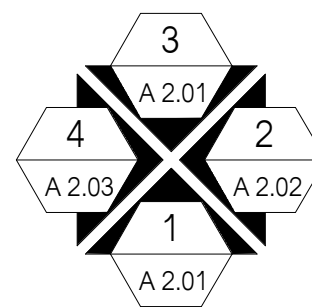

TRUE NORTH
PLAN NORTH

OWNER
LUXURY HOTEL DEVELOPMENT
SUKHUMVIT 38 CO., LTD.

DESIGNER
ARCHITECTS 49 LIMITED
81 SUKHUMVIT 26
BANGKOK 10110 THAILAND
T + 66 (0) 2260 4370
F + 66 (0) 2259 3872
E A49@A49.CO.TH
W A49.CO.TH

A 49

K.C.S. & ASSOCIATES CO. LTD.
22ND FLOOR, CHARN ISSARA TOWER II
2592/267 NEW PETCHABURI ROAD, BANGKAPI,
HUAY KWANG, BAKOK 10310 THAILAND
T +66 (0) 2308 2481 5
F +66 (0) 2308 2485

KCS
K.C.S. & ASSOCIATES CO. LTD.

MEC PRO DESIGN CO. LTD.
567 BUILDING 4TH FLOOR, SUKUMVIT 38
SUAN LUANG, BANGKOK 10250 THAILAND
T +66 (0) 2170 8029
+66 (0) 97 034 8917
E MECPRO.DESIGN@GMAIL.COM

MEC PRO
DESIGN

P LANDSCAPE CO. LTD.
59/3 SUKHUMVIT 39, KLONGTUN NUA,
WATTANA, BANGKOK 10110 THAILAND
T (622) 261 3700 TO 9
F (622) 239 3388
E INFO@PLANDSCAPE.COM
W WWW.PLANDSCAPE.COM

pla | | |

ARCHITECTS
ชื่อ วรวิทย์ วรวิทย์ วรวิทย์ วรวิทย์
ตำแหน่ง วรวิทย์ วรวิทย์ วรวิทย์ วรวิทย์
ตำแหน่ง วรวิทย์ วรวิทย์ วรวิทย์ วรวิทย์
SIGNED

STRUCTURAL ENGINEER
นาย จันทราวุธ วรวิทย์ วรวิทย์ วรวิทย์
นาย จันทราวุธ วรวิทย์ วรวิทย์ วรวิทย์
นาย จันทราวุธ วรวิทย์ วรวิทย์ วรวิทย์
นาย จันทราวุธ วรวิทย์ วรวิทย์ วรวิทย์
นาย จันทราวุธ วรวิทย์ วรวิทย์ วรวิทย์
นาย จันทราวุธ วรวิทย์ วรวิทย์ วรวิทย์
นาย จันทราวุธ วรวิทย์ วรวิทย์ วรวิทย์
นาย จันทราวุธ วรวิทย์ วรวิทย์ วรวิทย์

SIGNED

ELECTRICAL ENGINEER
นาย นันทกร วรวิทย์ วรวิทย์ วรวิทย์
นาย นันทกร วรวิทย์ วรวิทย์ วรวิทย์
นาย นันทกร วรวิทย์ วรวิทย์ วรวิทย์
นาย นันทกร วรวิทย์ วรวิทย์ วรวิทย์
นาย นันทกร วรวิทย์ วรวิทย์ วรวิทย์
นาย นันทกร วรวิทย์ วรวิทย์ วรวิทย์
นาย นันทกร วรวิทย์ วรวิทย์ วรวิทย์
นาย นันทกร วรวิทย์ วรวิทย์ วรวิทย์

SIGNED

MECHANICAL ENGINEER
นาย ชัยวัฒน์ วรวิทย์ วรวิทย์ วรวิทย์
นาย ชัยวัฒน์ วรวิทย์ วรวิทย์ วรวิทย์
นาย ชัยวัฒน์ วรวิทย์ วรวิทย์ วรวิทย์
นาย ชัยวัฒน์ วรวิทย์ วรวิทย์ วรวิทย์
นาย ชัยวัฒน์ วรวิทย์ วรวิทย์ วรวิทย์
นาย ชัยวัฒน์ วรวิทย์ วรวิทย์ วรวิทย์
นาย ชัยวัฒน์ วรวิทย์ วรวิทย์ วรวิทย์
นาย ชัยวัฒน์ วรวิทย์ วรวิทย์ วรวิทย์

SIGNED

ENVIRONMENTAL ENGINEER
นางสาว วิภาดา วรวิทย์ วรวิทย์ วรวิทย์
นางสาว วิภาดา วรวิทย์ วรวิทย์ วรวิทย์
นางสาว วิภาดา วรวิทย์ วรวิทย์ วรวิทย์
นางสาว วิภาดา วรวิทย์ วรวิทย์ วรวิทย์
นางสาว วิภาดา วรวิทย์ วรวิทย์ วรวิทย์
นางสาว วิภาดา วรวิทย์ วรวิทย์ วรวิทย์
นางสาว วิภาดา วรวิทย์ วรวิทย์ วรวิทย์
นางสาว วิภาดา วรวิทย์ วรวิทย์ วรวิทย์

SIGNED

SANITARY ENGINEER
ชื่อ นามสกุล เลขใบอนุญาต
ชื่อ นามสกุล เลขใบอนุญาต
ชื่อ นามสกุล เลขใบอนุญาต
ชื่อ นามสกุล เลขใบอนุญาต
ชื่อ นามสกุล เลขใบอนุญาต
ชื่อ นามสกุล เลขใบอนุญาต
ชื่อ นามสกุล เลขใบอนุญาต
ชื่อ นามสกุล เลขใบอนุญาต

SIGNED

LANDSCAPE ARCHITECT
นาย วรรณวิทย์ วรวิทย์ วรวิทย์ วรวิทย์
นาย วรรณวิทย์ วรวิทย์ วรวิทย์ วรวิทย์
นาย วรรณวิทย์ วรวิทย์ วรวิทย์ วรวิทย์
นาย วรรณวิทย์ วรวิทย์ วรวิทย์ วรวิทย์
นาย วรรณวิทย์ วรวิทย์ วรวิทย์ วรวิทย์
นาย วรรณวิทย์ วรวิทย์ วรวิทย์ วรวิทย์
นาย วรรณวิทย์ วรวิทย์ วรวิทย์ วรวิทย์
นาย วรรณวิทย์ วรวิทย์ วรวิทย์ วรวิทย์

SIGNED

GENERAL NOTE
1. THIS DRAWING IS THE PROPERTY OF ARCHITECTS 49 LIMITED OR
ONE OF ITS AFFILIATES. IT IS ISSUED SUBJECT TO RETURN UPON
DEMAND AND IS NOT TO BE USED EXCEPT IN CONNECTION WITH THE
PROJECT FOR WHICH IT IS INTENDED.
2. DO NOT SCALE THIS DRAWING. USE FIGURED DIMENSIONS ONLY.
ไม่ใช้ตัวเลขวัดขนาดจากแบบ

PROJECT NAME
THE OKURA PRESTIGE
SUKHUMVIT BANGKOK HOTEL
AND SPA

DRAWING TITLE
ผังพื้นที่ขนาดพื้นที่


ISSUE/REVISION
NO DESCRIPTION BY DATE
1 แก้ไขแบบสถาปัตย์ A49 17/04/2569

CHECK BY DRAWING NO.



ARCHITECT SIGNED
PM
PD
PA
JC

A1.30

DRAWN BY Author SCALE: 1 : 100
PRINTED DATE 17/04/2569 REF. FILE

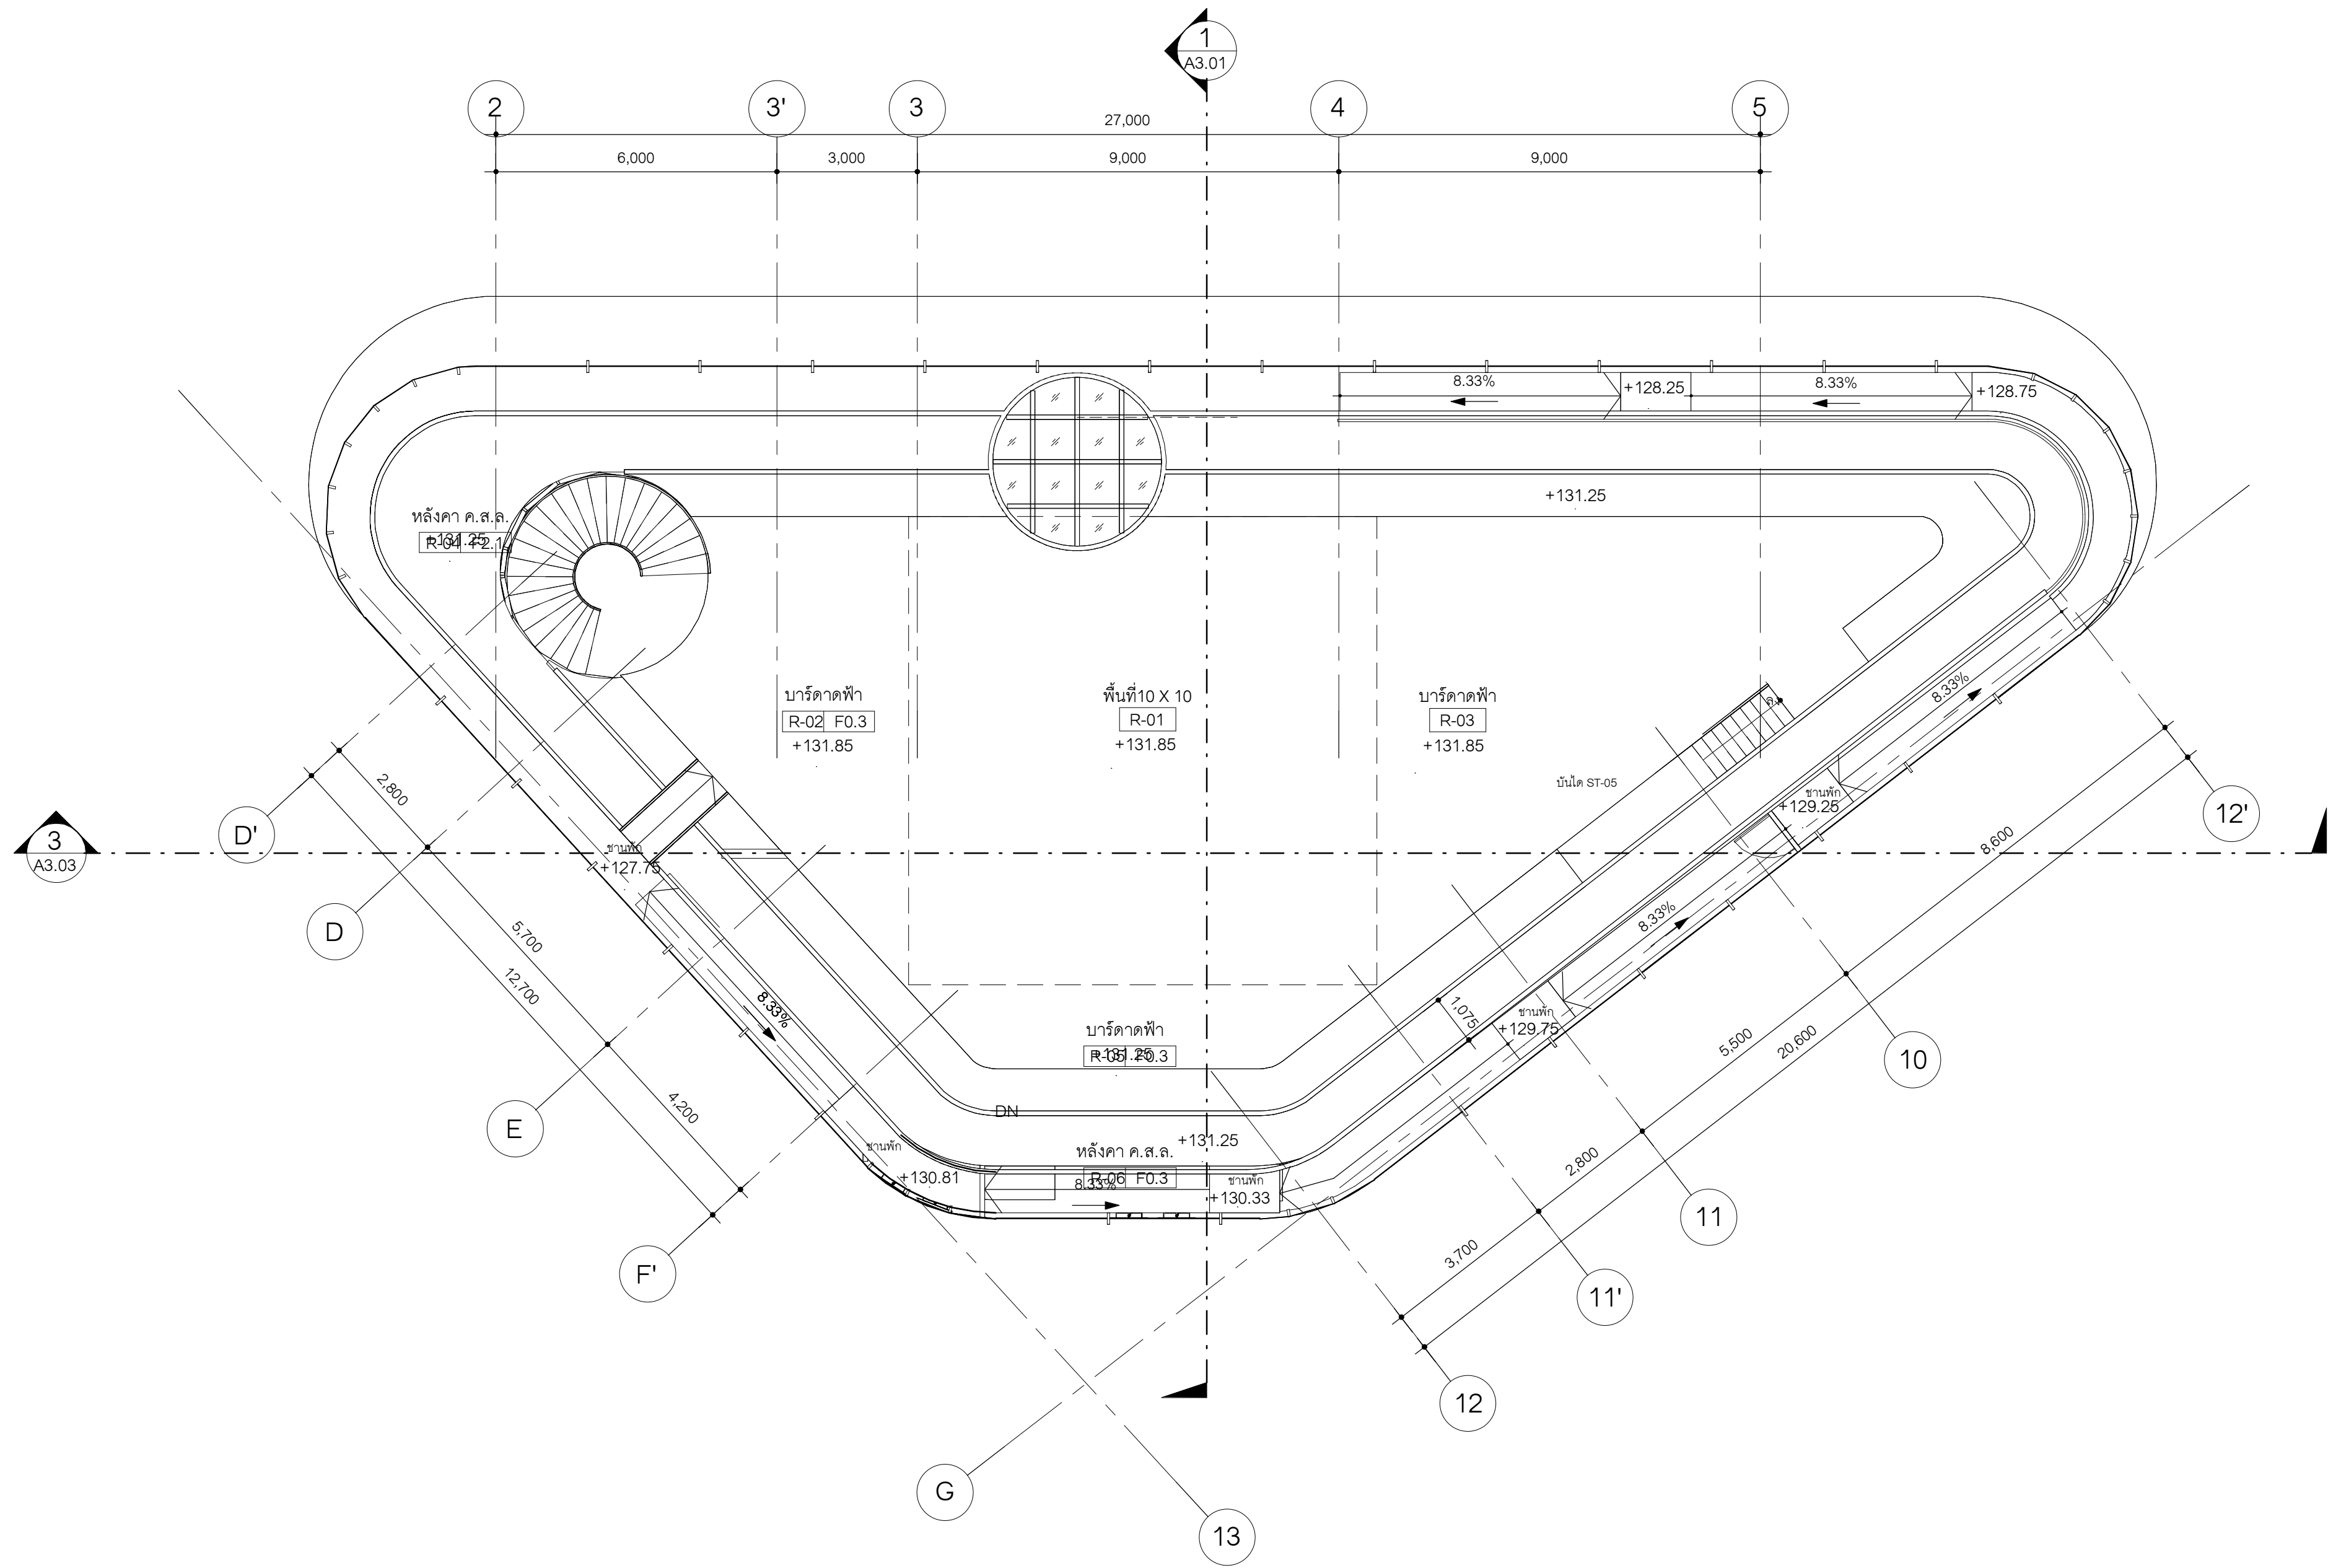

ผังพื้นที่ 10x10
มาตราส่วน 1 : 100

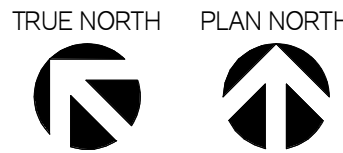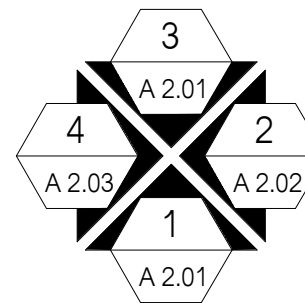

OWNER
LUXURY HOTEL DEVELOPMENT
SUKHUMVIT 38 CO., LTD.

DESIGNER
ARCHITECTS 49 LIMITED
81 SUKHUMVIT 26
BANGKOK 10110 THAILAND
T + 66 (0) 2260 4370
F + 66 (0) 2259 3872
E A49@A49.CO.TH
W A49.CO.TH

A | 49

K.C.S. & ASSOCIATES CO.LTD.
22ND FLOOR, CHARN ISSARA TOWER II
2592/267 NEW PETCHABURI ROAD, BANGKAPI,
HUAY KWANG, BAKOK 10310 THAILAND
T +66 (0) 2308 2481 5
F +66 (0) 2308 2485

KCS
K.C.S. & ASSOCIATES CO.LTD.

MEC PRO DESIGN CO.LTD.
567 BUILDING 4TH FLOOR, SUAN LUANG, BANGKOK 10250 THAILAND
T +66 (0) 2170 8029
+66 (0) 97 034 8917
E MECPRO.DESIGN@GMAIL.COM

MEC PRO
DESIGN

P.LANDSCAPE CO.LTD.
59/3 SUKHUMVIT 39, KLONGTON NUA,
WATTANA, BANGKOK 10110 THAILAND
T (622) 261 3700 TO 9
F (622) 239 3388
E INFO@PLANDSCAPE.COM
W WWW.PLANDSCAPE.COM

pla | | |

ARCHITECTS			SIGNED
พี่ชัย	วงศ์โหวตวรรณ	วสท.509	
ณรงค์ชัย	อ.วิจิตร	วสท.720	
จารุวัฒน์	อ.วิเศษศักดิ์	วสท.769	
พิณพร	อ.พนธ์ศักดิ์	สท.3432	
สุชาดา	ศรีสมบุญ	สท.3347	
ปาริชาติ	จินนีน้อย	วสท.20910	
คสพร	ศิริพจน์	วสท.23830	
วันธรณ์	พลสวัสดิ์	วสท.27171	

STRUCTURAL ENGINEER			SIGNED
การุญ	จันทรางศุ	วส.1023	
กุลศิริ	จันทรางศุ	ส.9572	
ภาส	สายรวมญาติ	ส.15169	
อภิสิทธิ์	สมชาย	วส.69140	

ELECTRICAL ENGINEER			SIGNED
ชานน	นิมิต	วท.1118	
พนธ์ศักดิ์	พิรุณ	สท.1586	
ธนวัฒน์	น้อยจ้อย	วท.63548	

MECHANICAL ENGINEER			SIGNED
เบน	โชพงษ์	ส.3566	
ณภัทร	วิเชษฐพทยาน	ว.51086	
วิฑร	บุญนิยม	ว.52030	

ENVIRONMENTAL ENGINEER			SIGNED
ทรงวุฒิ	วิเศษศิลป์	ส.625	
เบน	โชพงษ์	ว.112	
วสุ	ละลาชนา	ว.7507	

SANITARY ENGINEER			SIGNED
ธีร	นามสกุล	ส.108	

LANDSCAPE ARCHITECT			SIGNED
นัท	รณศิริโพธิ์	ส.108	

GENERAL NOTE
1. THIS DRAWING IS THE PROPERTY OF ARCHITECTS 49 LIMITED OR ONE OF ITS AFFILIATES. IT IS ISSUED SUBJECT TO RETURN UPON DEMAND AND IS NOT TO BE USED EXCEPT IN CONNECTION WITH THE PROJECT FOR WHICH IT IS INTENDED.
2. DO NOT SCALE THIS DRAWING. USE FIGURED DIMENSIONS ONLY.
ให้ใช้ค่าเลขที่กำหนดไว้เท่านั้น ห้ามวัดจากแบบ

PROJECT NAME
THE OKURA PRESTIGE
SUKHUMVIT BANGKOK HOTEL
AND SPA

DRAWING TITLE
ผังพื้นที่ 10x10


ISSUE/REVISION			
NO	DESCRIPTION	BY	DATE
1	แบบแปลนอาคาร	A49	17/04/2569

CHECK BY **DRAWING NO.**

ARCHITECT	SIGNED	
PD		
PA		
JC		

DRAWN BY **Author** SCALE: **1:100**
PRINTED DATE **17/04/2569** REF. FILE

A1.31

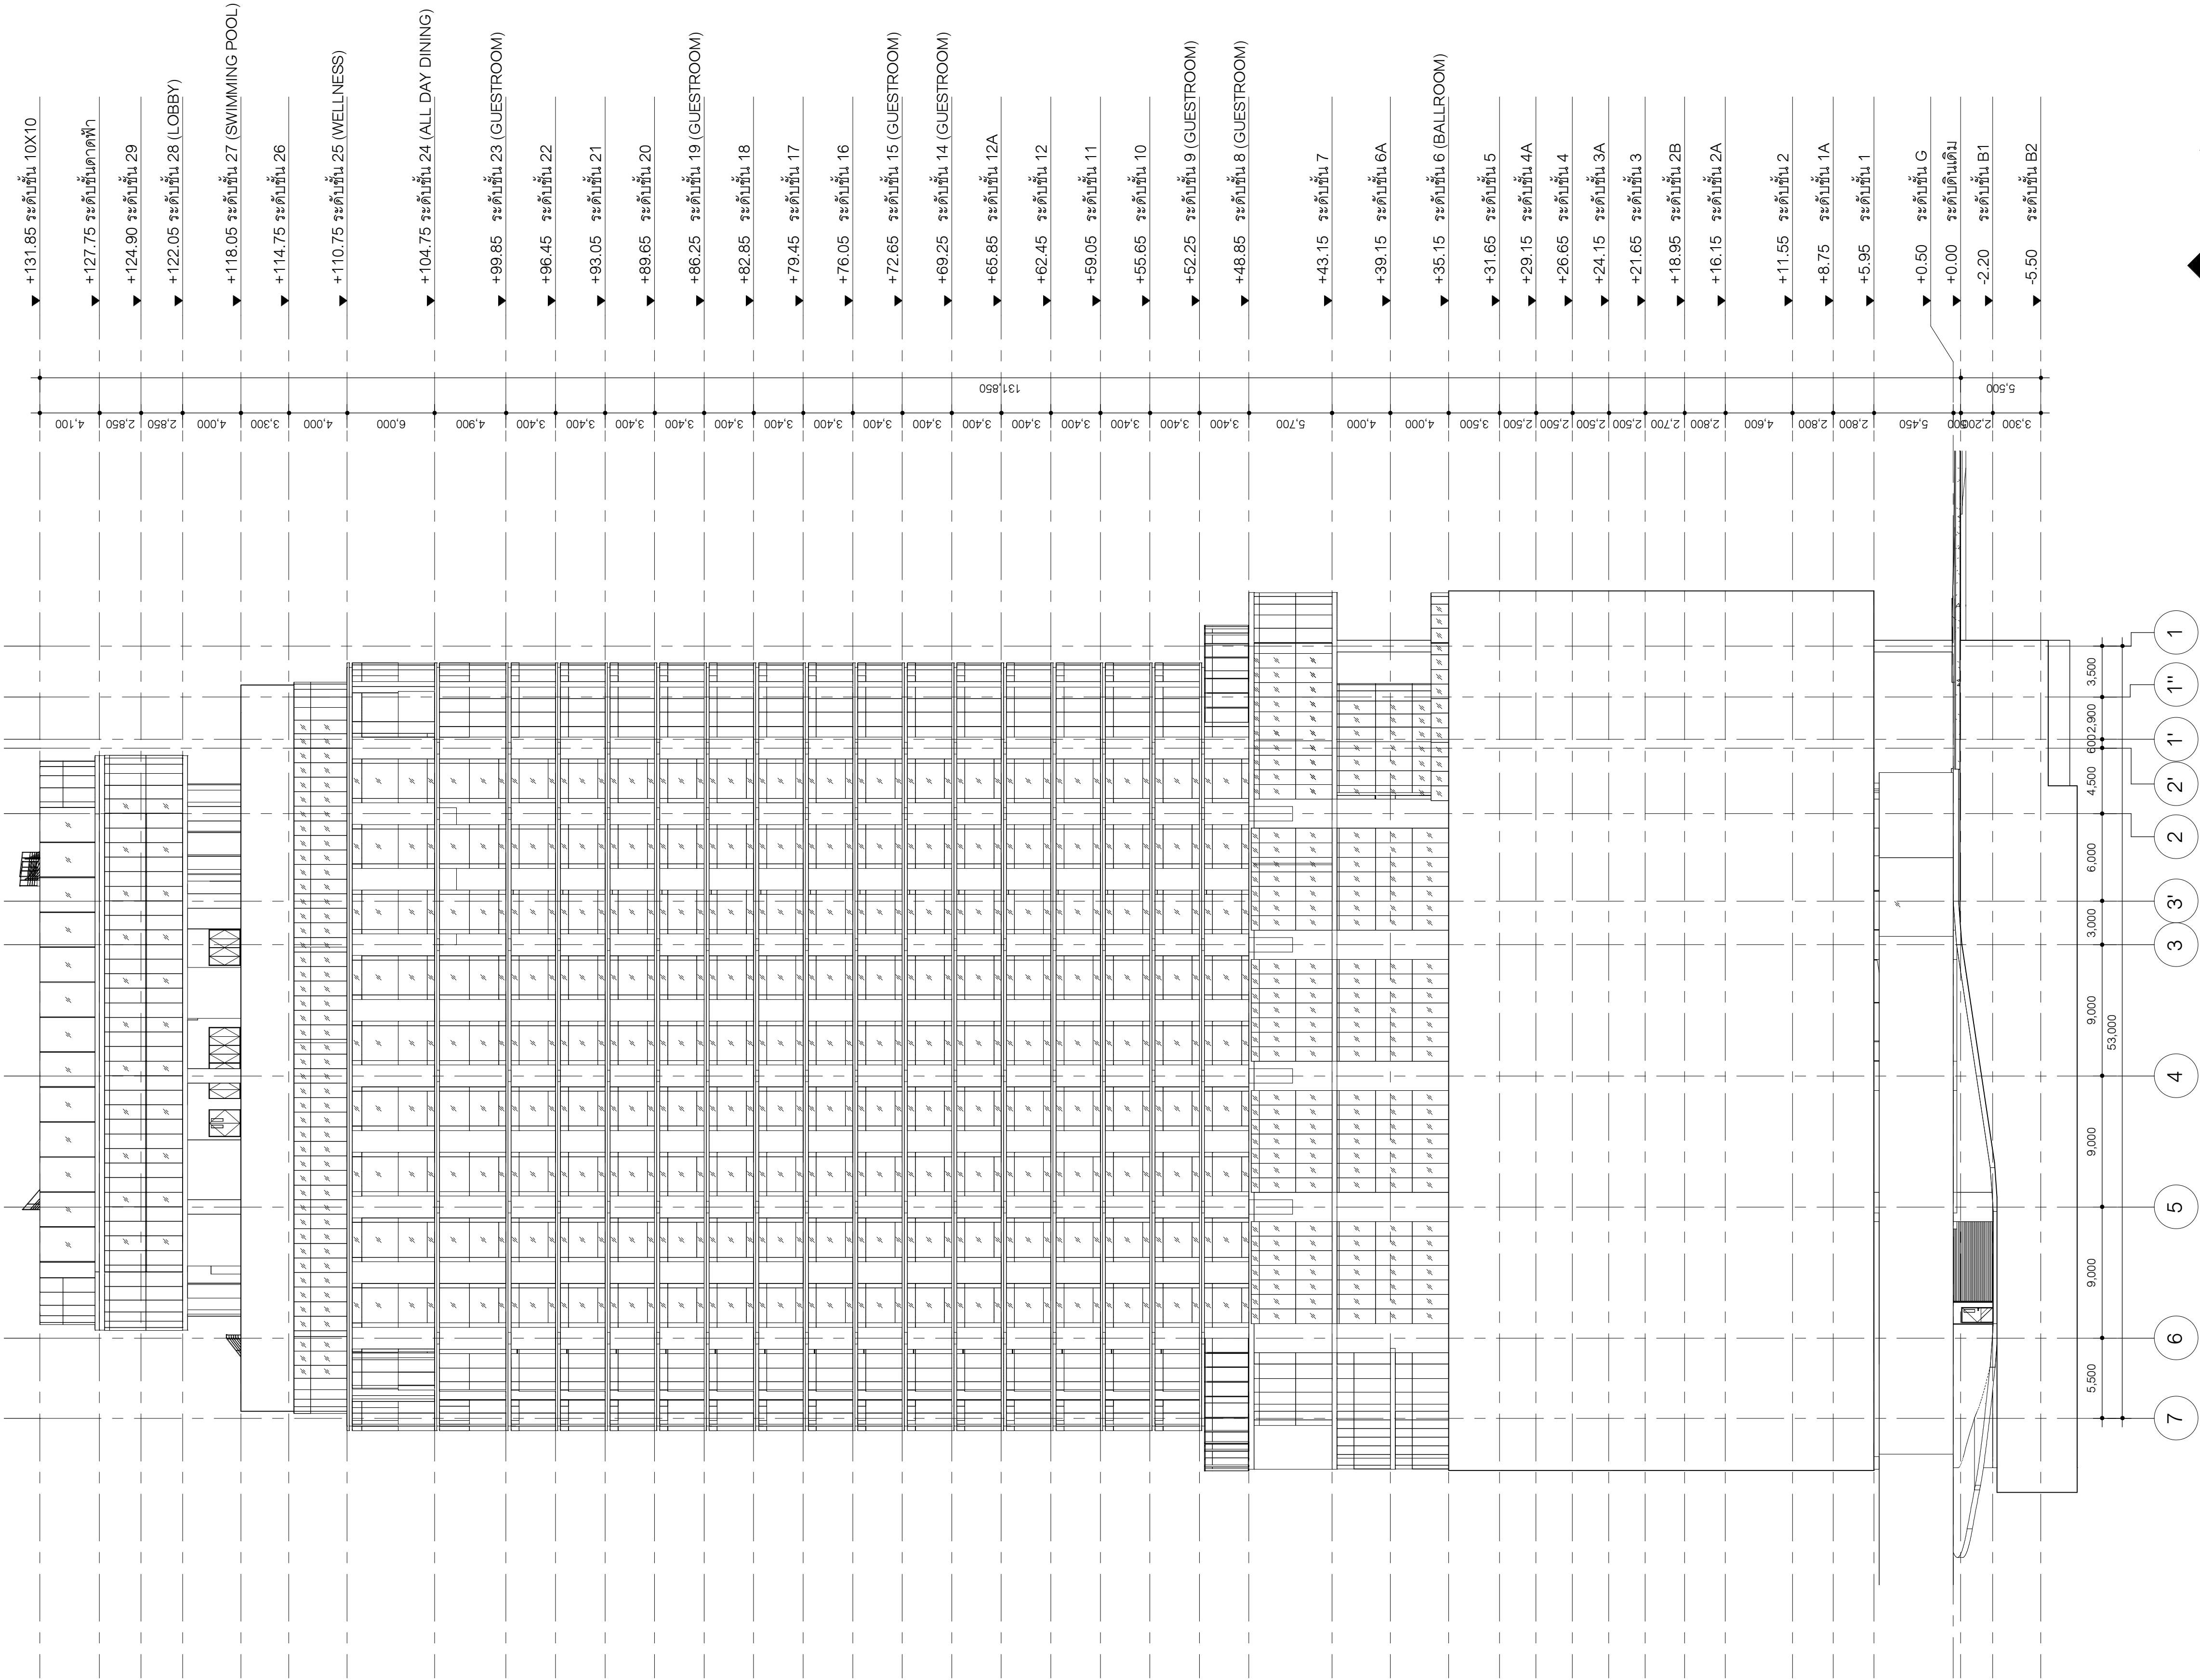

OWNER
LUXURY HOTEL DEVELOPMENT
SUKHUMVIT 38 CO., LTD.

DESIGNER
ARCHITECTS 49 LIMITED
81 SUKHUMVIT 26
BANGKOK 10110 THAILAND
T +66 (0) 2260 4370
F +66 (0) 2259 3872
E A49@A49.CO.TH
W A49.CO.TH

K.C.S. & ASSOCIATES CO. LTD.
22ND FLOOR, CHARN ISSARA TOWER II
2522/267 NEW PETCHABURI ROAD, BANGKAPI,
HUAY KWANG, BANGKOK 10310 THAILAND
T +66 (0) 270 8029
F +66 (0) 2308 2481 5
E MECPRO.DESIGN@GMAIL.COM

MEC PRO DESIGN CO. LTD.
57 BUILDING 4TH FLOOR, 1X SOI 51
SUAN LUANG, BANGKOK 10250 THAILAND
T (622) 251 3700 TO 9
F (622) 258 3388
E INFO@PLANDSCAPE.COM
W WWW.PLANDSCAPE.COM

P LANDSCAPE CO. LTD.
59/3 SUKHUMVIT 39, KLONGTON NUA,
WATTANA, BANGKOK 10110 THAILAND
T (622) 251 3700 TO 9
F (622) 258 3388
E INFO@PLANDSCAPE.COM
W WWW.PLANDSCAPE.COM

ARCHITECTS			SIGNED
พิธีชัย วงศ์ไวศยวรรณ	วสท.509		
เนตรศศิวิทย์ อารีมิตร	วสท.720		
จารุวิมลศักดิ์ อรุณเกียรติศักดิ์	วสท.769		
พิชญ์พร อรุณศักดิ์	วสท.3432		
สุชภา ศรีสมบูรณ์	วสท.3347		
ปวีร์ศักดิ์ หิวนนินไวย	วสท.20910		
ศสพร ศิริพาน	วสท.23830		
วริศรณัน พูลสวัสดิ์	วสท.27171		

STRUCTURAL ENGINEER			SIGNED
กาญจนา จันทวงศ	วบ.1023		
กุลศิริ จันทวงศ	วบ.9572		
ภาณุ สายรวมญาติ	วบ.15169		
อภิสิทธิ์ สมอียง	วบ.69140		

ELECTRICAL ENGINEER			SIGNED
ชานน นิ่มตรง	วพท.1118		
ชนัดดีศักดิ์ พิกุลสง	วพท.1586		
ชนวิวัฒน์ น้อยจ้อย	วพท.63548		

MECHANICAL ENGINEER			SIGNED
เบนศ ไชยพงษ์	วสท.3566		
ณภัทร วิเชียรเมฆาเขต	วสท.51086		
วิฑรศักดิ์ บุญวิเศษ	วสท.52030		

ENVIRONMENTAL ENGINEER			SIGNED
ทรงวุฒิ วิเศษศิลป์	วสท.625		
เบนศ ไชยพงษ์	วสท.112		
วสุ ละครยาบ	วสท.7507		

SANITARY ENGINEER			SIGNED
ชื้อ นามสกุล	เลขใบอนุญาต		

LANDSCAPE ARCHITECT			SIGNED
นัทธกร รามศิริโยธิน	วสท.108		

GENERAL NOTE
1. THIS DRAWING IS THE PROPERTY OF ARCHITECTS 49 LIMITED OR ONE OF ITS AFFILIATES. IT IS ISSUED SUBJECT TO RETURN UPON DEMAND AND IS NOT TO BE USED EXCEPT IN CONNECTION WITH THE PROJECT FOR WHICH IT IS INTENDED.
2. DO NOT SCALE THIS DRAWING. USE FIGURED DIMENSIONS ONLY.
ให้ใช้ตัวเลขที่กำหนดไว้เท่านั้น ห้ามวัดจากแบบ

PROJECT NAME
THE OKURA PRESTIGE
SUKHUMVIT BANGKOK HOTEL
AND SPA

DRAWING TITLE
รูปด้าน 1

ISSUE/REVISION			
NO	DESCRIPTION	BY	DATE
1	แบบแปลนสถาปัตย์	A49	17/04/2569

CHECK BY		DRAWING NO.	
ARCHITECT	SIGNED		
PM			
PD			
PA			
JC			

DRAWN BY Author
PRINTED DATE 17/04/2569
SCALE: 1 : 250
REF. FILE

A | 49

KCS
K.C.S. & ASSOCIATES CO. LTD.

MEC PRO
DESIGN

pla